
Дизайн-проект квартиры 20

6 этаж · г. Салехард
планировочное решение №148, вариант 1
72,8 м² · 13,0 × 6,0 м внутри

Рабочий альбом: визуализации, планы, развёртки, ведомости.
Выполнено по 3D-модели квартиры; размеры проектные, до контрольного обмера.
октябрь 2026 г.

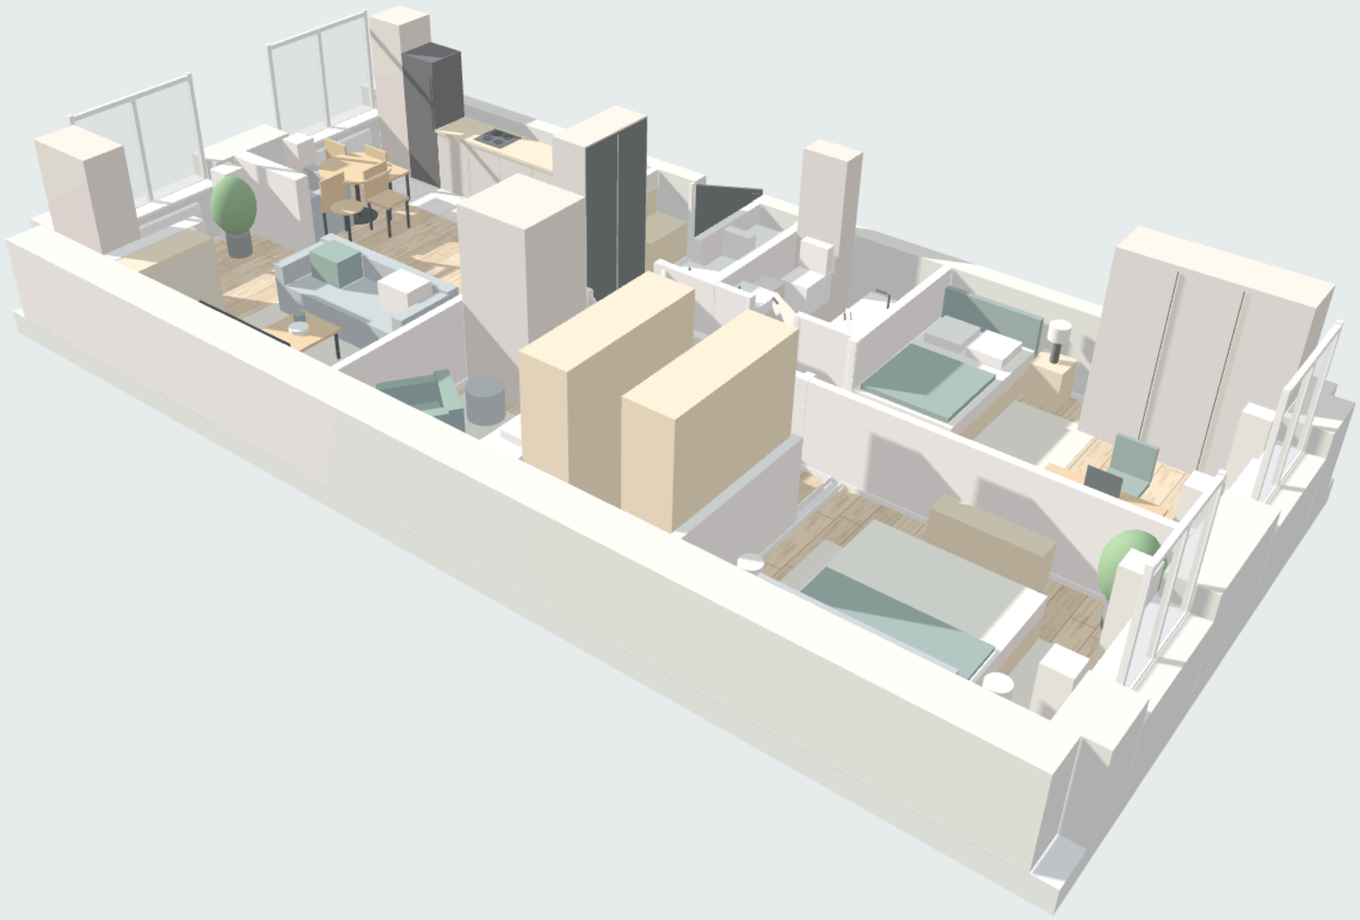

Содержание альбома

Лист	Наименование
01	Обложка
02	Содержание
03	Пояснительная записка
04	Общий вид квартиры Отделка «Светлая» (основная)
05	Визуализация прихожей Ракурс 1
06	Визуализация прихожей Ракурс 2
07	Визуализация кухни-гостиной Ракурс 3
08	Визуализация кухни-гостиной Ракурс 4
09	Визуализация кухни-гостиной Ракурс 5
10	Визуализация кухни-гостиной Ракурс 6
11	Визуализация кухни-гостиной Ракурс 7, вечернее освещение
12	Визуализация холла Ракурс 8
13	Визуализация гостевого санузла Ракурс 9, вид сверху (стены срезаны)
14	Визуализация ванной Ракурс 10
15	Визуализация ванной Ракурс 11
16	Визуализация детской Ракурс 12
17	Визуализация детской Ракурс 13
18	Визуализация кабинета Ракурс 14, вид сверху (стены срезаны)
19	Визуализация кабинета Ракурс 15
20	Визуализация гардеробной Ракурс 16, вид сверху (стены срезаны)
21	Визуализация спальни Ракурс 17
22	Визуализация спальни Ракурс 18
23	Визуализация спальни Ракурс 19, вечернее освещение
24	Варианты отделки «Светлая» · «Графит» · «Тёплая»
25	Общий вид квартиры Отделка «Графит» и «Тёплая»
26	План обмера помещения
27	План демонтажа

Лист	Наименование
28	План монтажа перегородок
29	Строительный план с экспликацией помещений
30	План расположения мебели и оборудования
31	План пола спецификация напольных покрытий
32	План плинтусов
33	План потолка и освещения
34	План привязки выключателей к группам освещения
35	План размещения розеток и электровыводов
36	План тёплого пола
37	План кондиционирования и вентиляции
38	План дверей спецификация дверных блоков
39	План сантехнического оборудования и спецификация
40	Развёртки стен кухни-гостиной
41	Развёртки стен прихожей
42	Развёртки стен холла
43	Развёртки стен гостевого санузла
44	Развёртки стен ванной
45	Развёртки стен детской
46	Развёртки стен кабинета
47	Развёртки стен гардеробной
48	Развёртки стен спальни
49	Ведомость отделки помещений
50	Чертежи мебели кухонный гарнитур
51	Чертежи мебели прихожая и гостиная
52	Чертежи мебели детская и кабинет
53	Чертежи мебели гардеробная и спальня
54	Чертежи мебели санузлы

						Дизайн-проект квартиры 20, 6 этаж г. Салехард · планировочное решение №148, вариант 1	№ ДП	Лист	Листов
Изм.	Уч-к	К-во	№ Док.	Подпись	Дата		ДП-20	02	54
Дизайнер						Содержание	**КВ 20** 3D-модель · альбом		
Рук. проекта									
Заказчик									

Пояснительная записка к дизайн-проекту

1. Альбом выполнен на основании планировочного решения №148 (вариант 1) и плана 6 этажа. Геометрия снята с векторного чертежа: внутренний контур 13,0 × 6,0 м, стена к лестничной клетке 250 мм, наружные стены 500 мм, перегородки 110–140 мм.

2. За отметку 0,000 принята отметка чистого пола квартиры. Высота помещений принята 2,75 м и подлежит уточнению по факту.

3. Все размеры указаны в миллиметрах от чистовых поверхностей и проверяются по месту до заказа материалов и мебели.

4. Планировка — по планировочному решению застройщика №148 с одним изменением: кабинет и гардеробная сдвинуты на 300 мм к гостиной, за счёт чего спальня родителей расширена с 3,21 до 3,51 м (кровать 1800). Перегородки возводятся заново по плану монтажа; несущие конструкции не затрагиваются.

5. В процессе ремонта возможна корректировка отдельных размеров (площадь помещений, привязки) по результатам контрольного обмера.

6. Перед устройством потолков уточнить фактическую высоту и трассы инженерных сетей; отступ подвесных участков — по плану потолков.

7. Привязки выводов воды и канализации, сечения труб и высоту установки сантехнических приборов уточнить по техническим картам выбранных приборов.

8. Розетки и выключатели устанавливать после штукатурных работ; высоты — по плану розеток. Группы освещения — по плану выключателей.

9. Заказ дверей производить после завершения штукатурных работ и снятия финальных замеров проёмов.

10. Встроенную мебель (кухня, шкафы, гардеробная) заказывать по чертежам раздела «Чертежи мебели» после контрольного замера изготовителем.

11. Образцы отделочных материалов согласовать с заказчиком до закупки; оттенки краски — по выкрасам на месте.

12. Визуализации выполнены по 3D-модели квартиры и передают планировку, габариты и цветовое решение. Они не являются фотореалистичными изображениями и не заменяют чертежи.


13. Отделка предложена в трёх вариантах: «Светлая» (основной, по дизайн-проекту), «Графит» и «Тёплая». Ведомости материалов даны для основного варианта.

14. Размещение внутренних и наружных блоков кондиционирования согласовать с управляющей компанией и монтажной организацией.

15. Кондиционирование, тёплые полы, подсветка — опции; их объём уточняется при составлении сметы.


16. Работы вести в соответствии с действующими нормами и правилами РФ; перепланировка, затрагивающая мокрые зоны, подлежит согласованию в установленном порядке.


						Дизайн-проект квартиры 20, 6 этаж г. Салехард · планировочное решение №148, вариант 1	№ ДП	Лист	Листов
Изм.	Уч-к	К-во	№ Док.	Подпись	Дата		ДП-20	03	54
Дизайнер						Пояснительная записка	**КВ 20** 3D-модель · альбом		
Рук. проекта									
Заказчик									

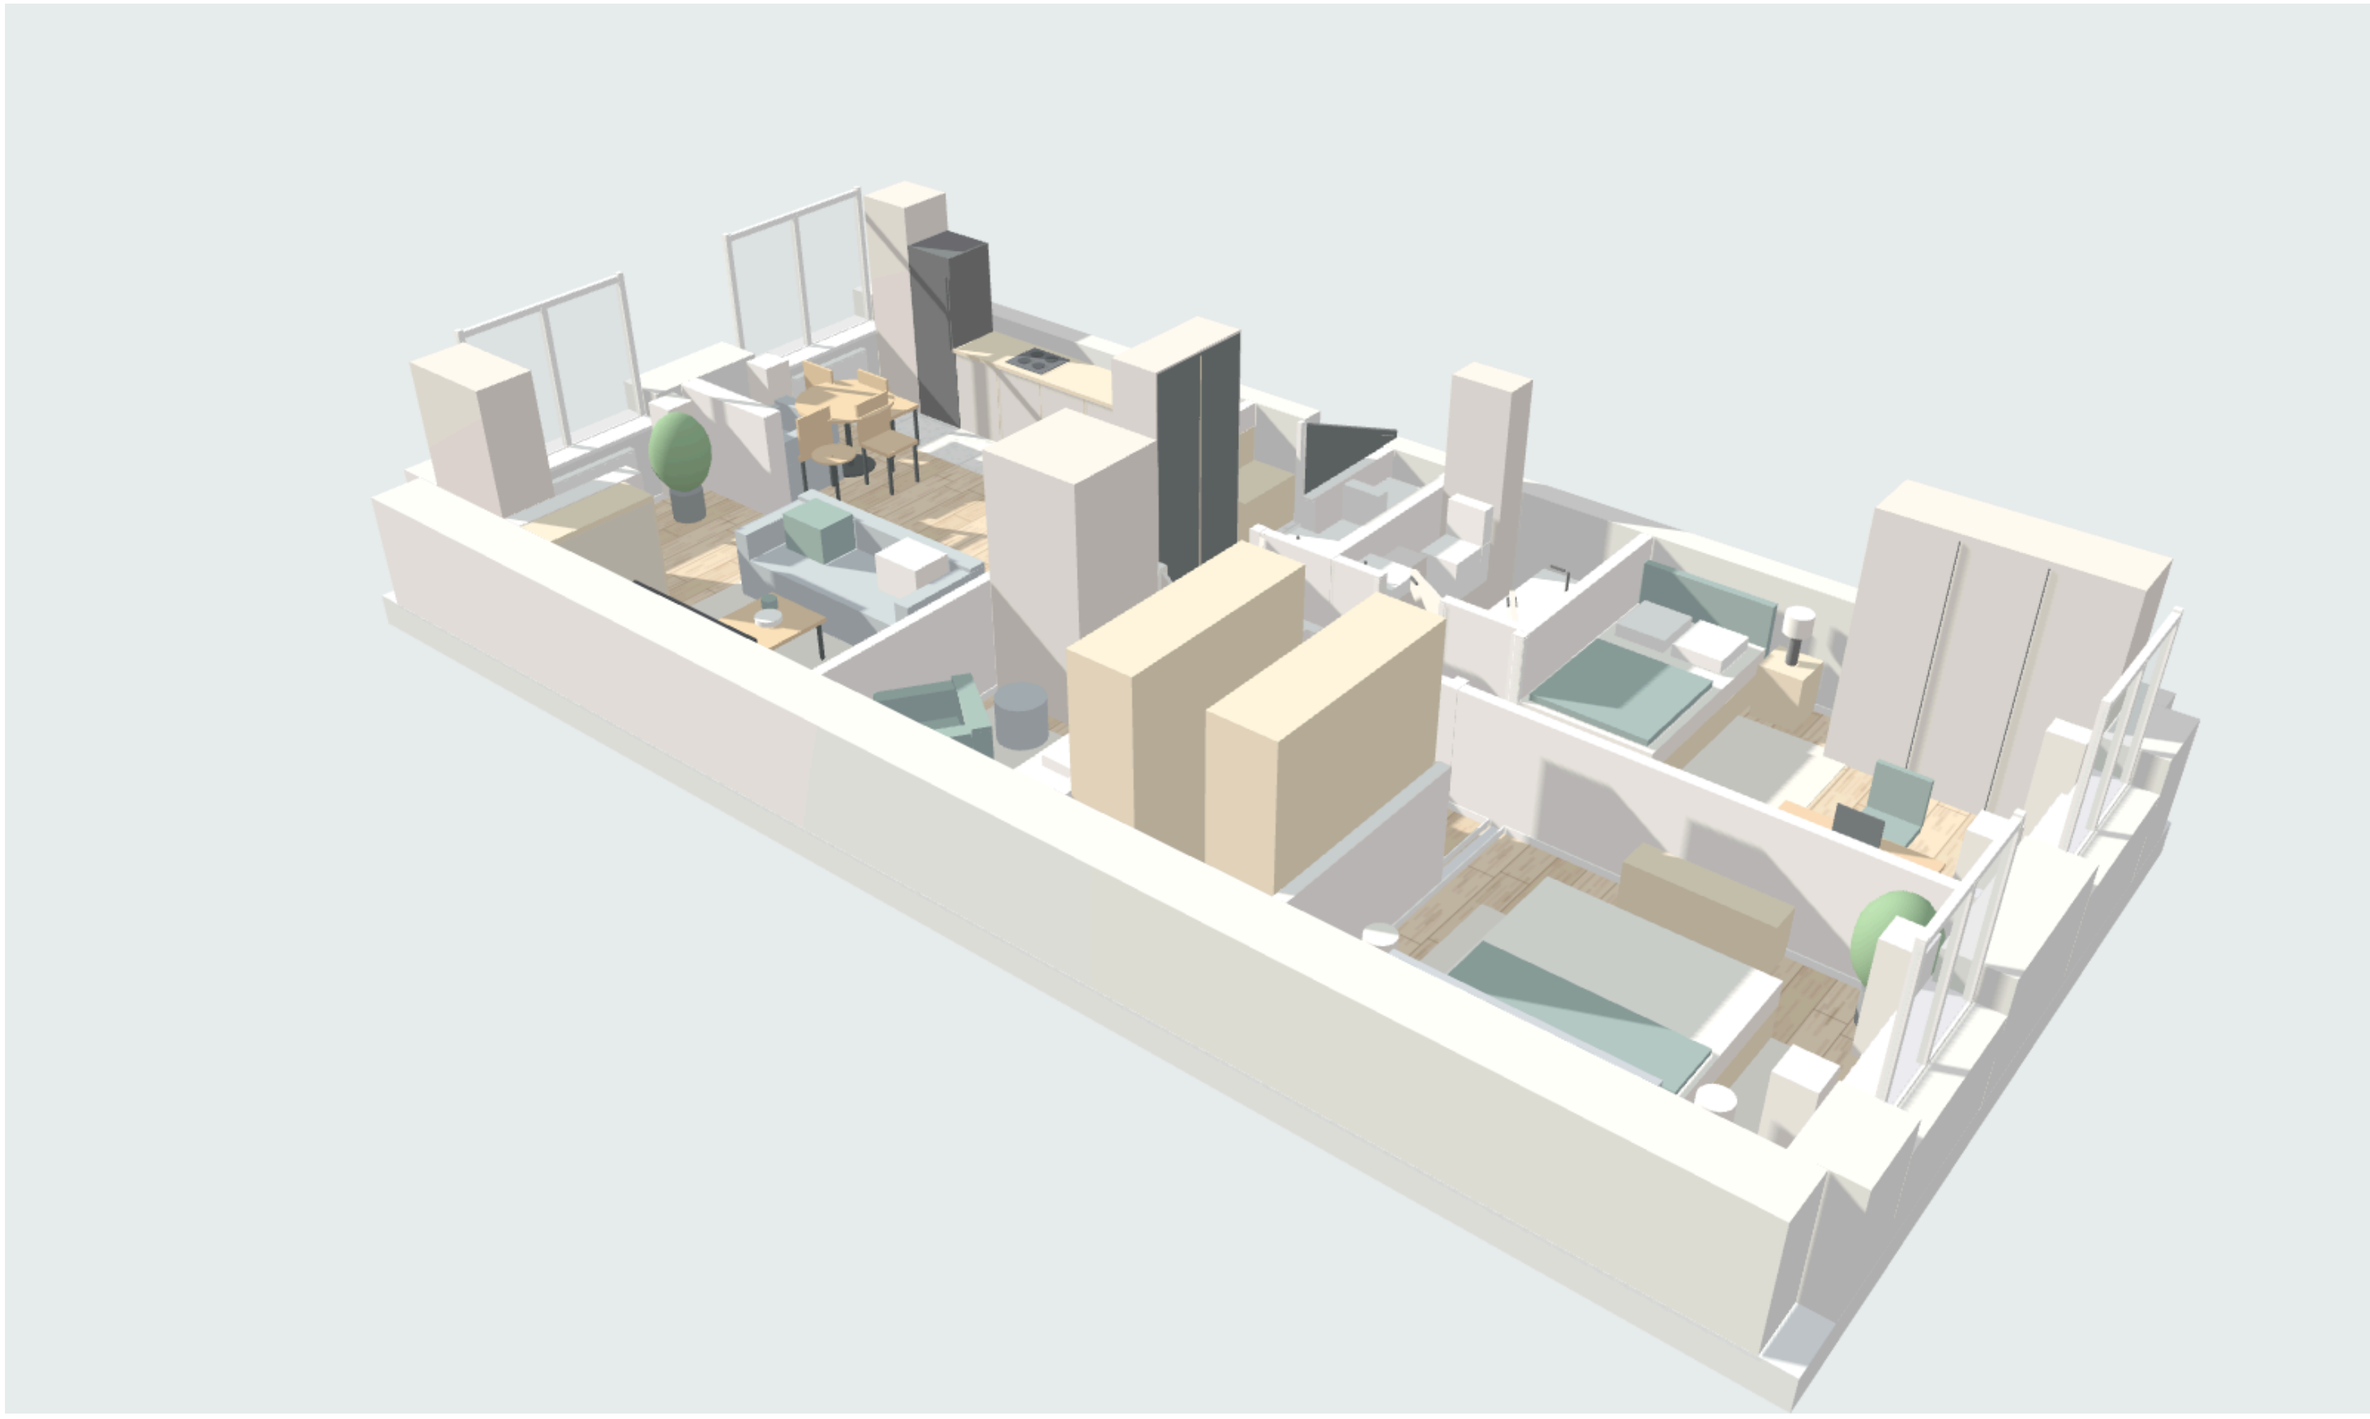


Общий вид квартиры со срезанными стенами. Основной вариант отделки: стены greige, светлый дуб, светлый камень, графитовые акценты.


						Дизайн-проект квартиры 20, 6 этаж г. Салехард · планировочное решение №148, вариант 1	№ ДП	Лист	Листов
Изм.	Уч-к	К-во	№ Док.	Подпись	Дата		**ДП-20**	**04**	**54**
Дизайнер						Общий вид квартиры Отделка «Светлая» (основная)	**КВ 20** 3D-модель · альбом		
Рук. проекта									
Заказчик									

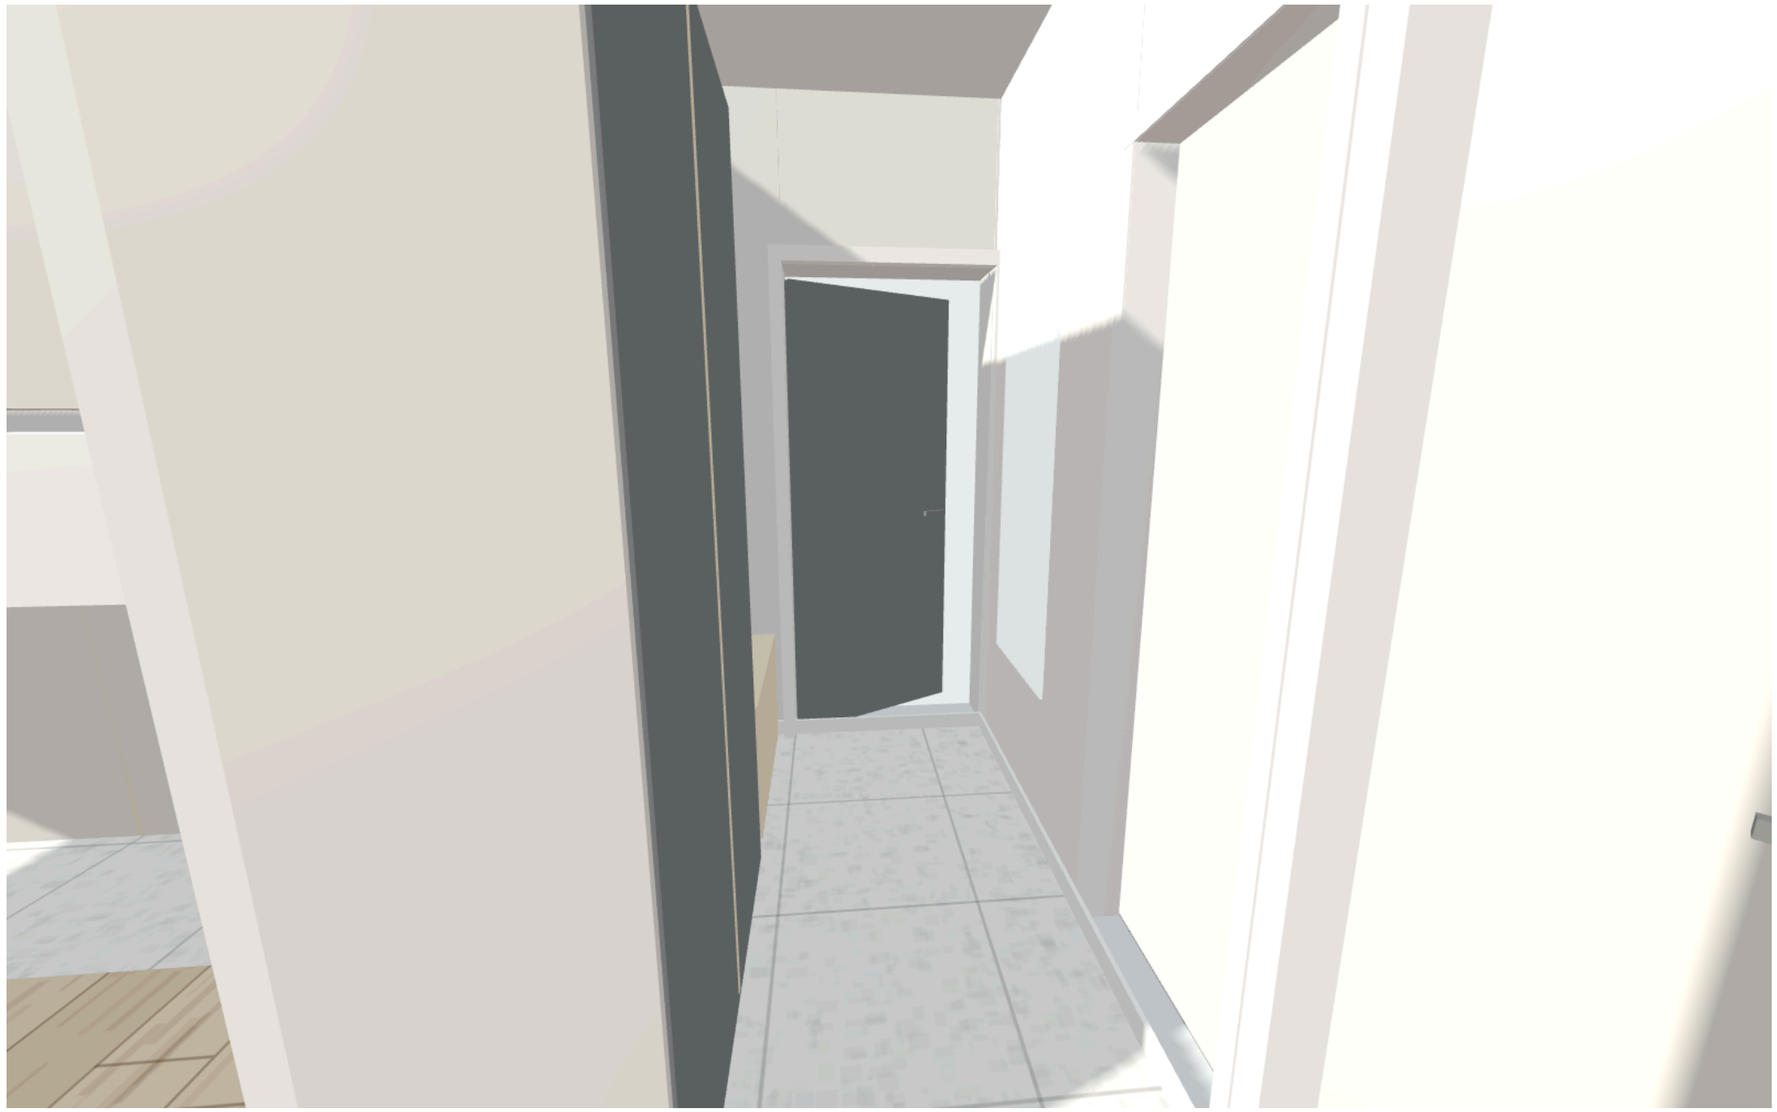

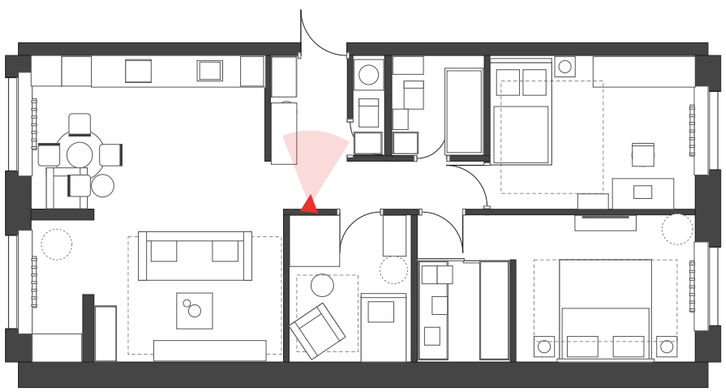


						Дизайн-проект квартиры 20, 6 этаж г. Салехард · планировочное решение №148, вариант 1	№ ДП	Лист	Листов
Изм.	Уч-к	К-во	№ Док.	Подпись	Дата		ДП-20	05	54
Дизайнер						Визуализация прихожей Ракурс 1	**КВ 20** 3D-модель · альбом		
Рук. проекта									
Заказчик									

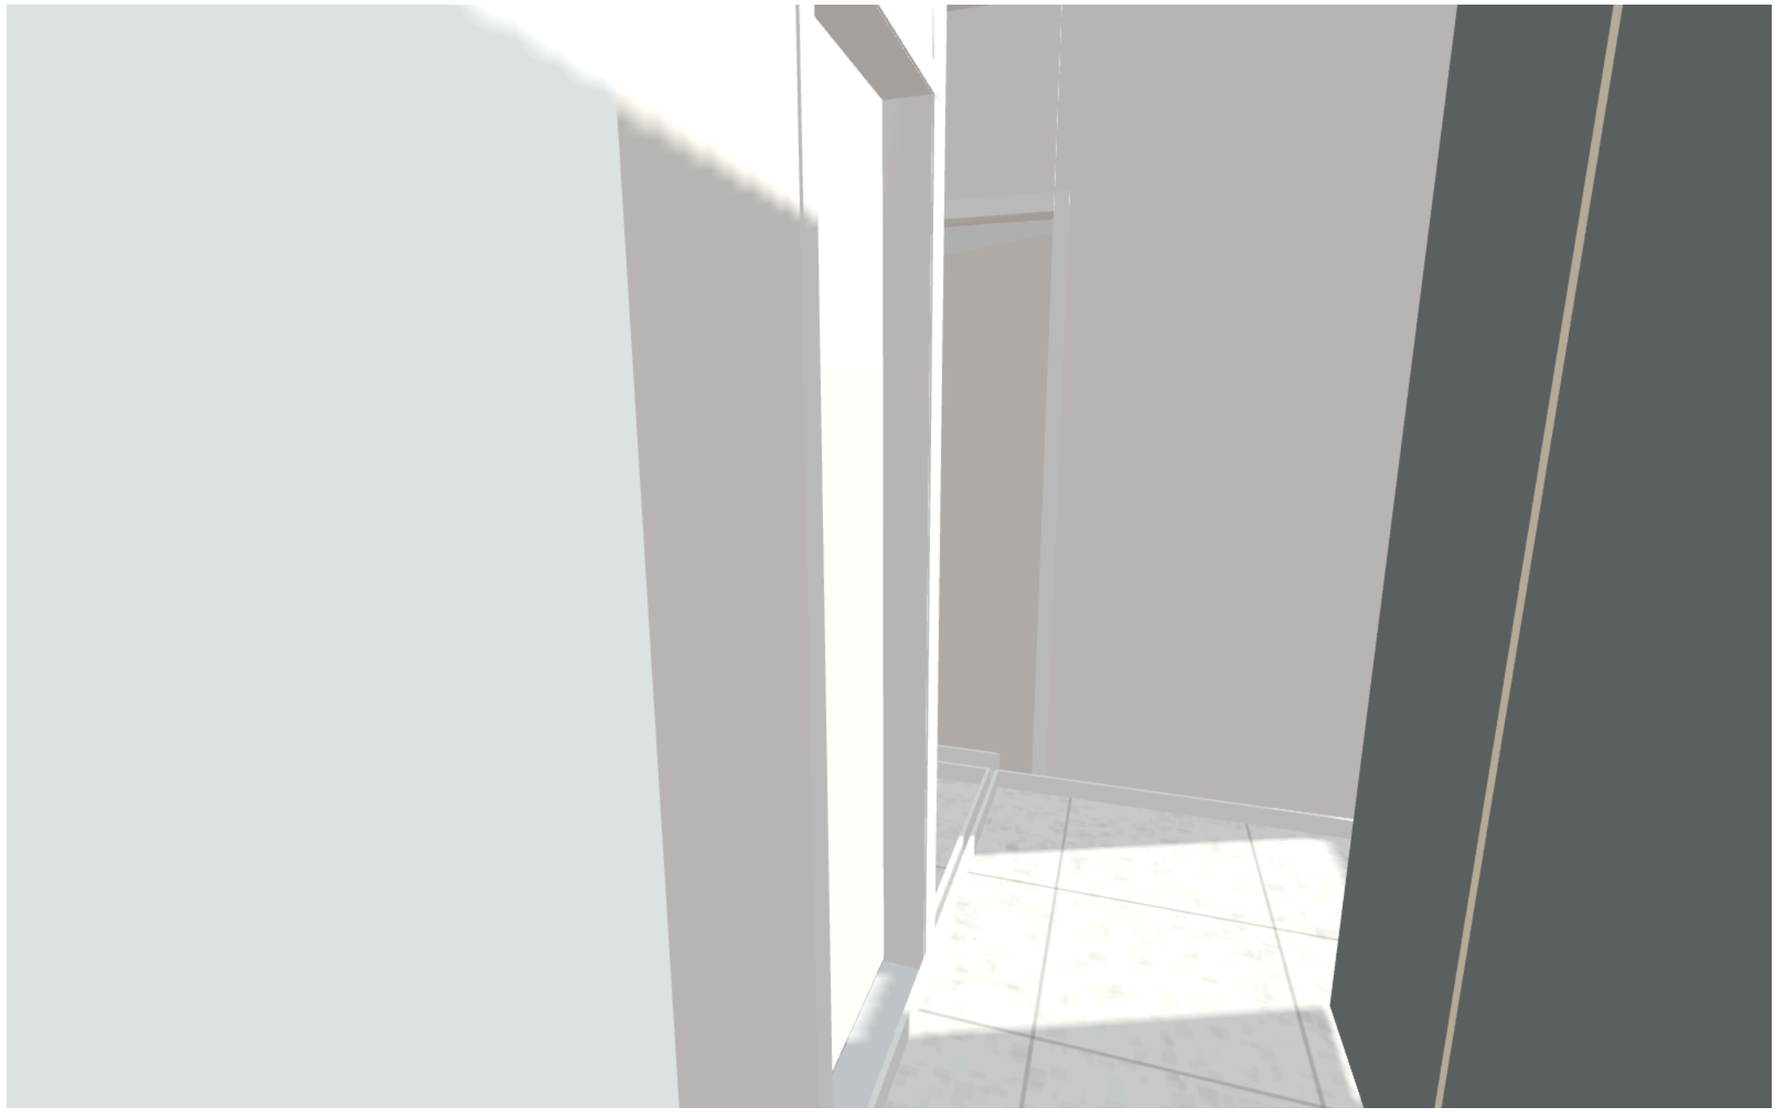

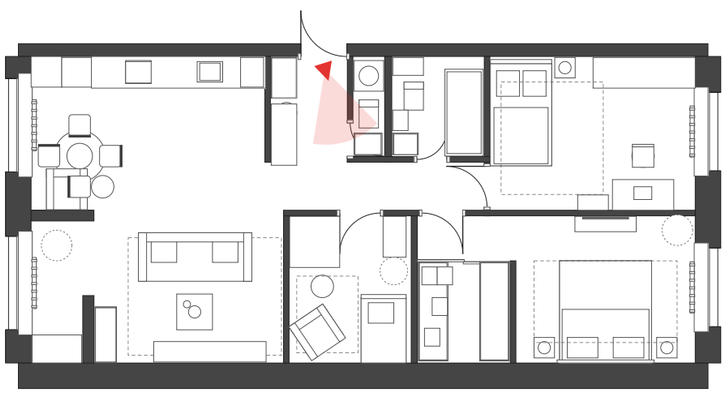

Изм.	Уч-к	К-во	№ Док.	Подпись	Дата	Дизайн-проект квартиры 20, 6 этаж г. Салехард · планировочное решение №148, вариант 1	№ ДП	Лист	Листов
							ДП-20	06	54
Дизайнер						Визуализация прихожей Ракурс 2	**КВ 20** 3D-модель · альбом		
Рук. проекта									
Заказчик									



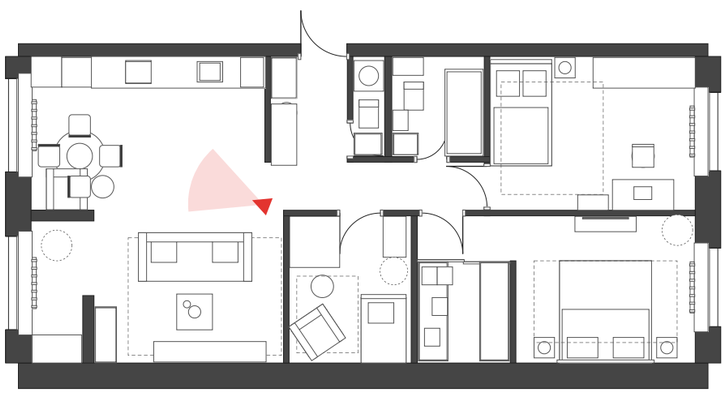


						Дизайн-проект квартиры 20, 6 этаж г. Салехард · планировочное решение №148, вариант 1	№ ДП	Лист	Листов
Изм.	Уч-к	К-во	№ Док.	Подпись	Дата		**ДП-20**	**07**	**54**
Дизайнер						Визуализация кухни-гостиной Ракурс 3	**КВ 20** 3D-модель · альбом		
Рук. проекта									
Заказчик									






						Дизайн-проект квартиры 20, 6 этаж г. Салехард · планировочное решение №148, вариант 1	№ ДП	Лист	Листов
Изм.	Уч-к	К-во	№ Док.	Подпись	Дата		ДП-20	08	54
Дизайнер						Визуализация кухни-гостиной Ракурс 4	**КВ 20** 3D-модель · альбом		
Рук. проекта									
Заказчик									

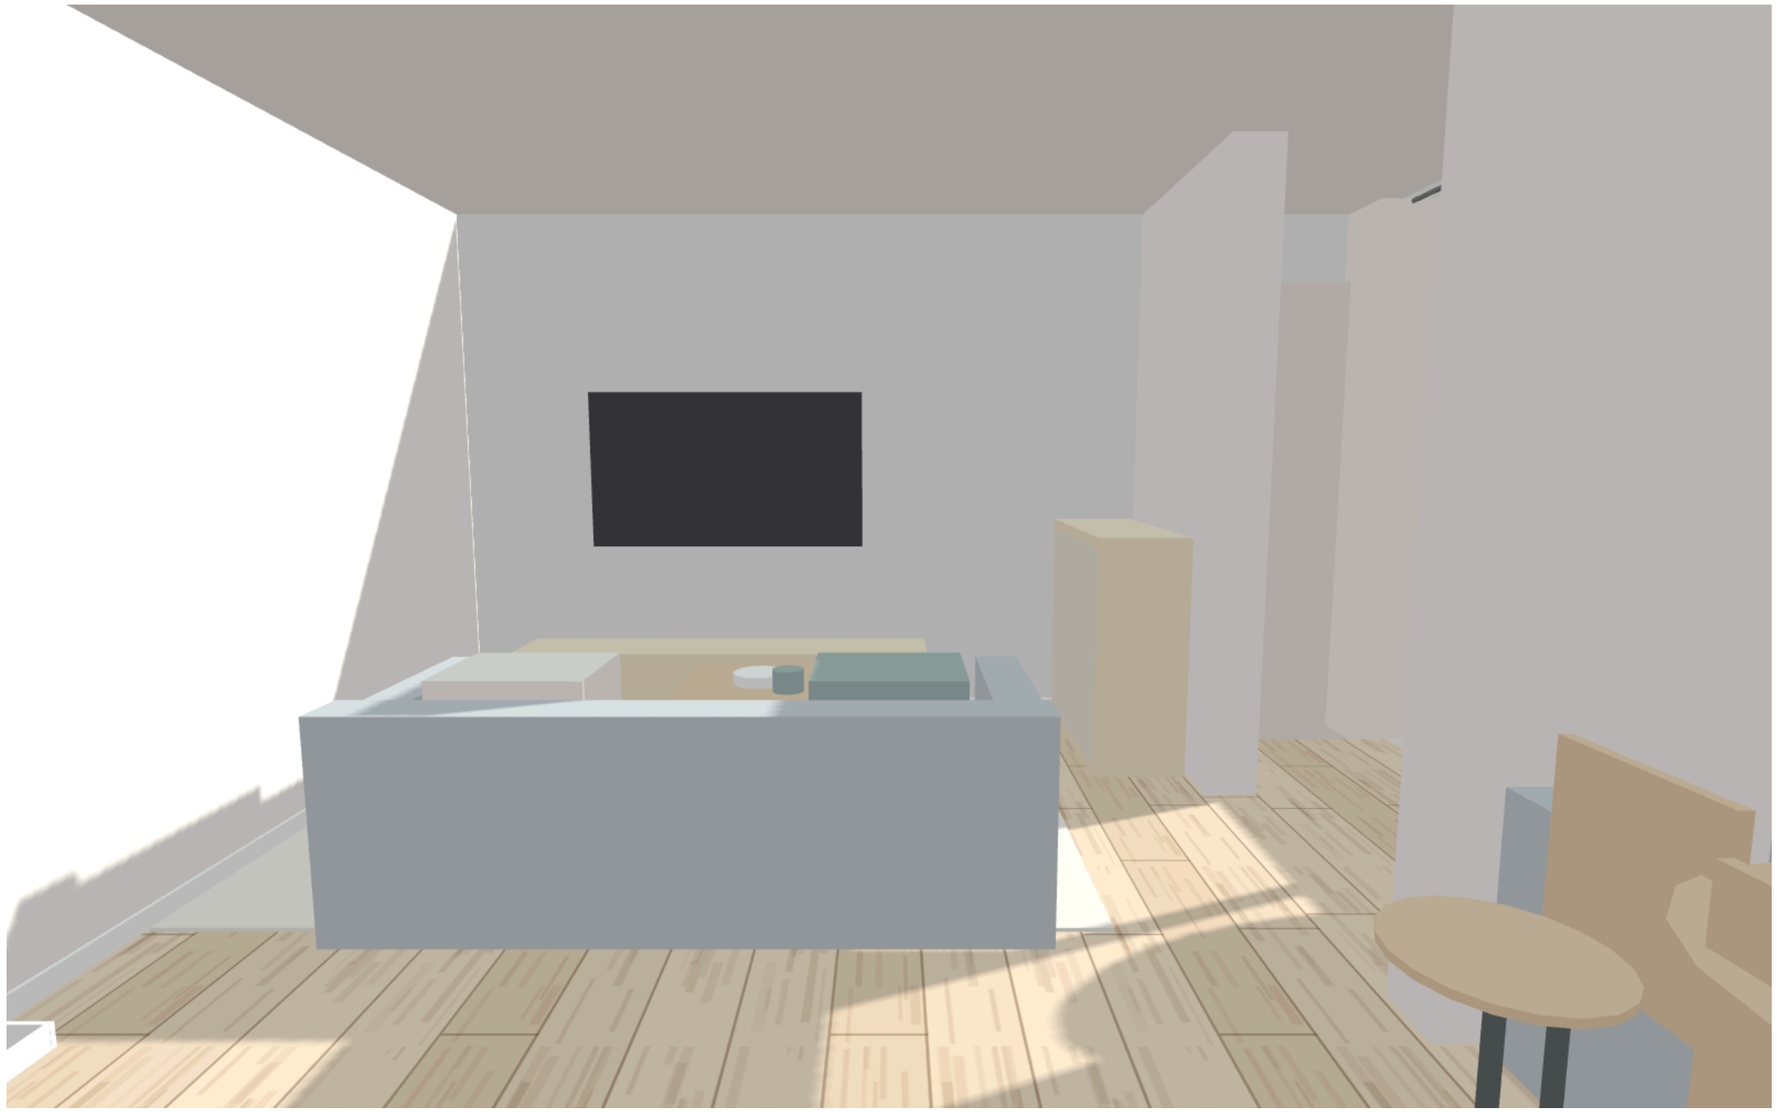





						Дизайн-проект квартиры 20, 6 этаж г. Салехард · планировочное решение №148, вариант 1	№ ДП	Лист	Листов
Изм.	Уч-к	К-во	№ Док.	Подпись	Дата		ДП-20	09	54
Дизайнер						Визуализация кухни-гостиной Ракурс 5	**КВ 20** 3D-модель · альбом		
Рук. проекта									
Заказчик									

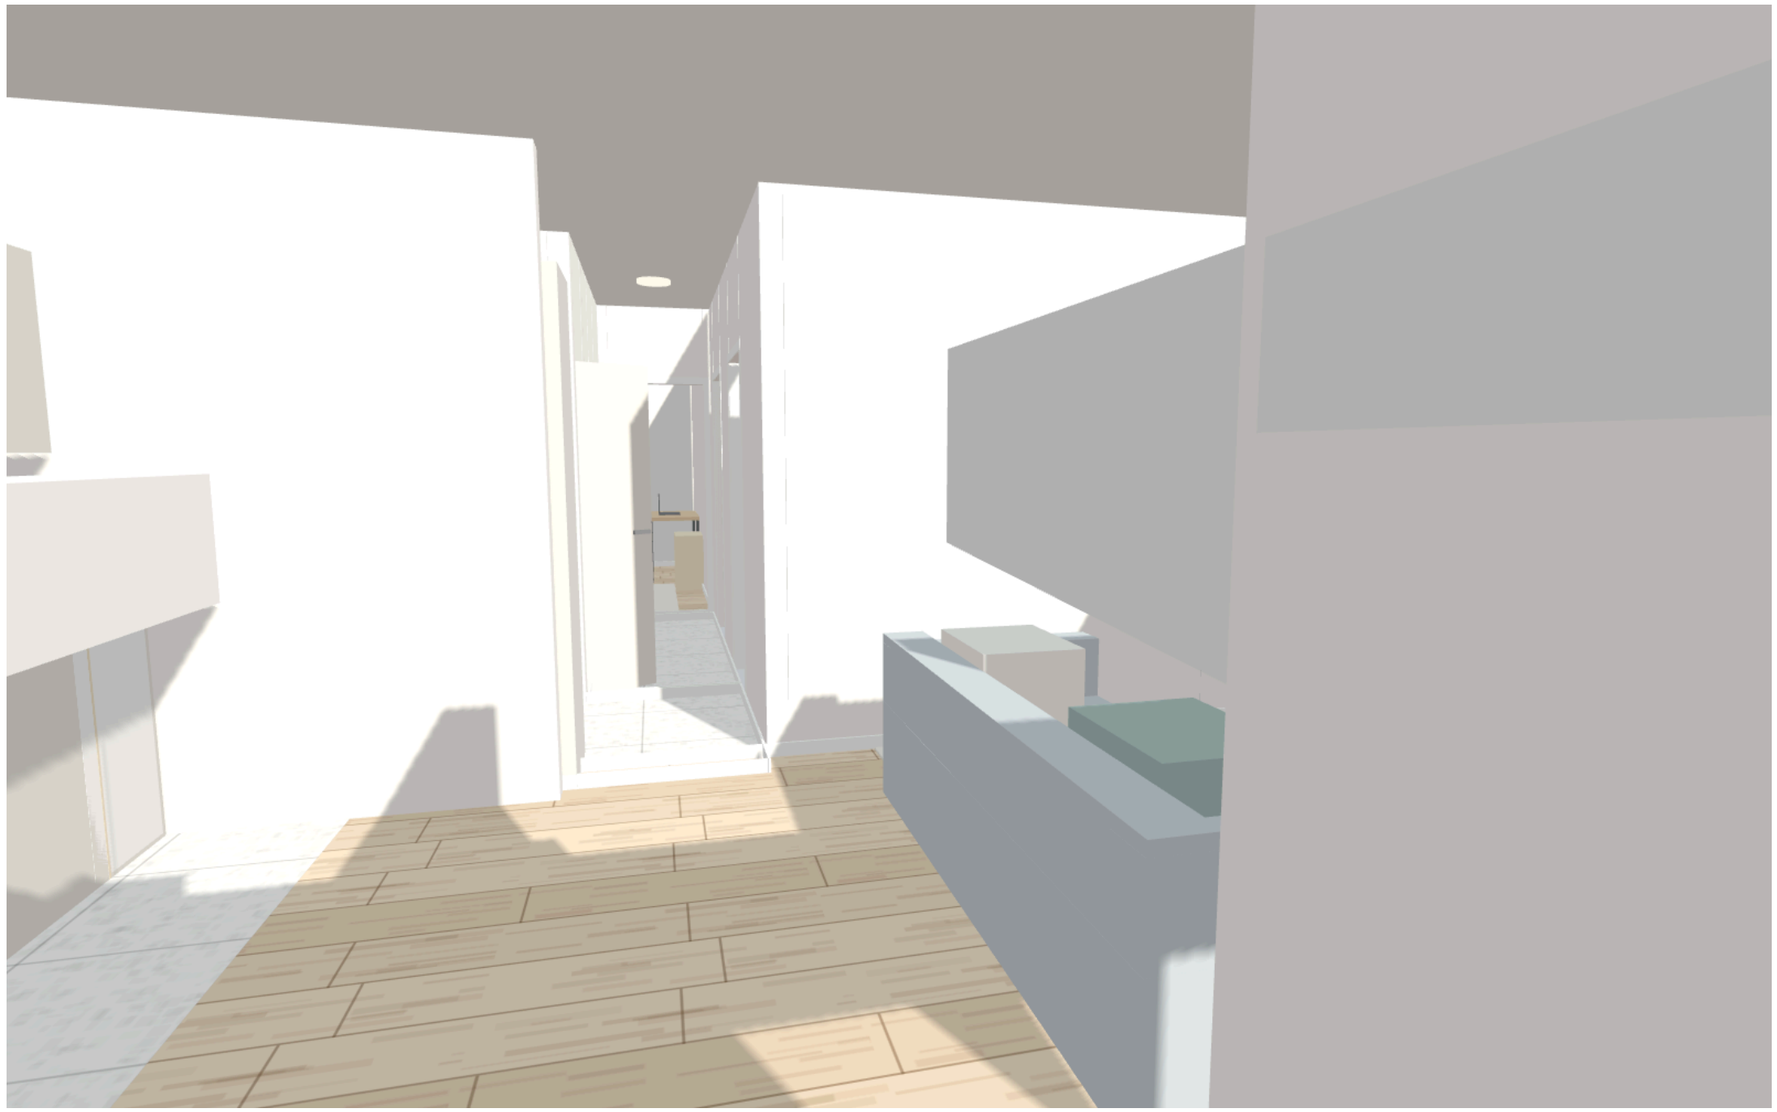



						Дизайн-проект квартиры 20, 6 этаж г. Салехард · планировочное решение №148, вариант 1	№ ДП	Лист	Листов
Изм.	Уч-к	К-во	№ Док.	Подпись	Дата		ДП-20	10	54
Дизайнер						Визуализация кухни-гостиной Ракурс 6	**КВ 20** 3D-модель · альбом		
Рук. проекта									
Заказчик									

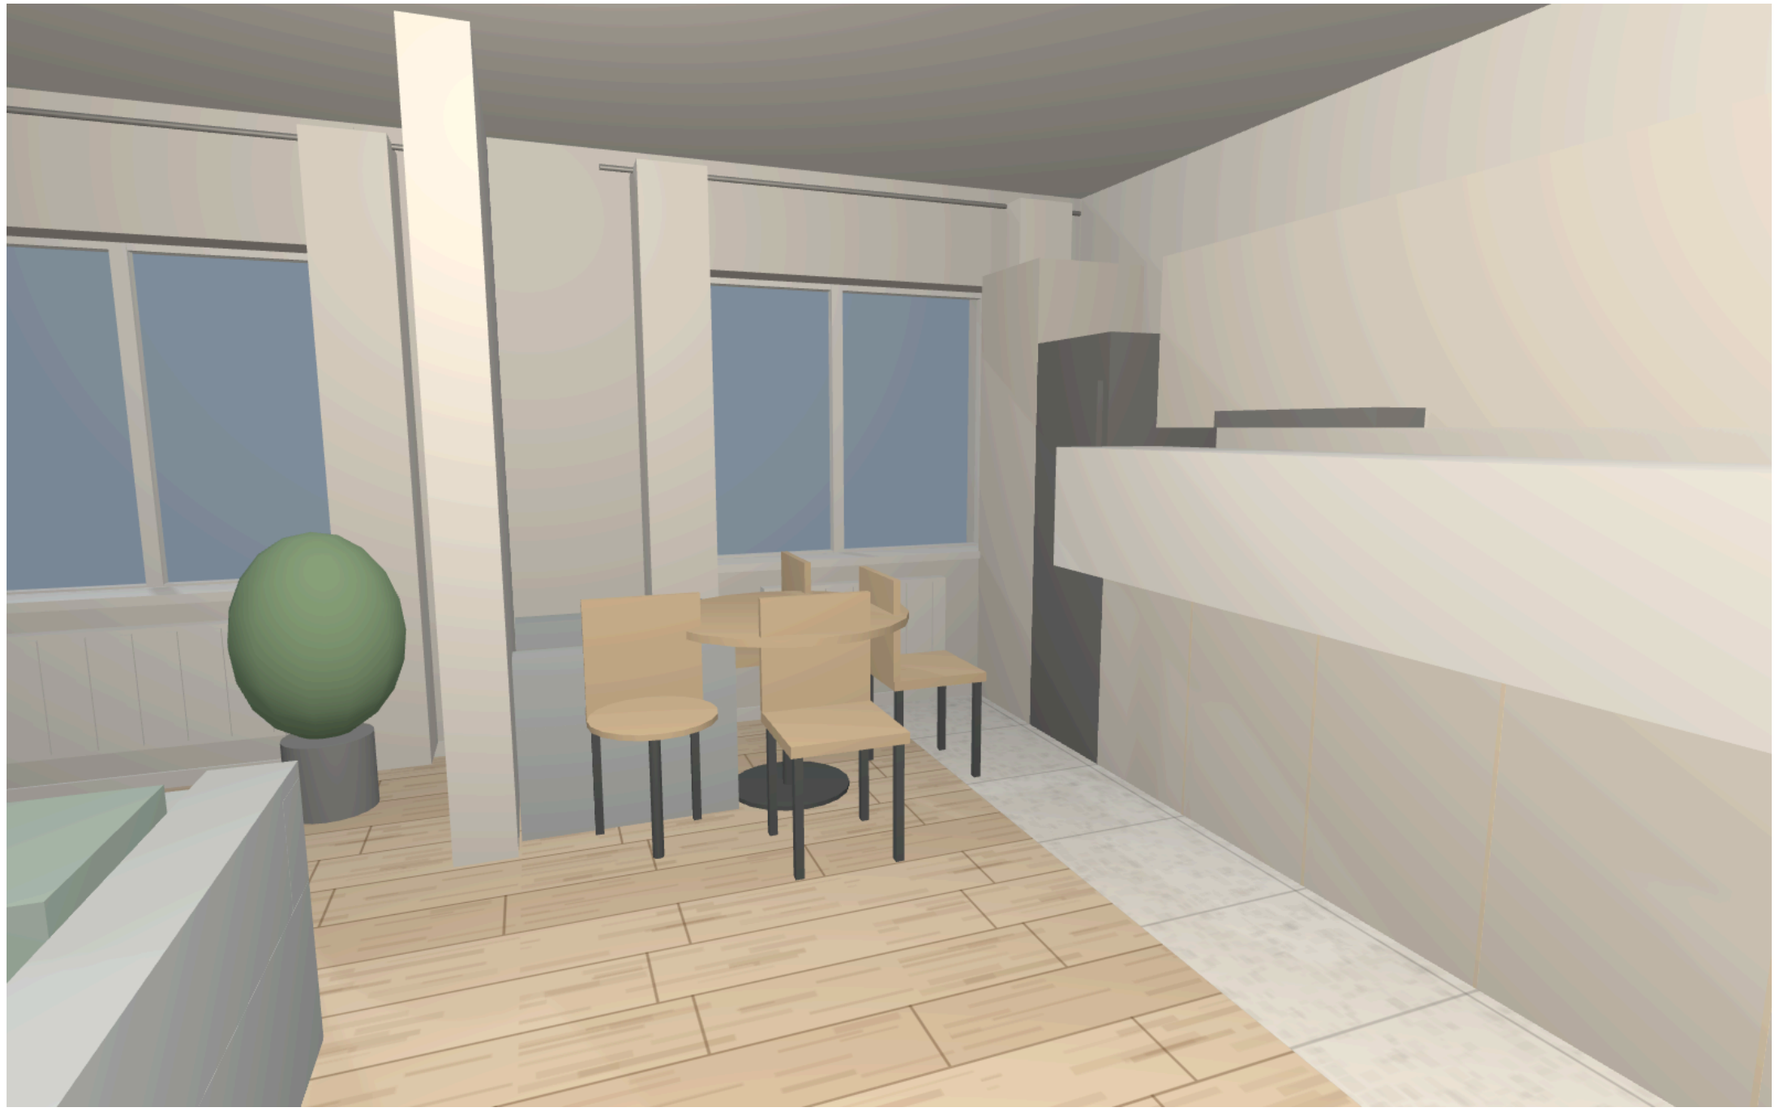

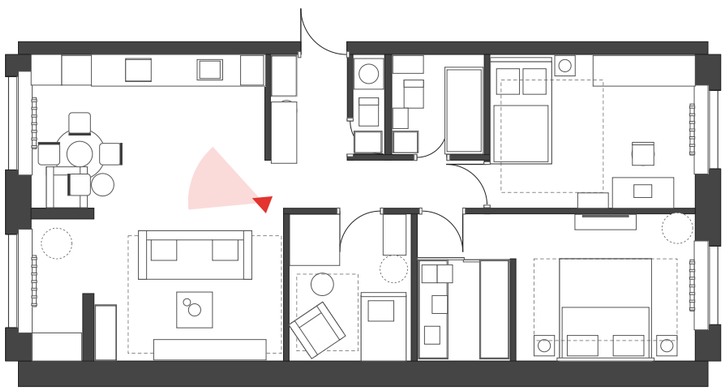



						Дизайн-проект квартиры 20, 6 этаж г. Салехард · планировочное решение №148, вариант 1	№ ДП	Лист	Листов
Изм.	Уч-к	К-во	№ Док.	Подпись	Дата		ДП-20	11	54
Дизайнер						Визуализация кухни-гостиной Ракурс 7, вечернее освещение	**КВ 20** 3D-модель · альбом		
Рук. проекта									
Заказчик									







						Дизайн-проект квартиры 20, 6 этаж г. Салехард · планировочное решение №148, вариант 1	№ ДП	Лист	Листов
Изм.	Уч-к	К-во	№ Док.	Подпись	Дата		ДП-20	12	54
Дизайнер						Визуализация холла Ракурс 8	**КВ 20** 3D-модель · альбом		
Рук. проекта									
Заказчик									

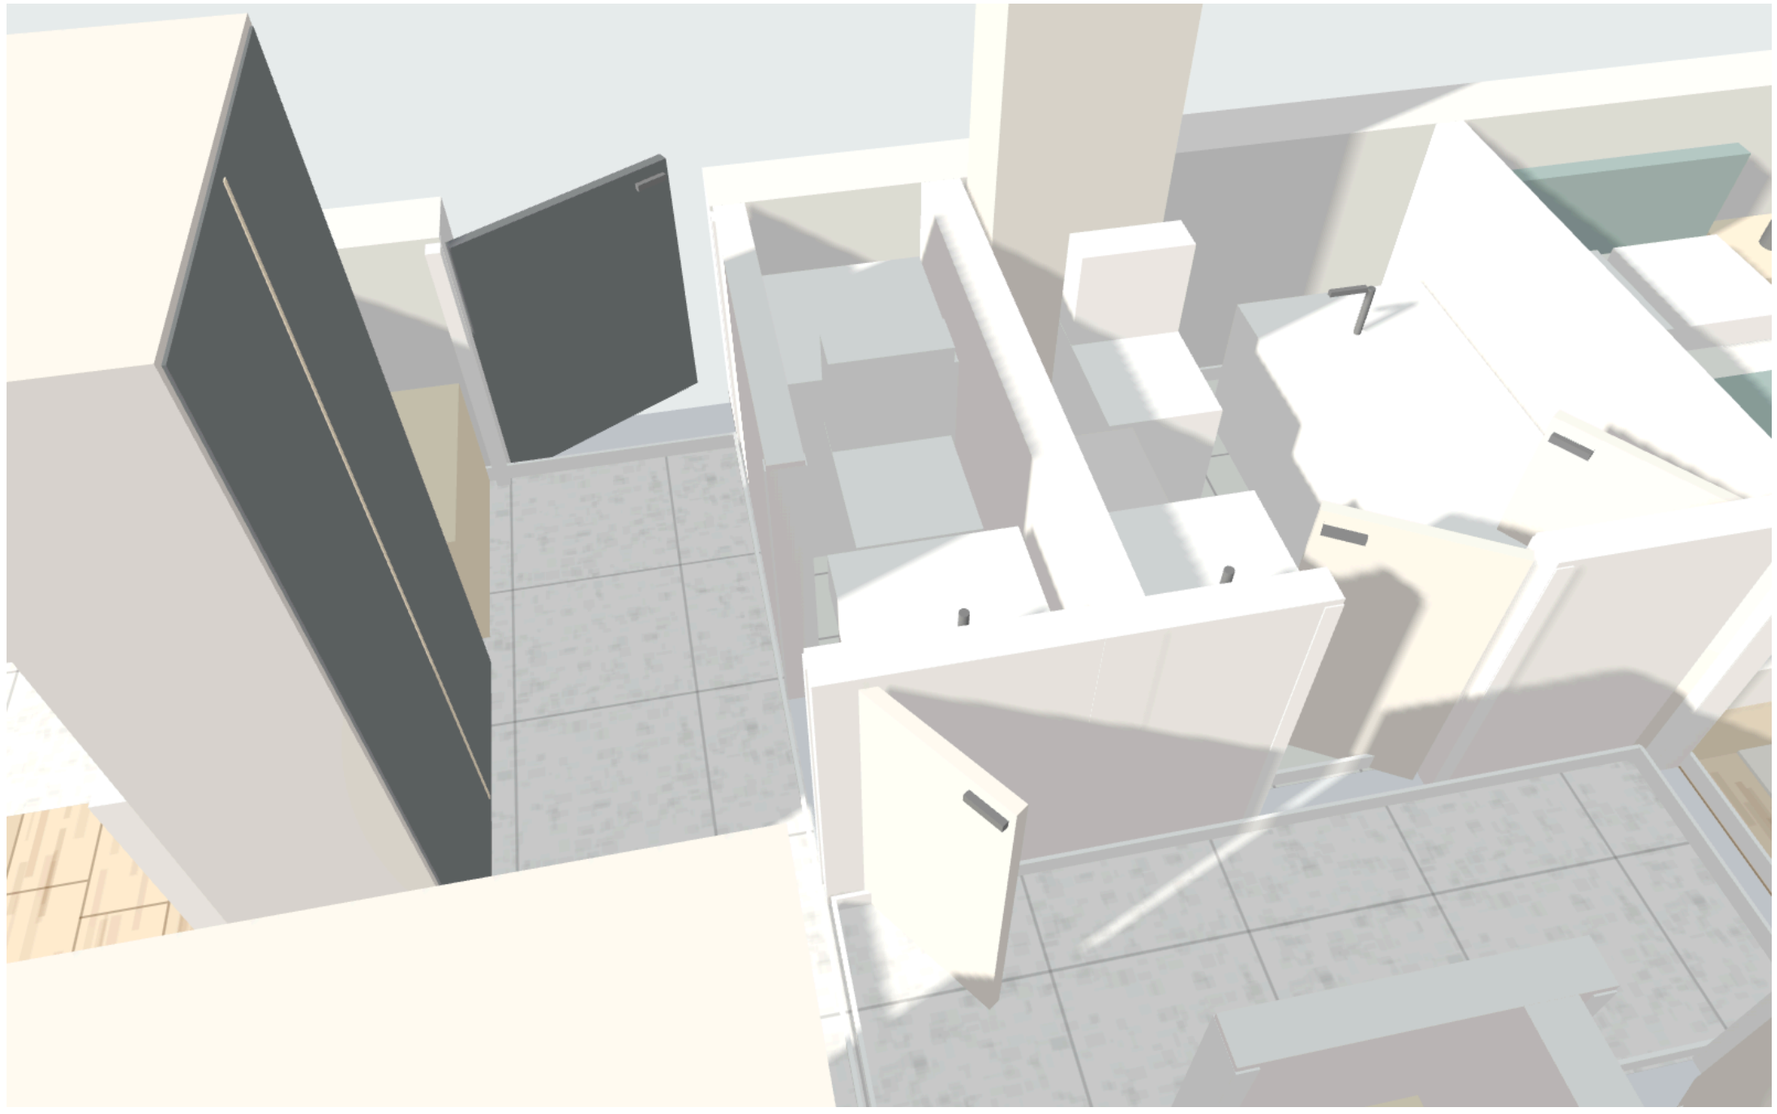

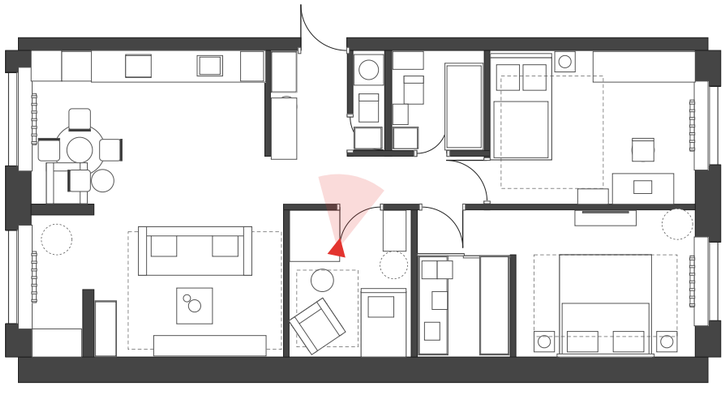


						Дизайн-проект квартиры 20, 6 этаж г. Салехард · планировочное решение №148, вариант 1	№ ДП	Лист	Листов
Изм.	Уч-к	К-во	№ Док.	Подпись	Дата		ДП-20	13	54
Дизайнер						Визуализация гостевого санузла Ракурс 9, вид сверху (стены срезаны)	**КВ 20** 3D-модель · альбом		
Рук. проекта									
Заказчик									

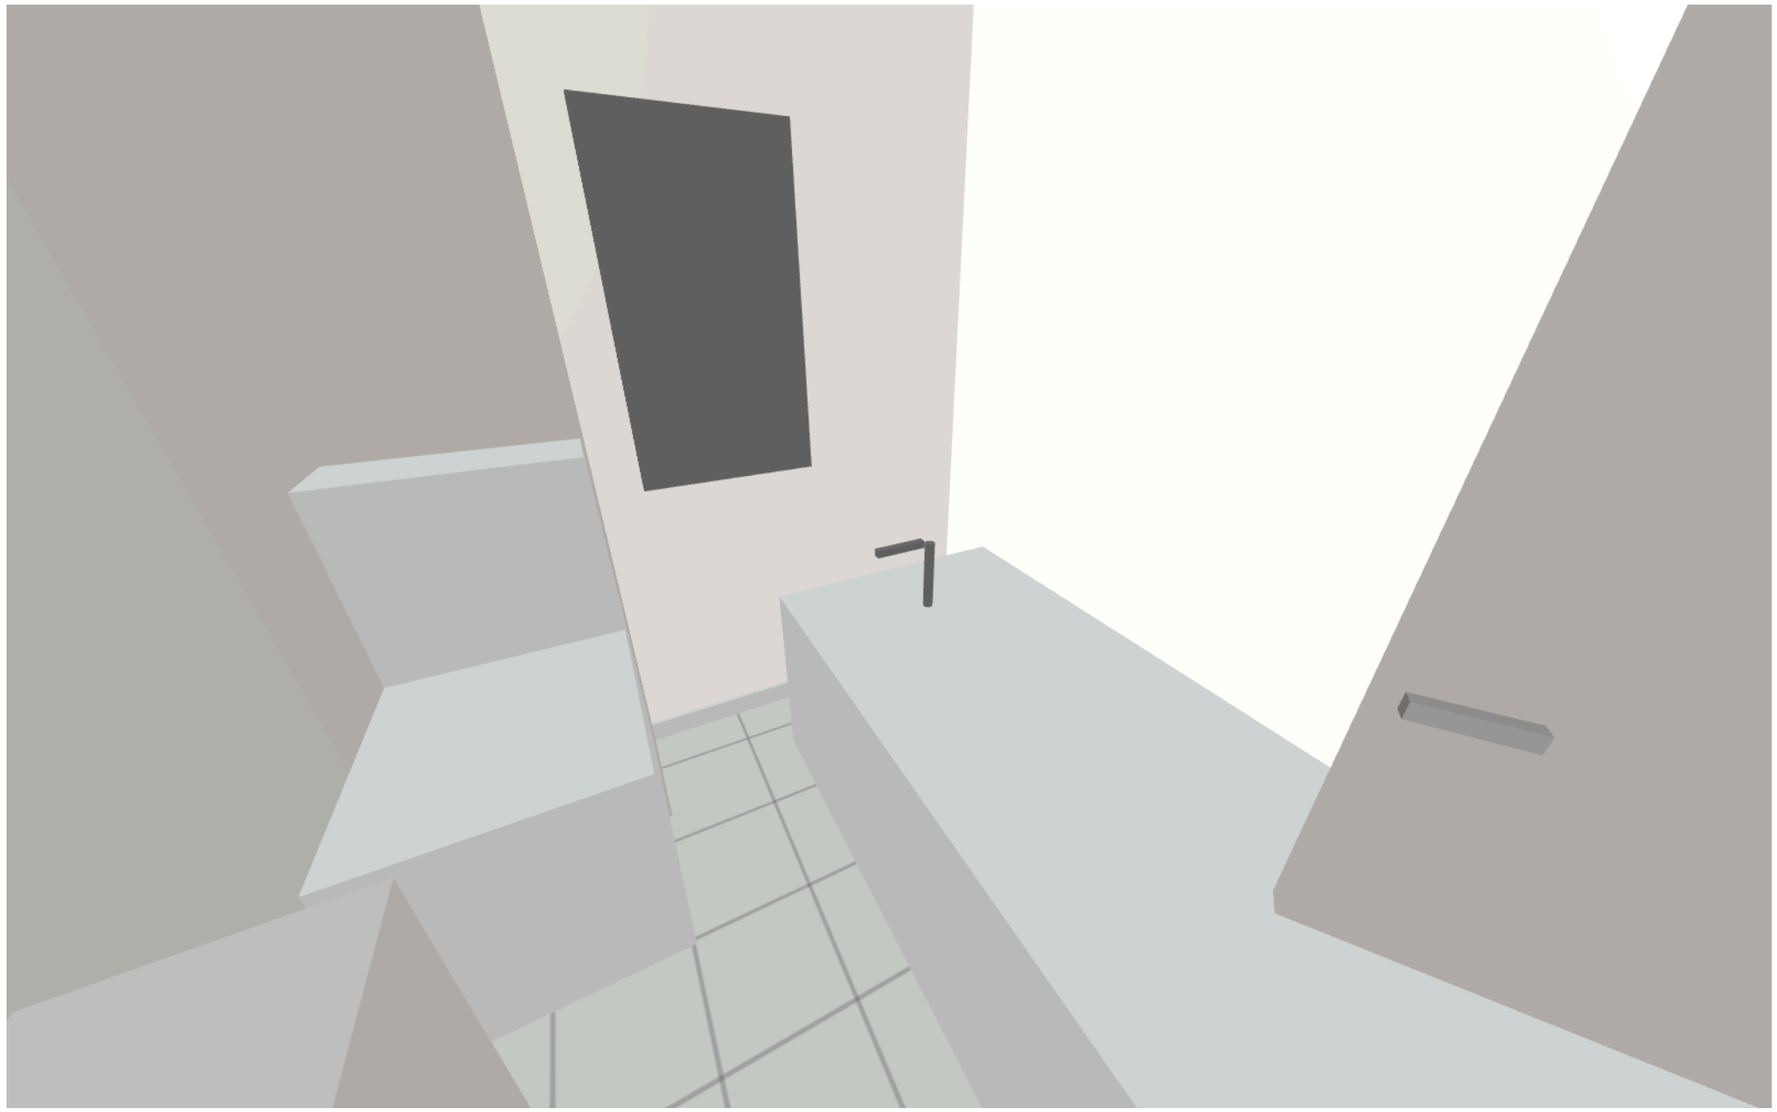

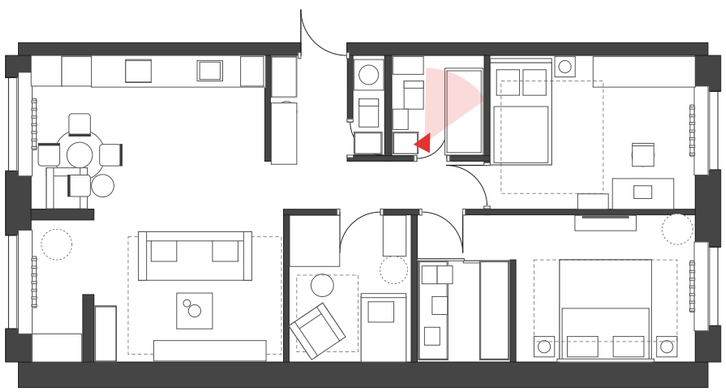



						Дизайн-проект квартиры 20, 6 этаж г. Салехард · планировочное решение №148, вариант 1	№ ДП	Лист	Листов
Изм.	Уч-к	К-во	№ Док.	Подпись	Дата		ДП-20	14	54
Дизайнер						Визуализация ванной Ракурс 10	**КВ 20** 3D-модель · альбом		
Рук. проекта									
Заказчик									

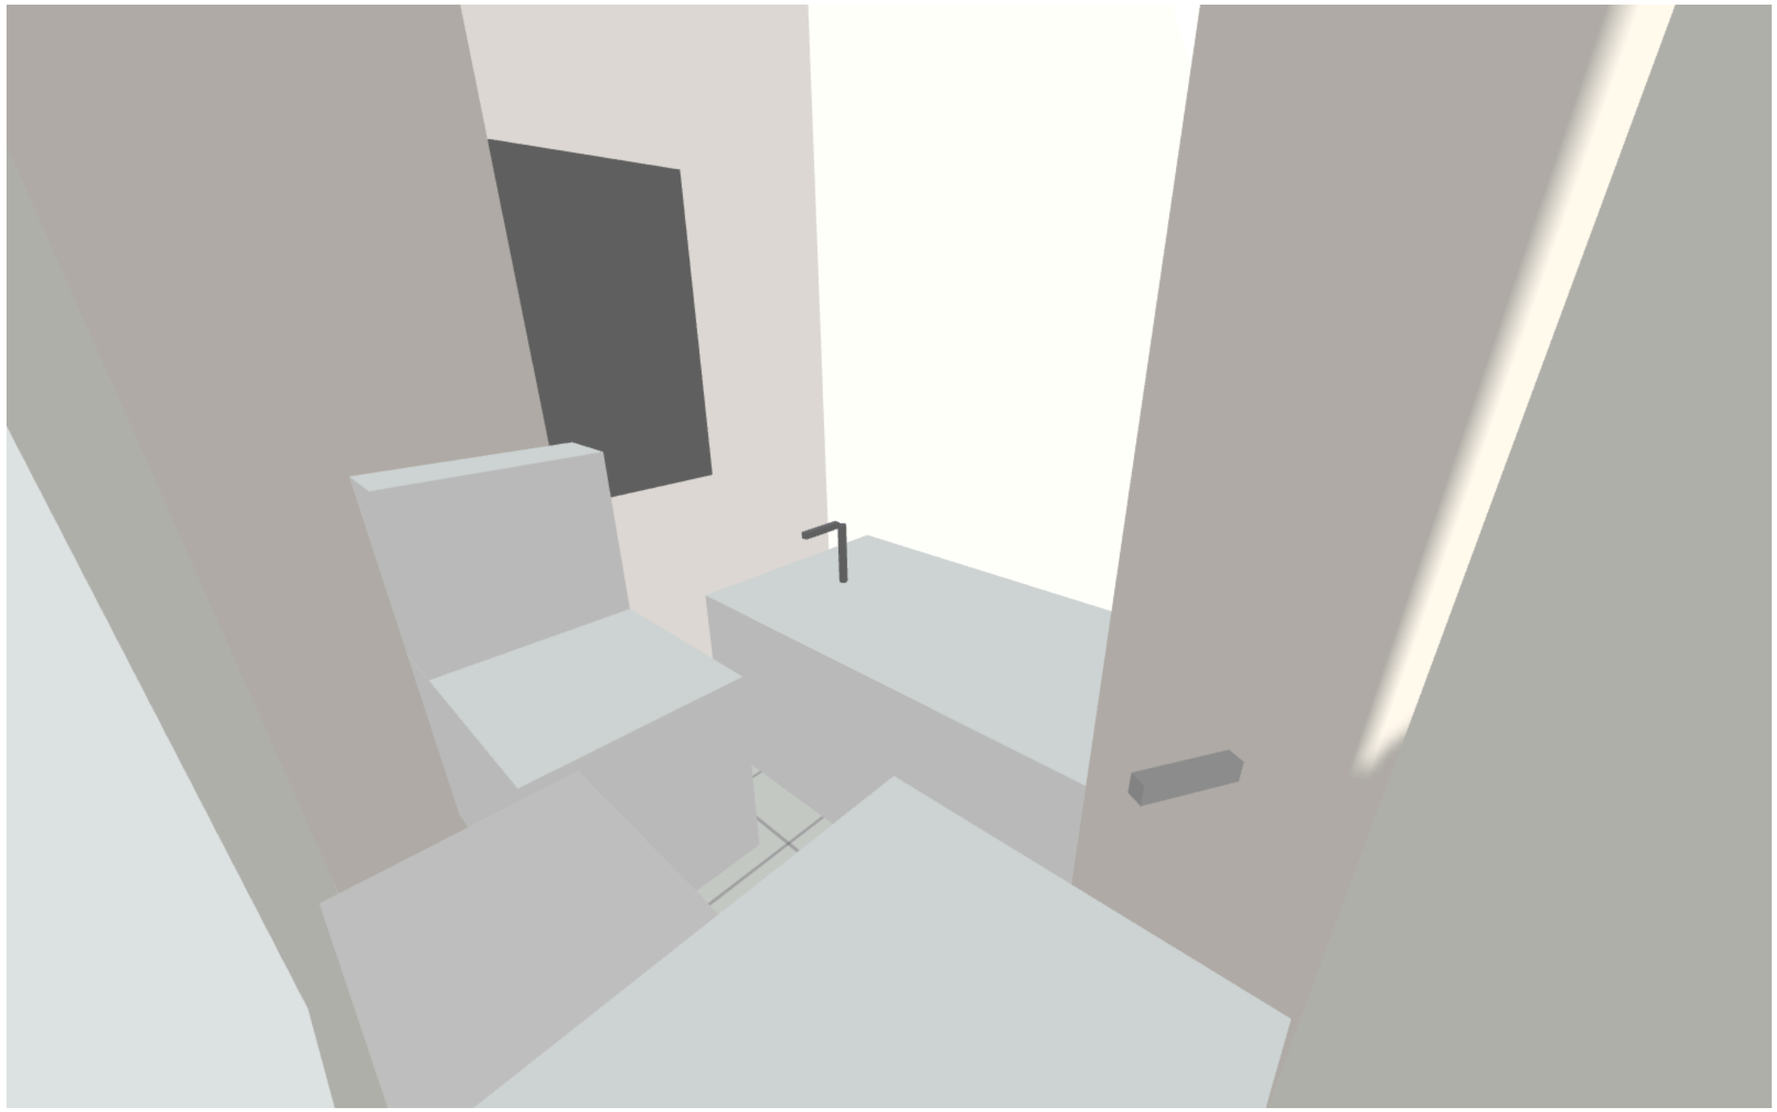




Изм.	Уч-к	К-во	№ Док.	Подпись	Дата	Дизайн-проект квартиры 20, 6 этаж г. Салехард · планировочное решение №148, вариант 1	№ ДП	Лист	Листов
							ДП-20	**15**	**54**
Дизайнер						Визуализация ванной Ракурс 11	**КВ 20** 3D-модель · альбом		
Рук. проекта									
Заказчик									

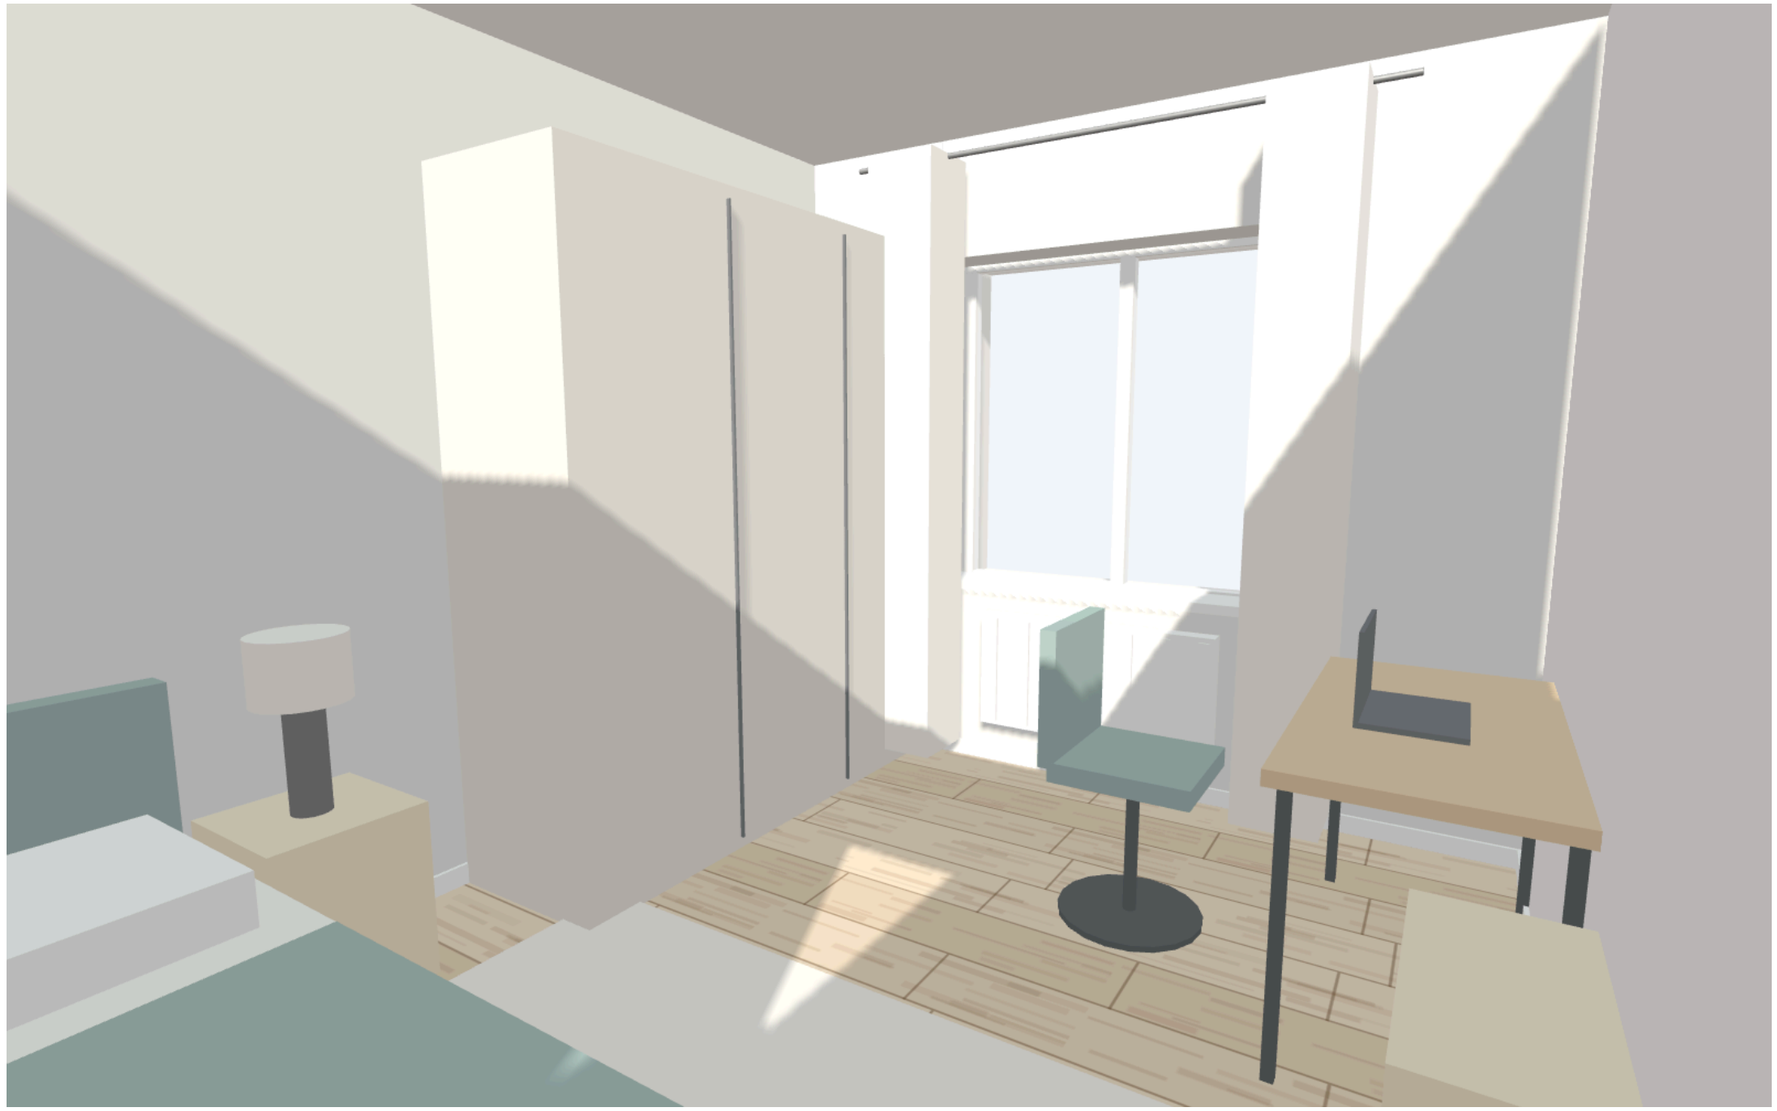

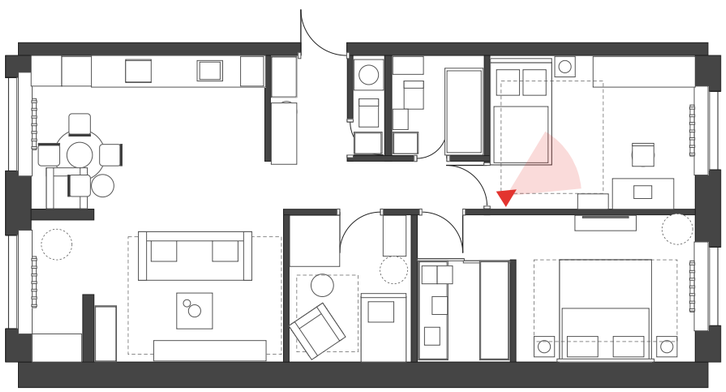



						Дизайн-проект квартиры 20, 6 этаж г. Салехард · планировочное решение №148, вариант 1	№ ДП	Лист	Листов
Изм.	Уч-к	К-во	№ Док.	Подпись	Дата		ДП-20	16	54
Дизайнер						Визуализация детской Ракурс 12	**КВ 20** 3D-модель · альбом		
Рук. проекта									
Заказчик									

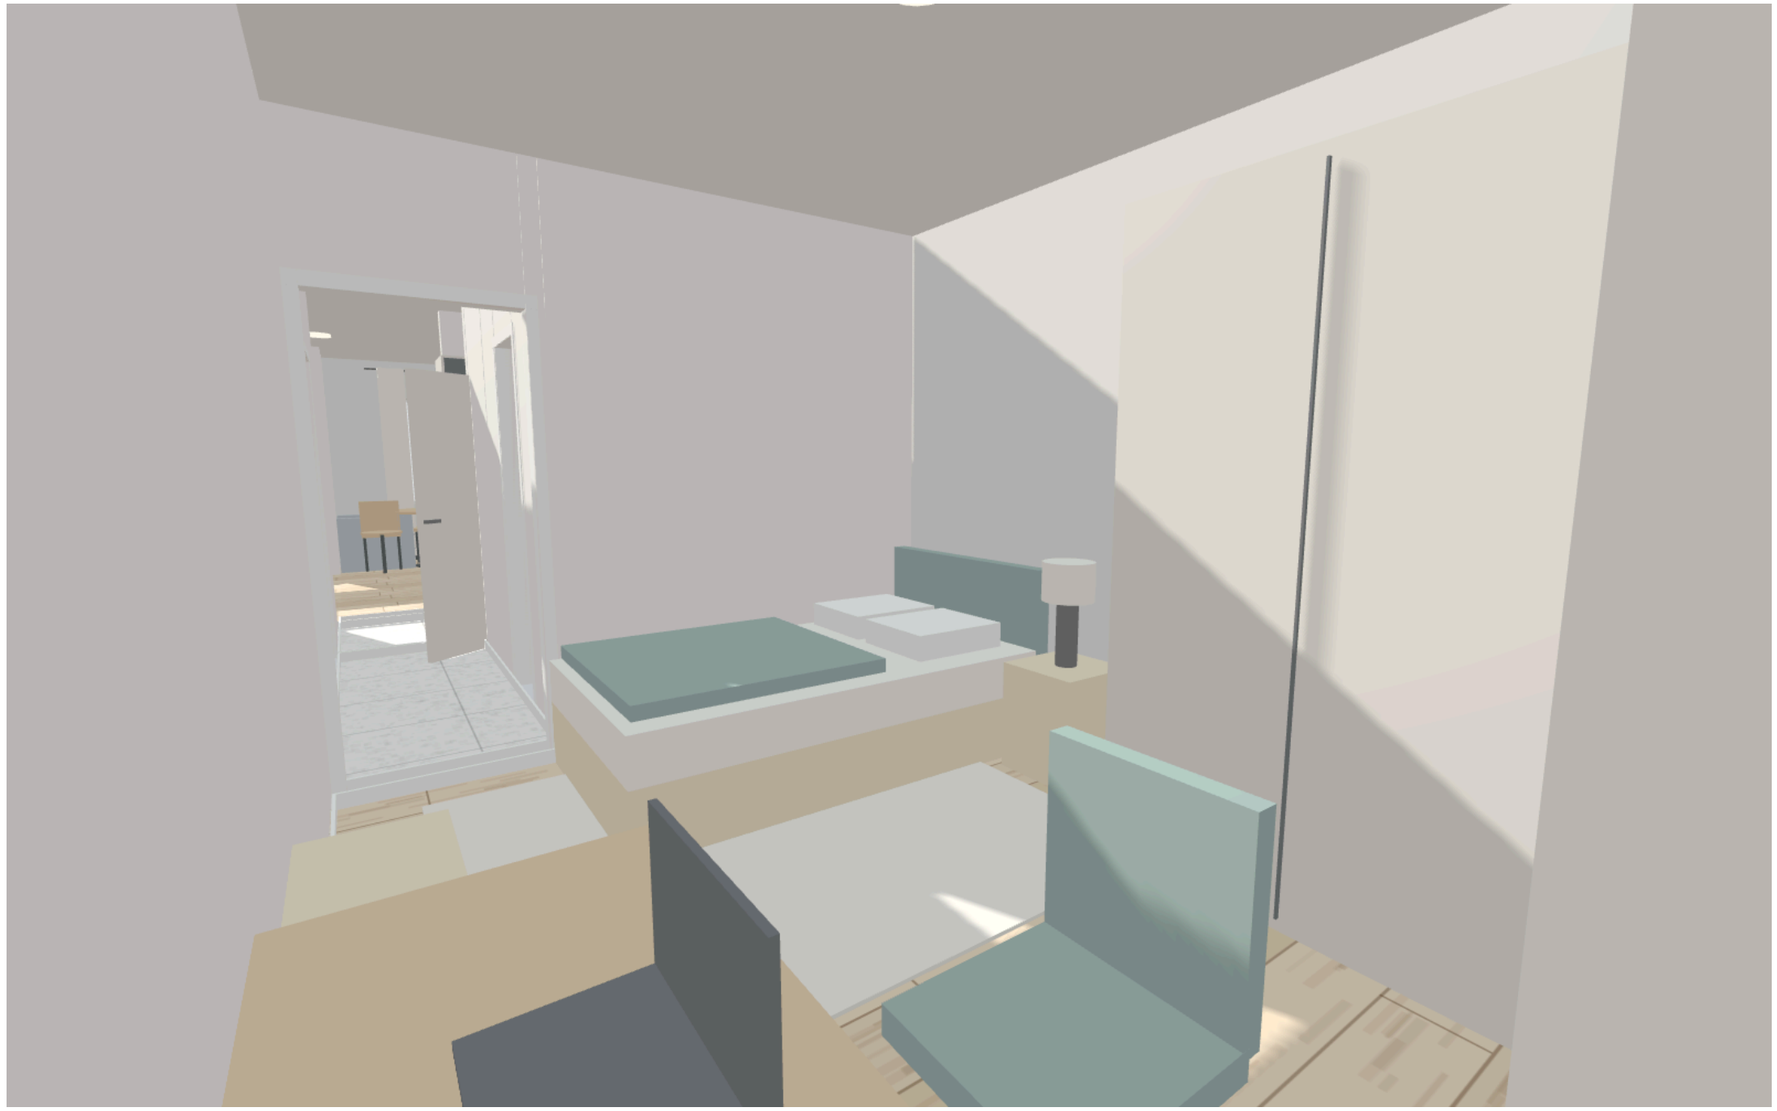




						Дизайн-проект квартиры 20, 6 этаж г. Салехард · планировочное решение №148, вариант 1	№ ДП	Лист	Листов
Изм.	Уч-к	К-во	№ Док.	Подпись	Дата		ДП-20	17	54
Дизайнер						Визуализация детской Ракурс 13	**КВ 20** 3D-модель · альбом		
Рук. проекта									
Заказчик									

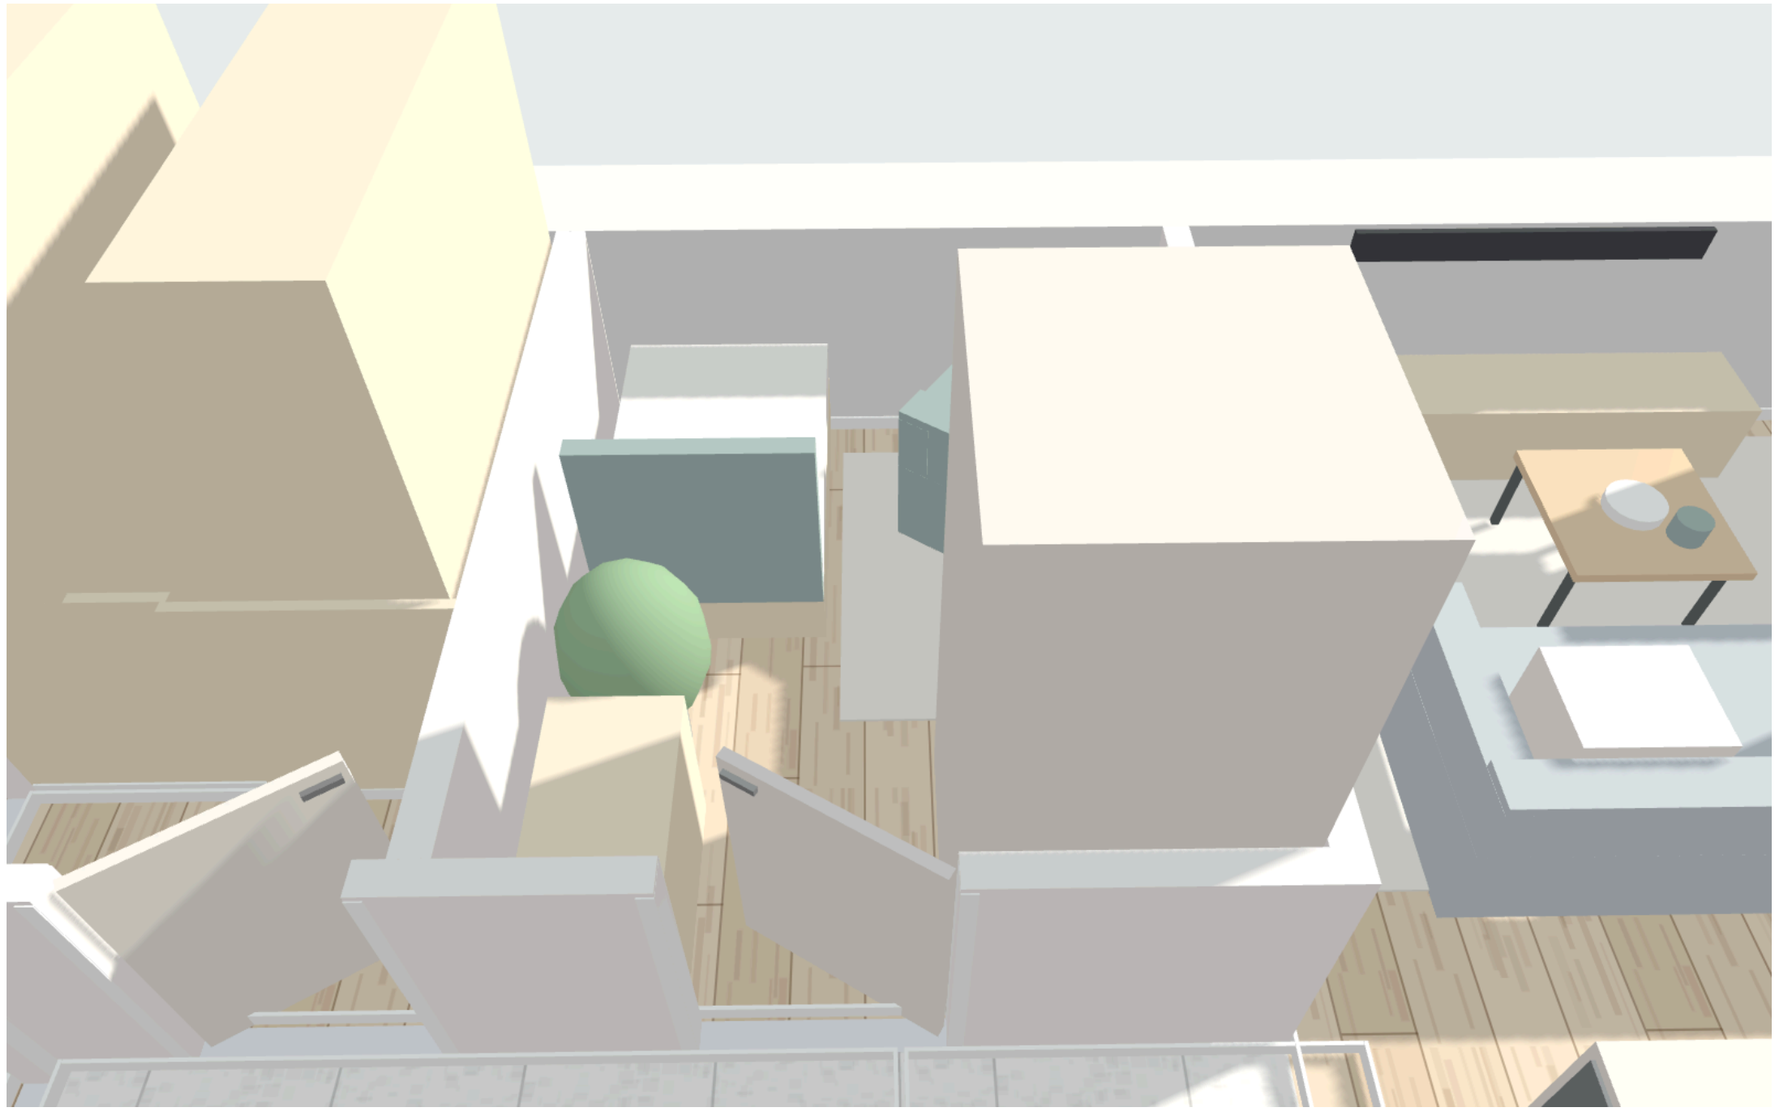

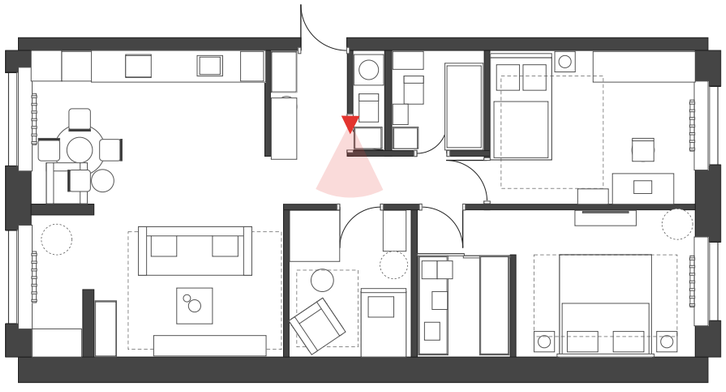



						Дизайн-проект квартиры 20, 6 этаж г. Салехард · планировочное решение №148, вариант 1	№ ДП	Лист	Листов
Изм.	Уч-к	К-во	№ Док.	Подпись	Дата		ДП-20	18	54
Дизайнер						Визуализация кабинета Ракурс 14, вид сверху (стены срезаны)	**КВ 20** 3D-модель · альбом		
Рук. проекта									
Заказчик									

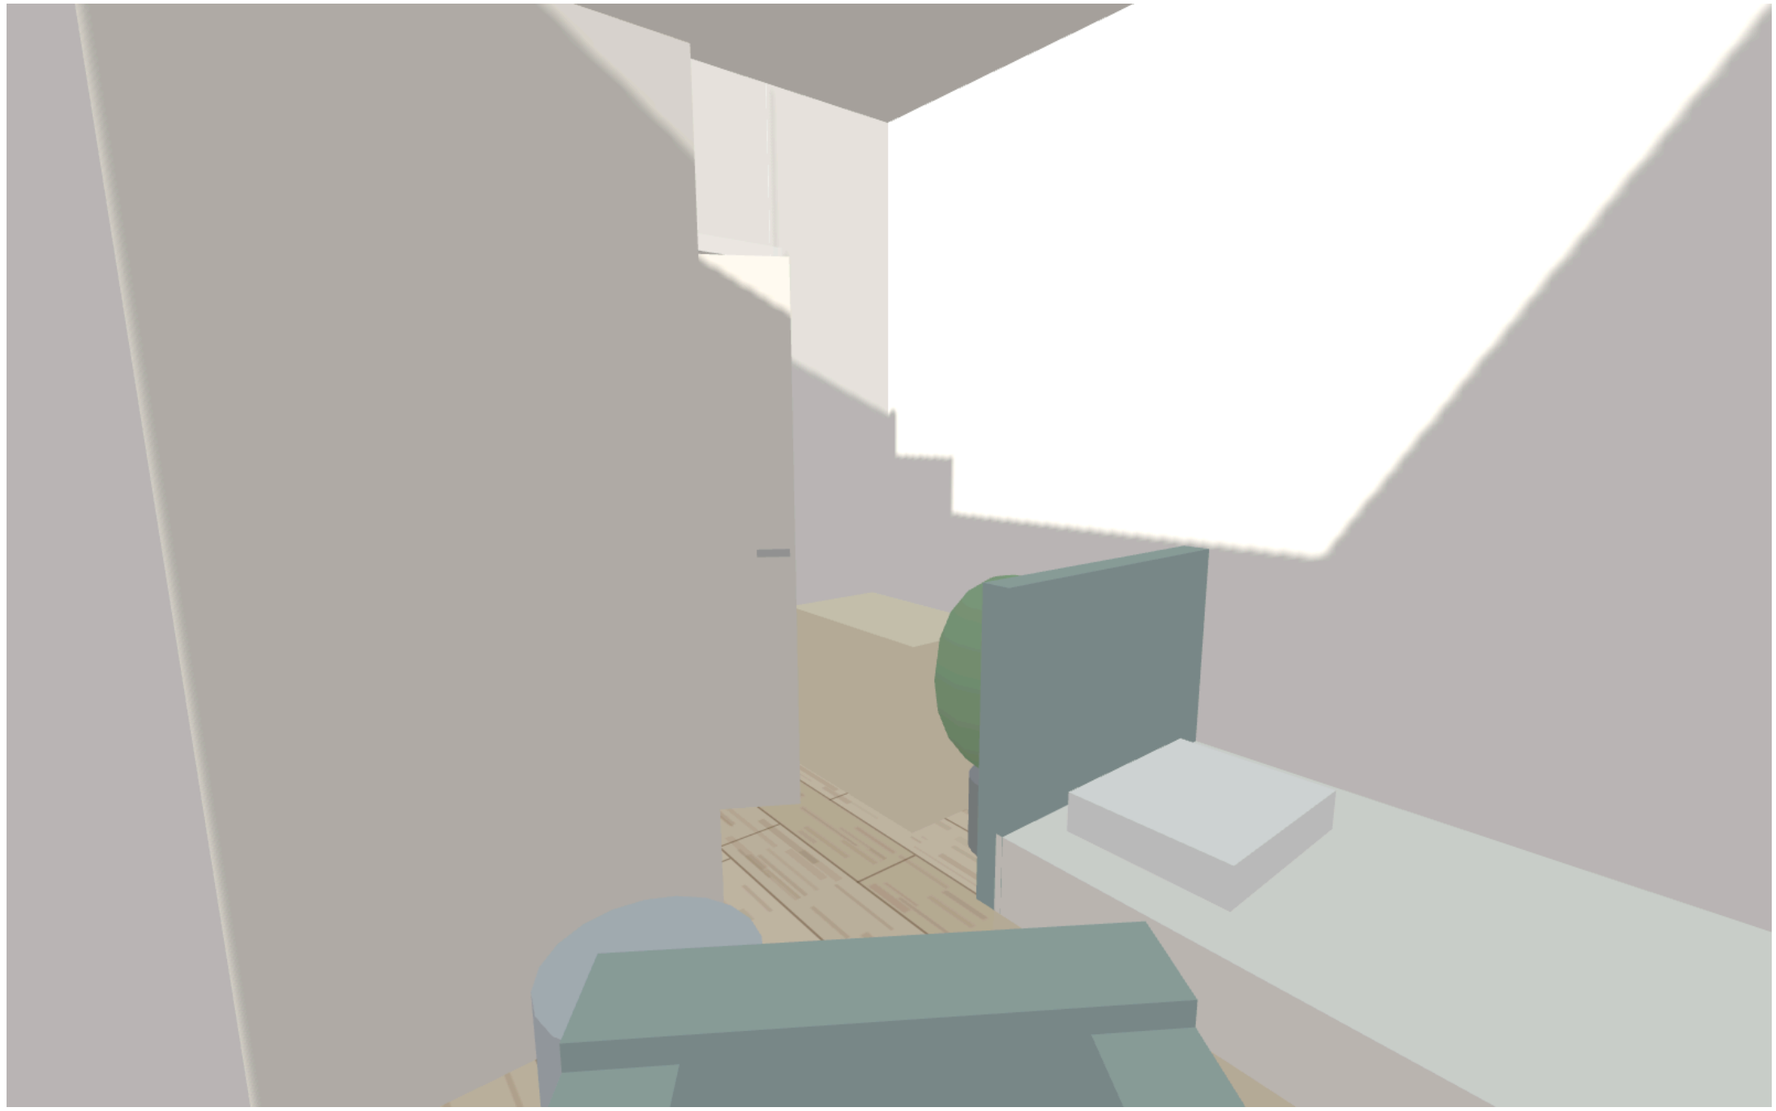





						Дизайн-проект квартиры 20, 6 этаж г. Салехард · планировочное решение №148, вариант 1	№ ДП	Лист	Листов
Изм.	Уч-к	К-во	№ Док.	Подпись	Дата		**ДП-20**	**19**	**54**
Дизайнер						Визуализация кабинета Ракурс 15	**КВ 20** 3D-модель · альбом		
Рук. проекта									
Заказчик									

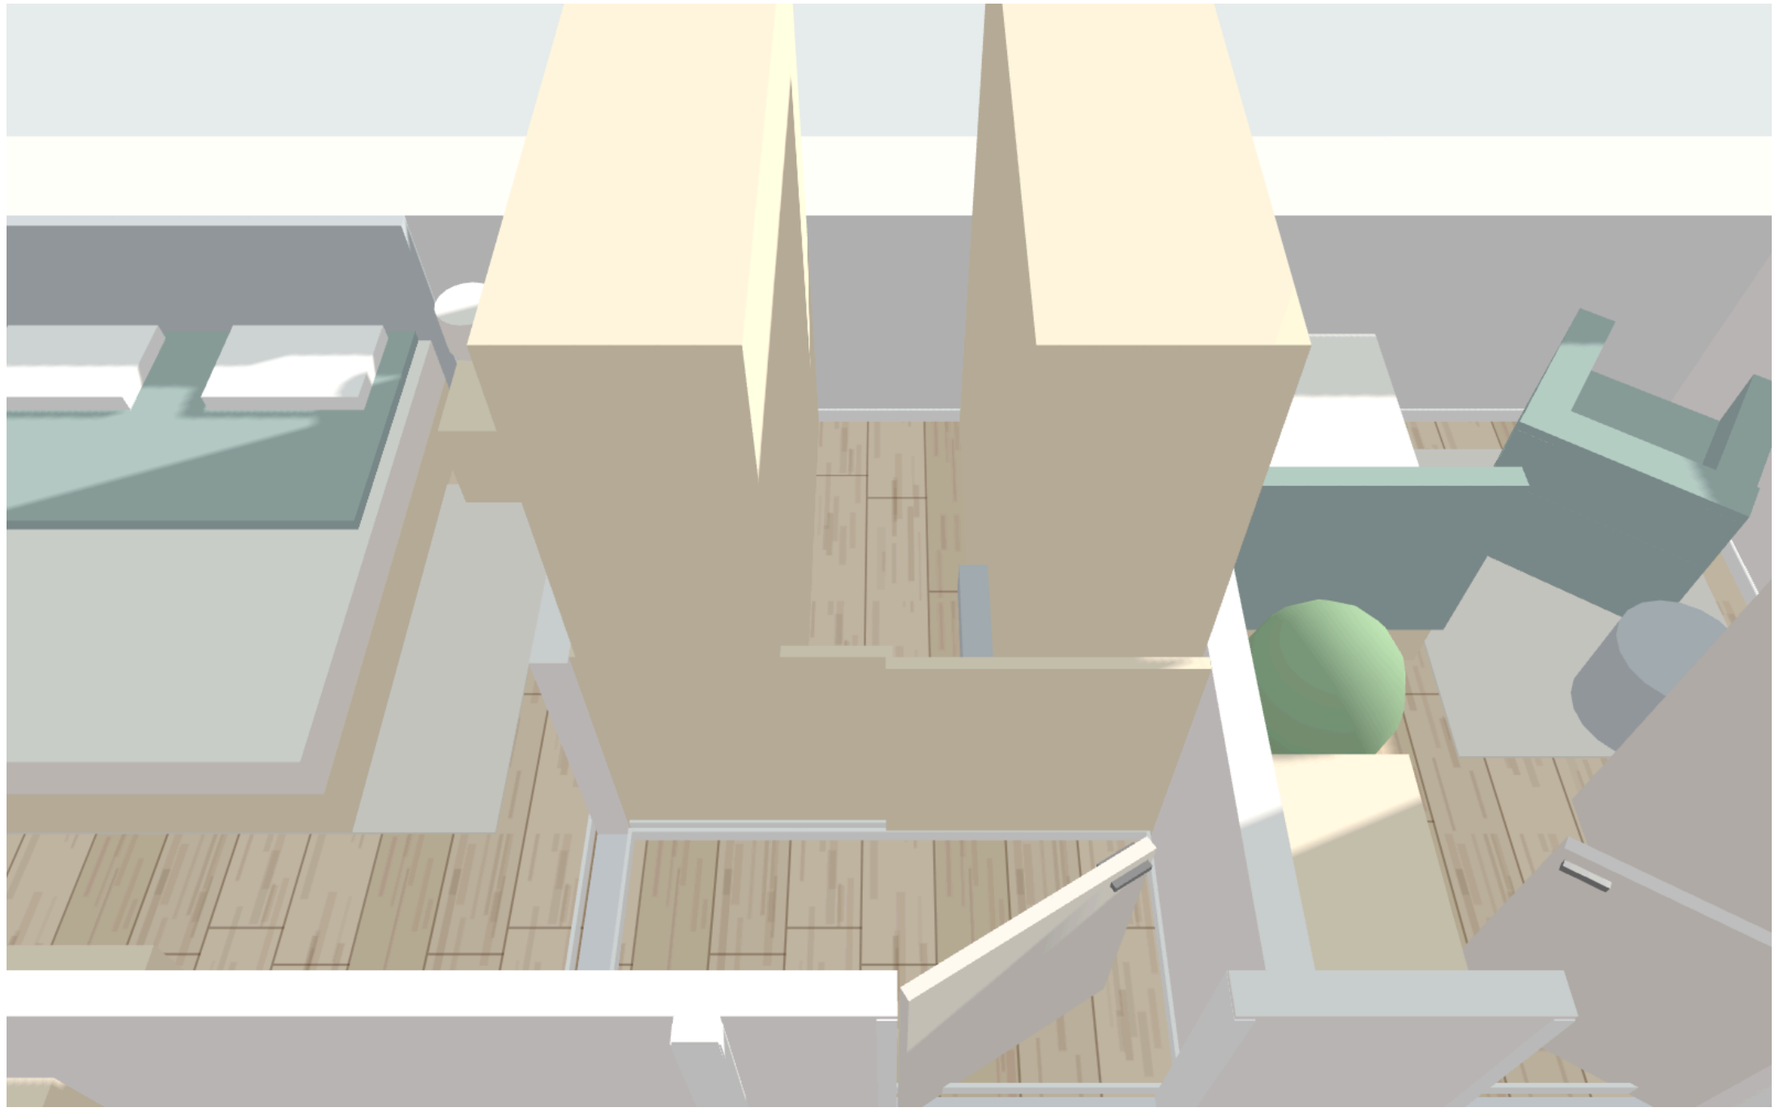

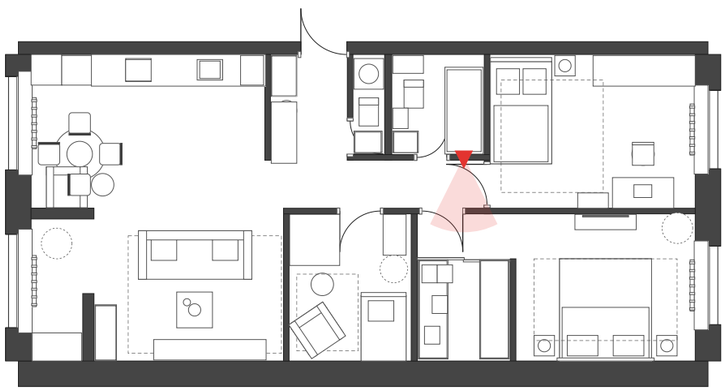


						Дизайн-проект квартиры 20, 6 этаж г. Салехард · планировочное решение №148, вариант 1	№ ДП	Лист	Листов
Изм.	Уч-к	К-во	№ Док.	Подпись	Дата		ДП-20	20	54
Дизайнер						Визуализация гардеробной Ракурс 16, вид сверху (стены срезаны)	**КВ 20** 3D-модель · альбом		
Рук. проекта									
Заказчик									

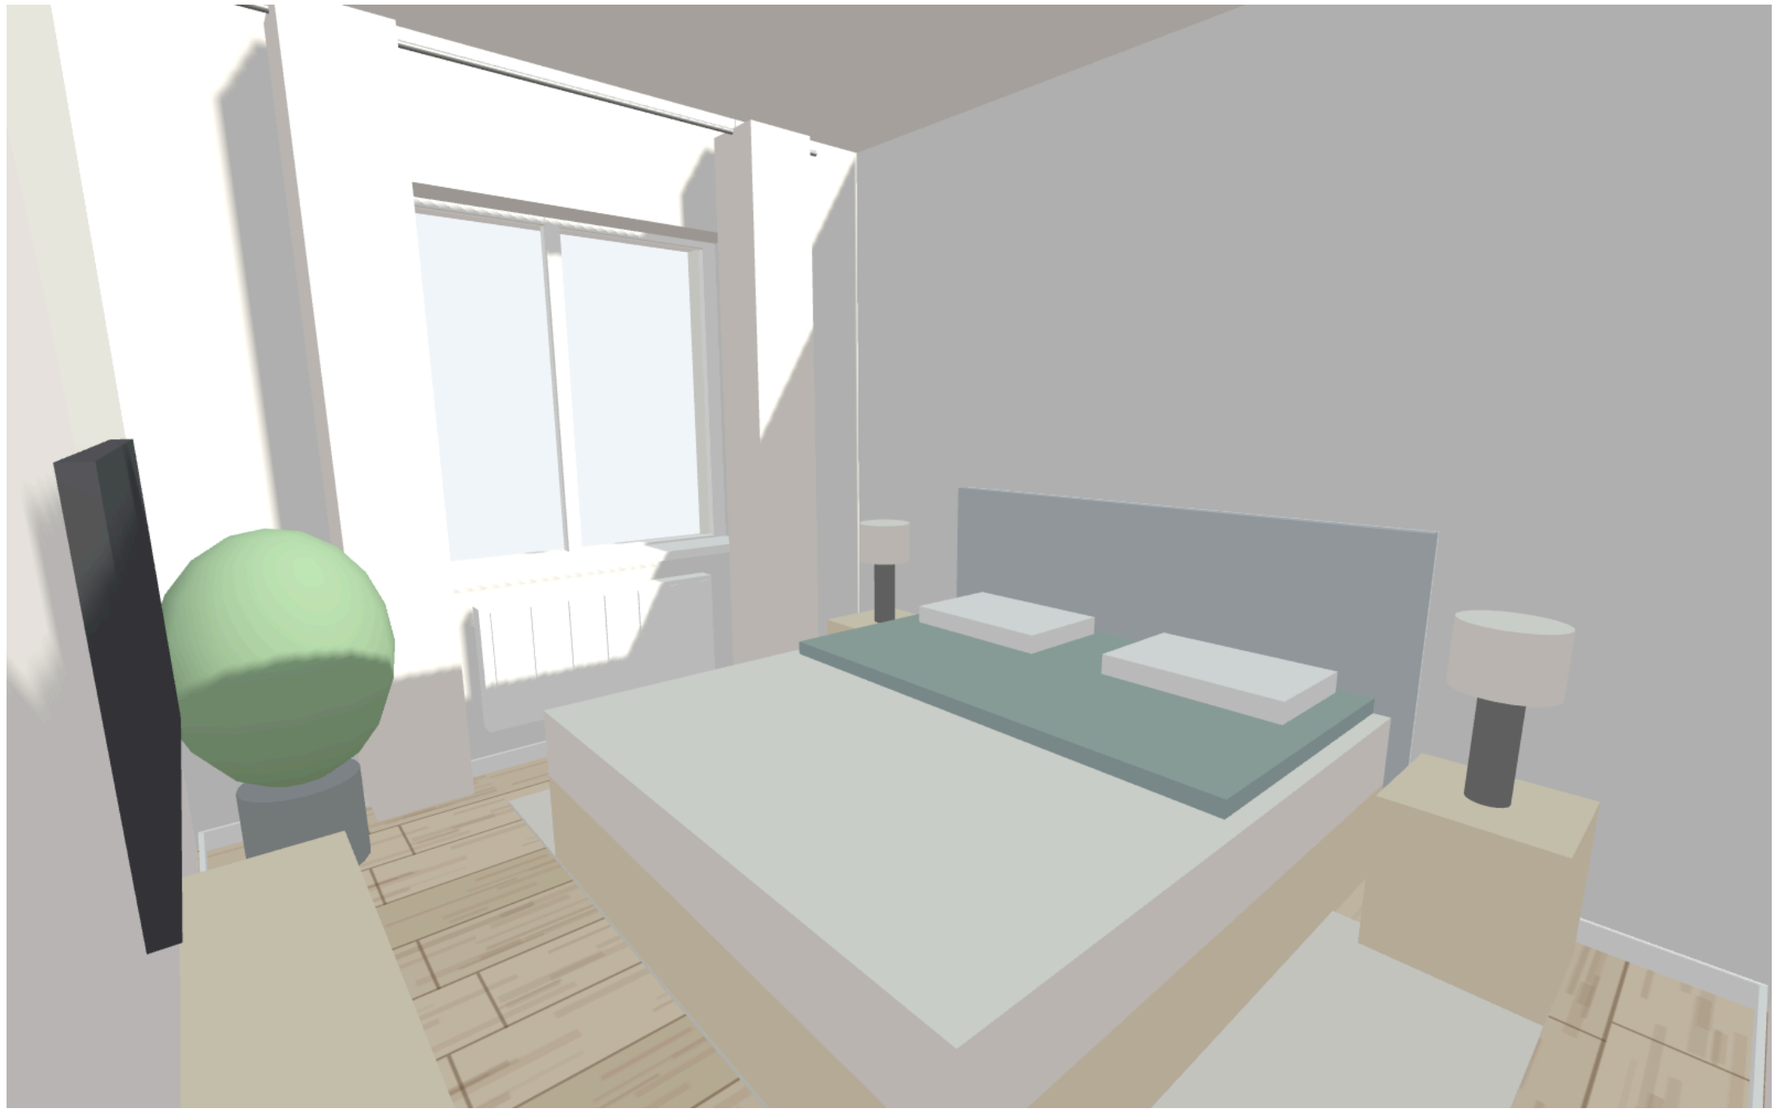

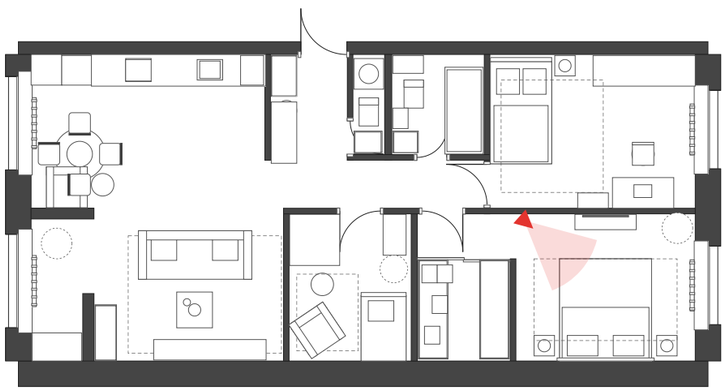



						Дизайн-проект квартиры 20, 6 этаж г. Салехард · планировочное решение №148, вариант 1	№ ДП	Лист	Листов
Изм.	Уч-к	К-во	№ Док.	Подпись	Дата		ДП-20	21	54
Дизайнер						Визуализация спальни Ракурс 17	**КВ 20** 3D-модель · альбом		
Рук. проекта									
Заказчик									

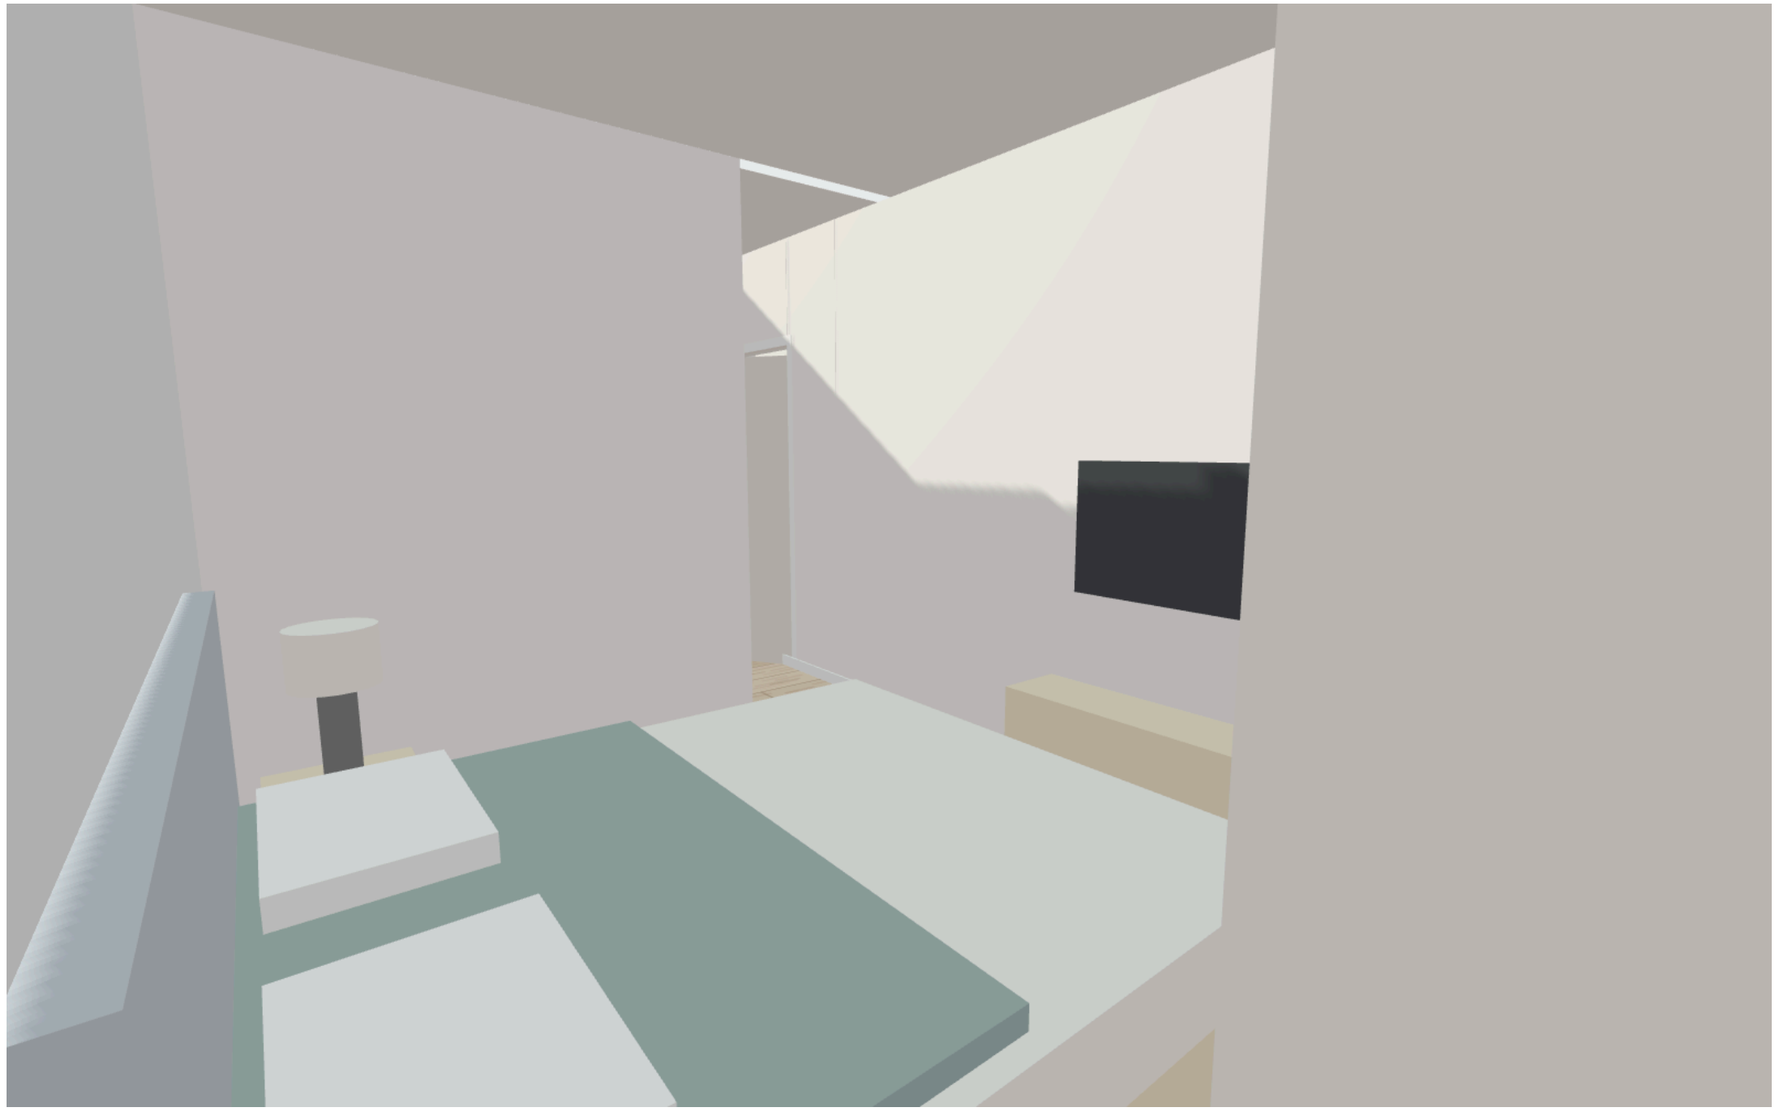



						Дизайн-проект квартиры 20, 6 этаж г. Салехард · планировочное решение №148, вариант 1	№ ДП	Лист	Листов
Изм.	Уч-к	К-во	№ Док.	Подпись	Дата		ДП-20	22	54
Дизайнер						Визуализация спальни Ракурс 18	**КВ 20** 3D-модель · альбом		
Рук. проекта									
Заказчик									

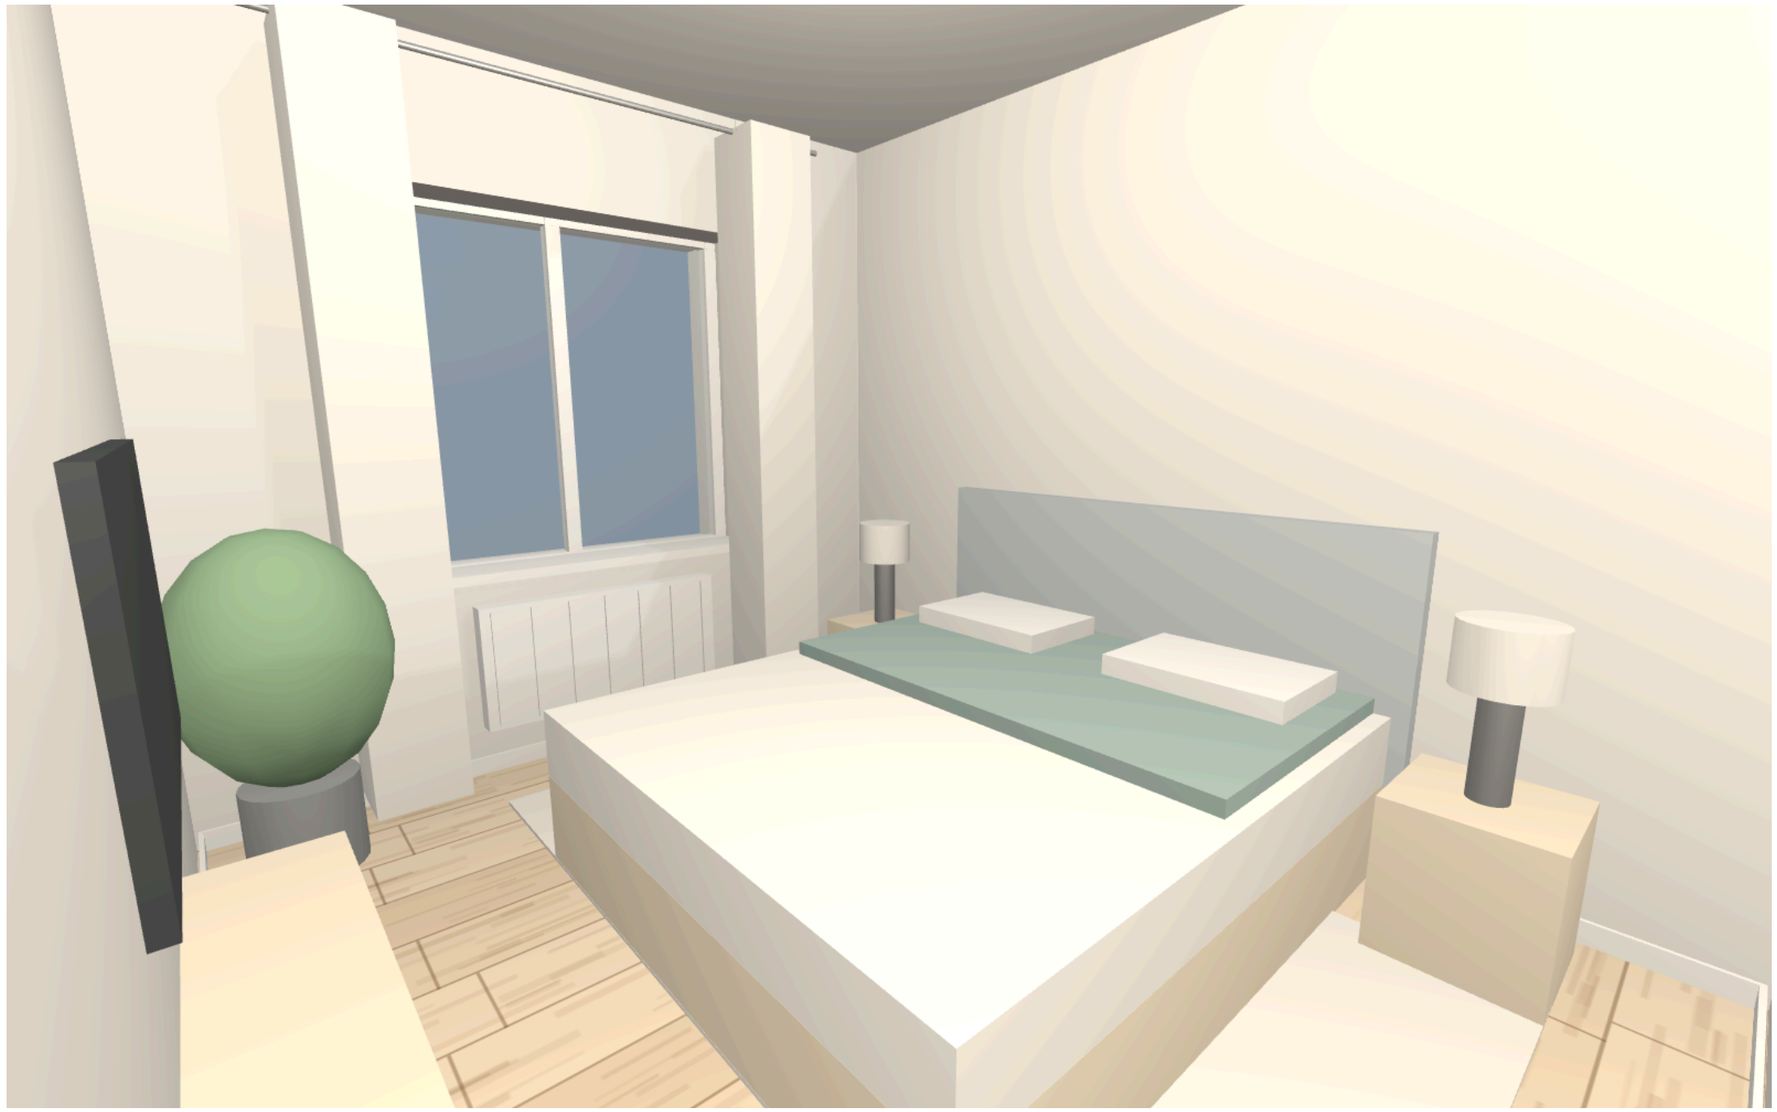

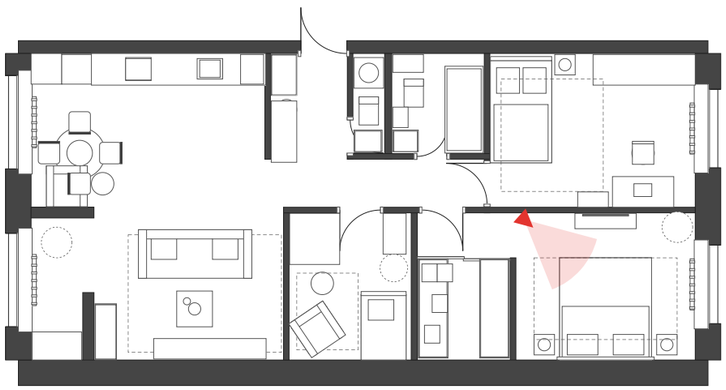

						Дизайн-проект квартиры 20, 6 этаж г. Салехард · планировочное решение №148, вариант 1	№ ДП	Лист	Листов
Изм.	Уч-к	К-во	№ Док.	Подпись	Дата		**ДП-20**	**23**	**54**
Дизайнер						Визуализация спальни Ракурс 19, вечернее освещение	**КВ 20** 3D-модель · альбом		
Рук. проекта									
Заказчик									




Кухня-гостиная · «Светлая»




Кухня-гостиная · «Графит»



Кухня-гостиная · «Тёплая»

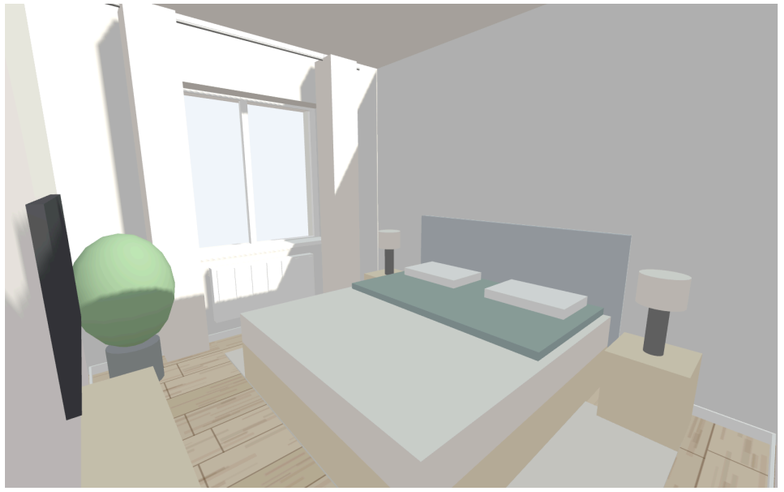

Спальня · «Светлая»

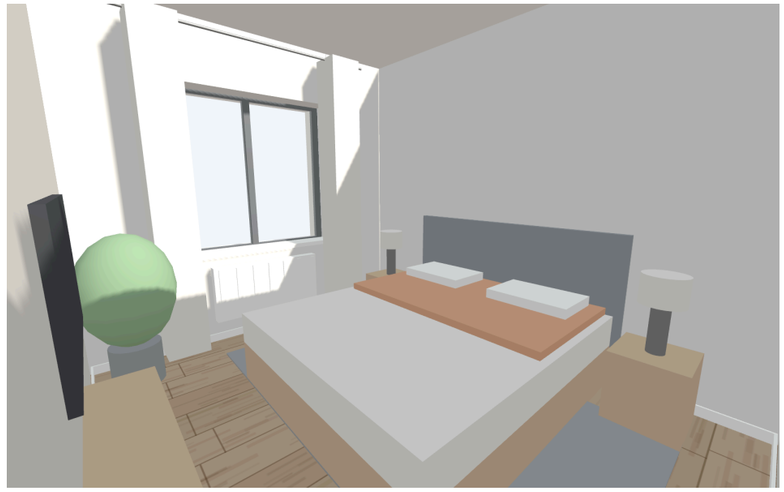

Спальня · «Графит»



Спальня · «Тёплая»

Палитры: «Светлая» — стены #ebe6df, дуб #d9b98f, фасады greige #cfc7bb, акцент шалфей #5f7c75 · «Графит» — стены #bdb6ad, тёмный дуб #8a6a4c, фасады #4a4e53, акцент терракота #b4683f · «Тёплая» — стены #efe3d2, дуб медовый #c99a6a, фасады песочные #d9c3a6, акцент #8a3f2b.

						Дизайн-проект квартиры 20, 6 этаж г. Салехард · планировочное решение №148, вариант 1	№ ДП	Лист	Листов
Изм.	Уч-к	К-во	№ Док.	Подпись	Дата		ДП-20	24	54
Дизайнер						Варианты отделки «Светлая» · «Графит» · «Тёплая»	**КВ 20** 3D-модель · альбом		
Рук. проекта									
Заказчик									




«Графит»



«Тёплая»

						Дизайн-проект квартиры 20, 6 этаж г. Салехард · планировочное решение №148, вариант 1	№ ДП	Лист	Листов
Изм.	Уч-к	К-во	№ Док.	Подпись	Дата		ДП-20	25	54
Дизайнер						Общий вид квартиры Отделка «Графит» и «Тёплая»	**КВ 20** 3D-модель · альбом		
Рук. проекта									
Заказчик									

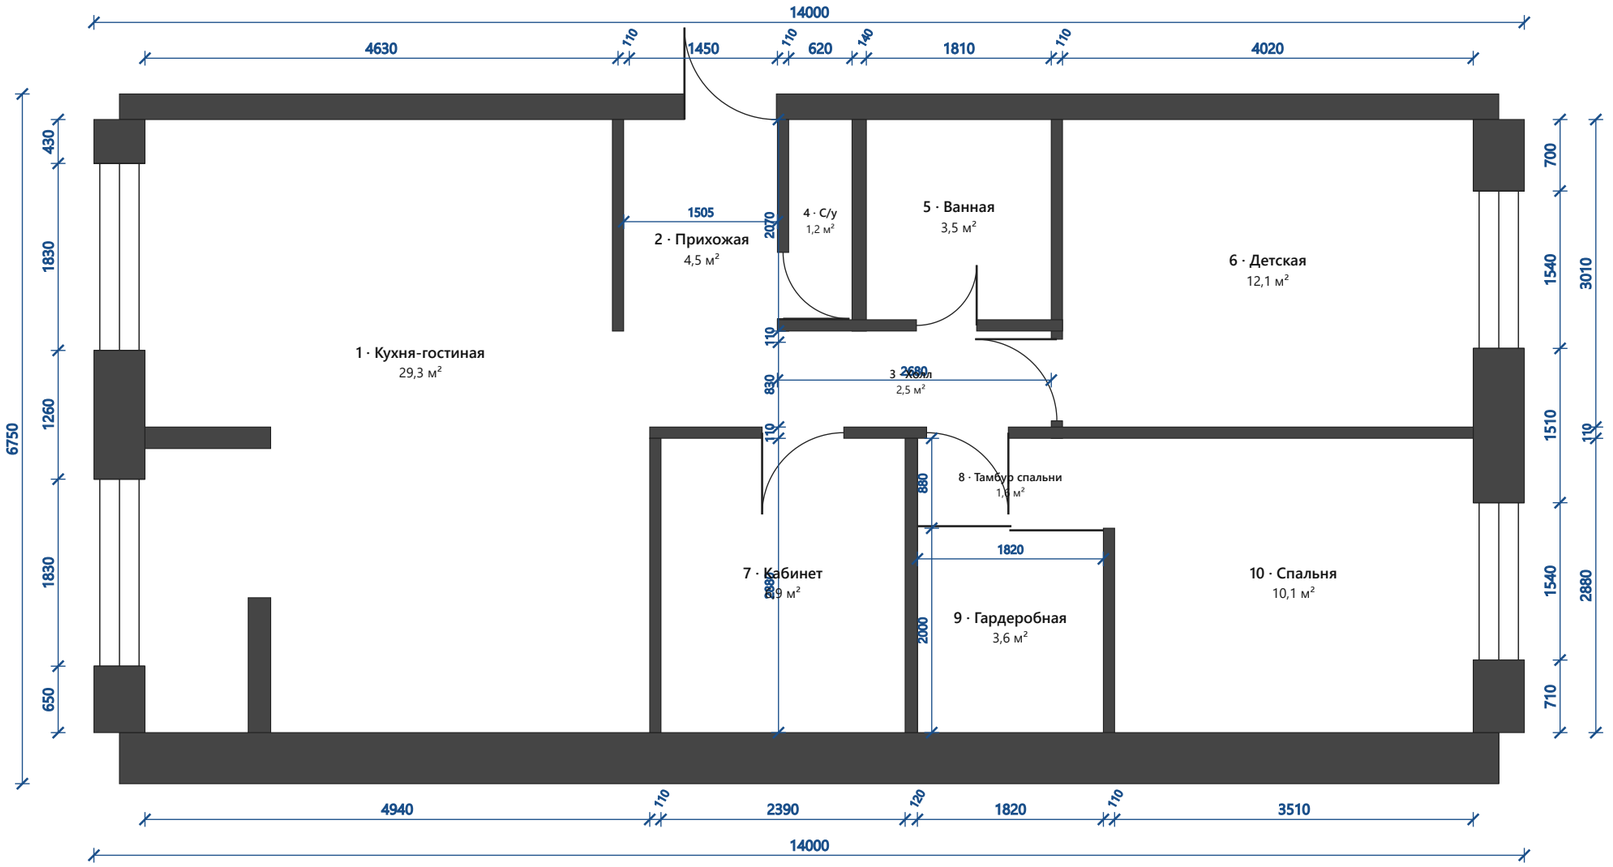


№	Помещение	Пол	Площадь, м²
1	Кухня-гостиная	П-3	29,3
2	Прихожая	П-1	4,5
3	Холл	П-1	2,5
4	Гостевой санузел	П-2	1,2
5	Ванная	П-2	3,5
6	Детская	П-3	12,1
7	Кабинет / вторая детская	П-3	6,9
8	Тамбур спальни	П-3	1,6
9	Гардеробная	П-3	3,6
10	Спальня	П-3	10,1
	Итого по внутреннему контуру		**75,3**
	Общая площадь по плану этажа (штамп кв. 20)		72,8

Примечания

1. Размеры сняты с векторного чертежа планировки №148 (масштаб проверен по цепочке 4570) и подлежат контрольному обмеру по месту.
2. Высота помещений принята 2750 мм (проектная).
3. Площади помещений посчитаны по внутреннему контуру перегородок планировки №148; общая площадь 72,8 м² — по штампу квартиры 20 на плане 6 этажа.
4. Оконные проёмы: 1830 мм — левый торец (2 шт.), 1540 мм — правый торец (2 шт.); низ 800, верх 2250 от чистого пола.

						Дизайн-проект квартиры 20, 6 этаж г. Салехард · планировочное решение №148, вариант 1	№ ДП	Лист	Листов
Изм.	Уч-к	К-во	№ Док.	Подпись	Дата		ДП-20	26	54
Дизайнер						План обмера помещения	**КВ 20** 3D-модель · альбом		
Рук. проекта									
Заказчик									

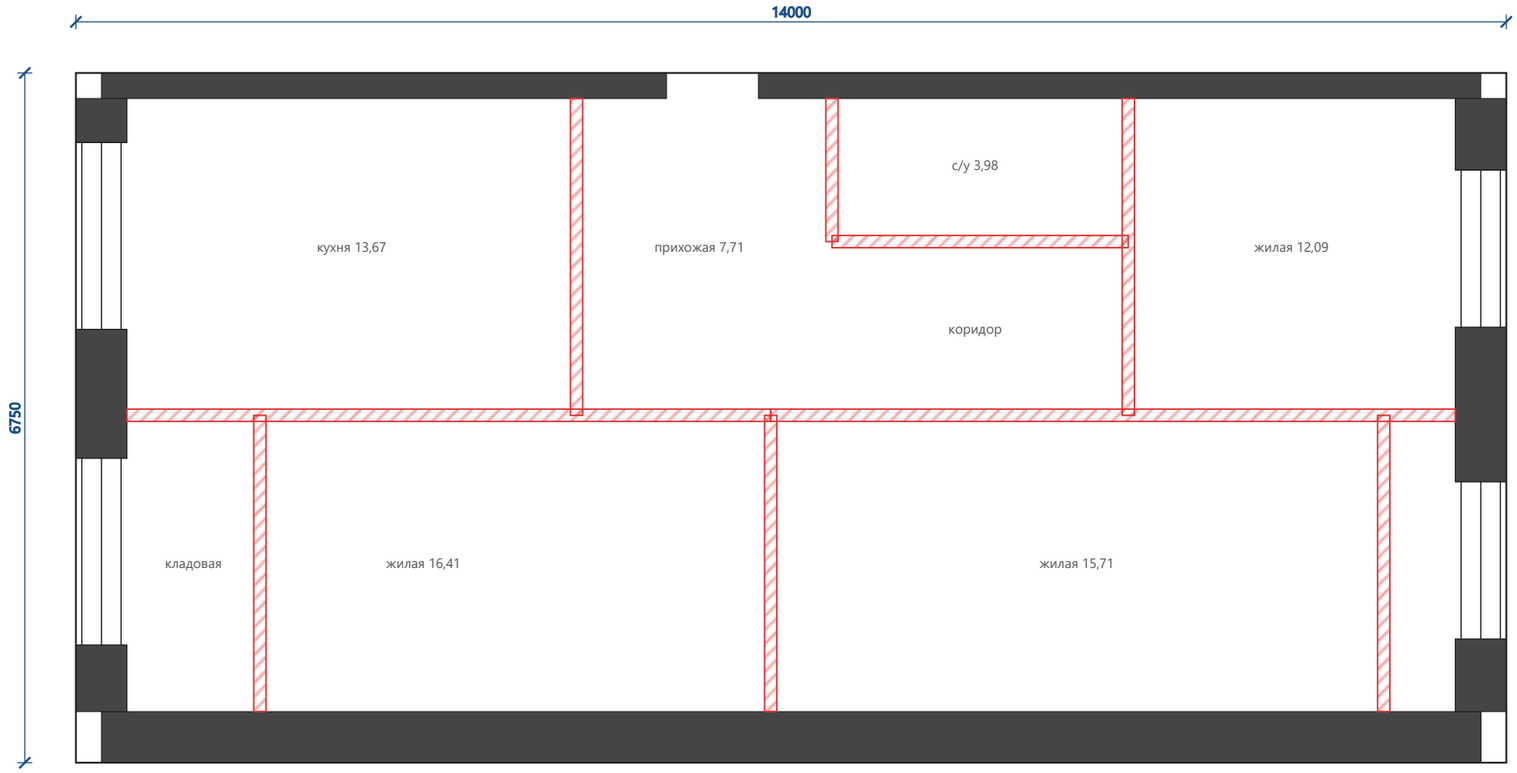


Условные обозначения

- демонтируемые перегородки застройщика (схематично, по плану 6 этажа)
- наружные стены и стена к лестничной клетке — сохраняются

Примечания

1. Положение перегородок застройщика показано схематично по плану 6 этажа (экспликация: кухня 13,67; жилые 16,41 / 15,71 / 12,09; прихожая 7,71; с/у 3,98; кладовая 3,23 м²) и уточняется по факту.
2. Несущие стены, вентканалы и стояки не затрагиваются. До начала работ выполнить обследование и фотофиксацию.
3. Демонтаж сантехнических перегородок — после отключения стояков и согласования с УК.
4. Мусор вывозить по графику УК; полы защитить на время работ.

						Дизайн-проект квартиры 20, 6 этаж г. Салехард · планировочное решение №148, вариант 1	№ ДП	Лист	Листов
Изм.	Уч-к	К-во	№ Док.	Подпись	Дата		ДП-20	27	54
Дизайнер						План демонтажа	**KB 20** 3D-модель · альбом		
Рук. проекта									
Заказчик									

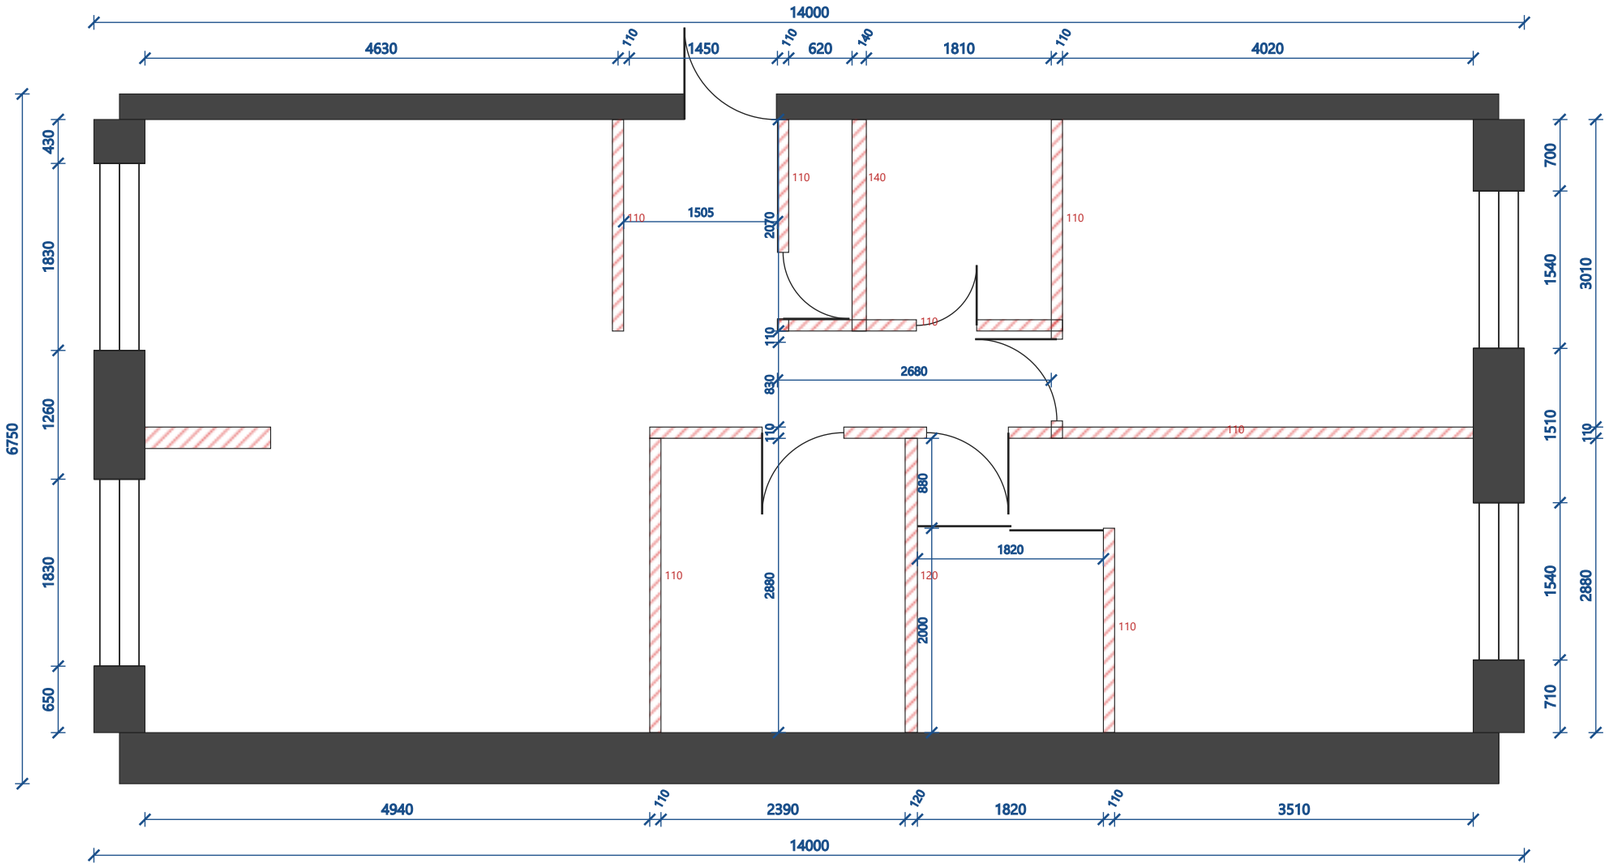


Условные обозначения

- новые перегородки: ПГП 80 / ГКЛ на профиле 100 — по планировке №148 (толщина в чистоте 110–140 мм)
- существующие стены
- Ø дверные проёмы: ширина — по плану дверей, высота 2100

Примечания

1. Перегородки санузлов — из влагостойких материалов (ПГП гидрофобизированный / ГКЛВ); в мокрых зонах — гидроизоляция пола с заходом на стены 200 мм.
2. Привязки перегородок — от чистовых поверхностей наружных стен; углы помещений 90°.
3. Размеры проёмов даны в штукатурке; заказ дверей — после снятия замеров с готовых проёмов.
4. Электрощит — в прихожей у входной двери; трассы инженерных сетей — по соответствующим планам.

						Дизайн-проект квартиры 20, 6 этаж г. Салехард · планировочное решение №148, вариант 1	№ ДП	Лист	Листов
Изм.	Уч-к	К-во	№ Док.	Подпись	Дата		ДП-20	28	54
Дизайнер						План монтажа перегородок	**KB 20** 3D-модель · альбом		
Рук. проекта									
Заказчик									

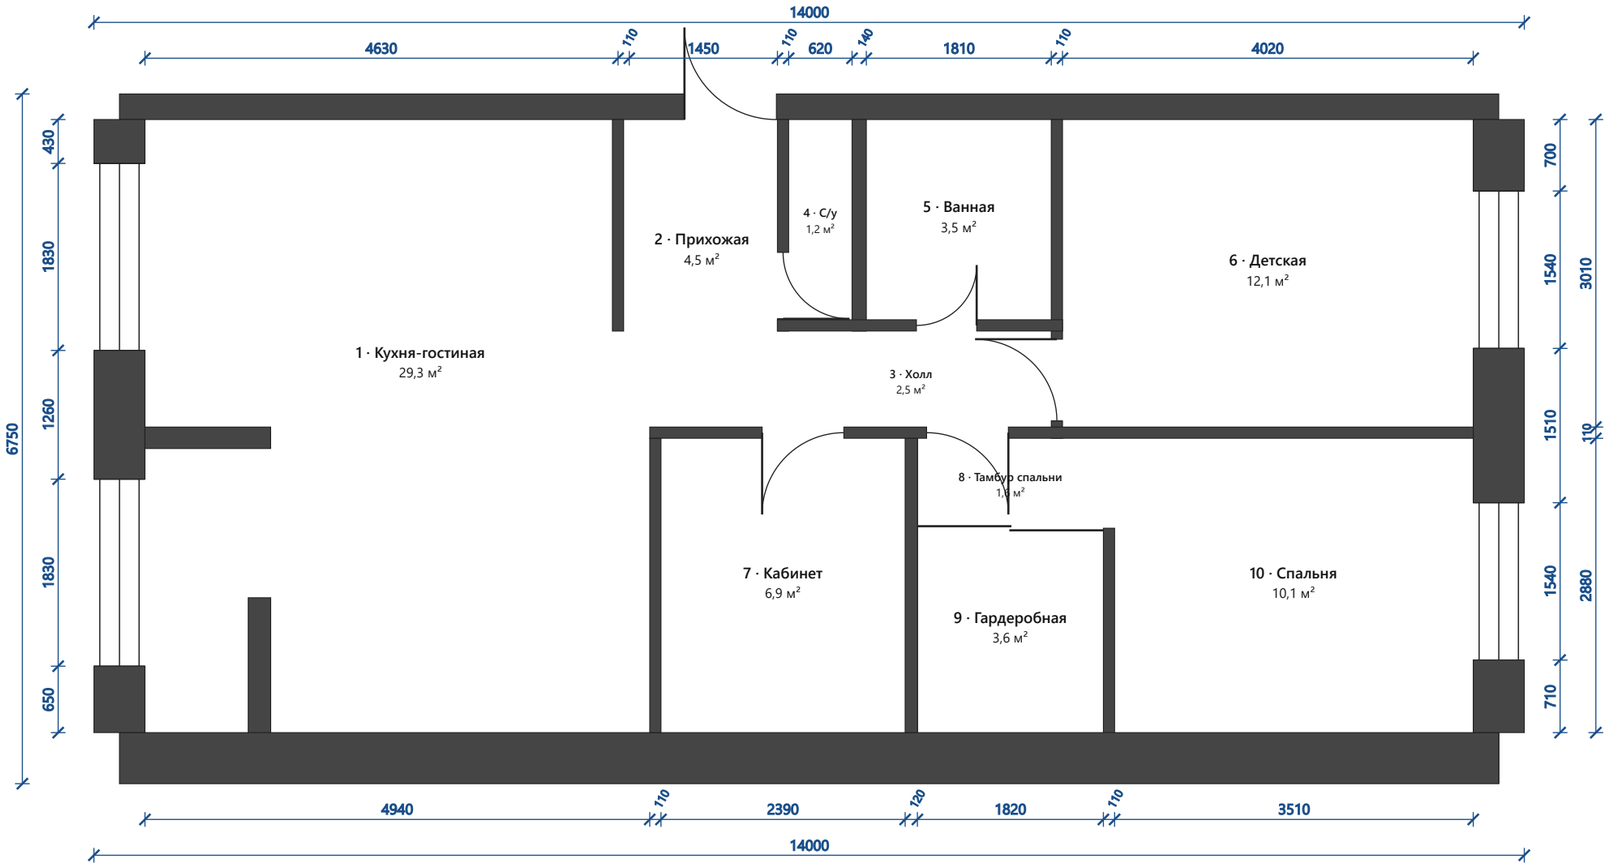


№	Помещение	Пол	Площадь, м²
1	Кухня-гостиная	П-3	29,3
2	Прихожая	П-1	4,5
3	Холл	П-1	2,5
4	Гостевой санузел	П-2	1,2
5	Ванная	П-2	3,5
6	Детская	П-3	12,1
7	Кабинет / вторая детская	П-3	6,9
8	Тамбур спальни	П-3	1,6
9	Гардеробная	П-3	3,6
10	Спальня	П-3	10,1
	Итого по внутреннему контуру		**75,3**
	Общая площадь по плану этажа (штамп кв. 20)		72,8

Примечания

1. Нумерация помещений — единая для всех листов альбома.
2. Площади — по внутреннему контуру, без учёта отделки.

						Дизайн-проект квартиры 20, 6 этаж г. Салехард · планировочное решение №148, вариант 1	№ ДП	Лист	Листов
Изм.	Уч-к	К-во	№ Док.	Подпись	Дата		ДП-20	29	54
Дизайнер						Строительный план с экспликацией помещений	**КВ 20** 3D-модель · альбом		
Рук. проекта									
Заказчик									

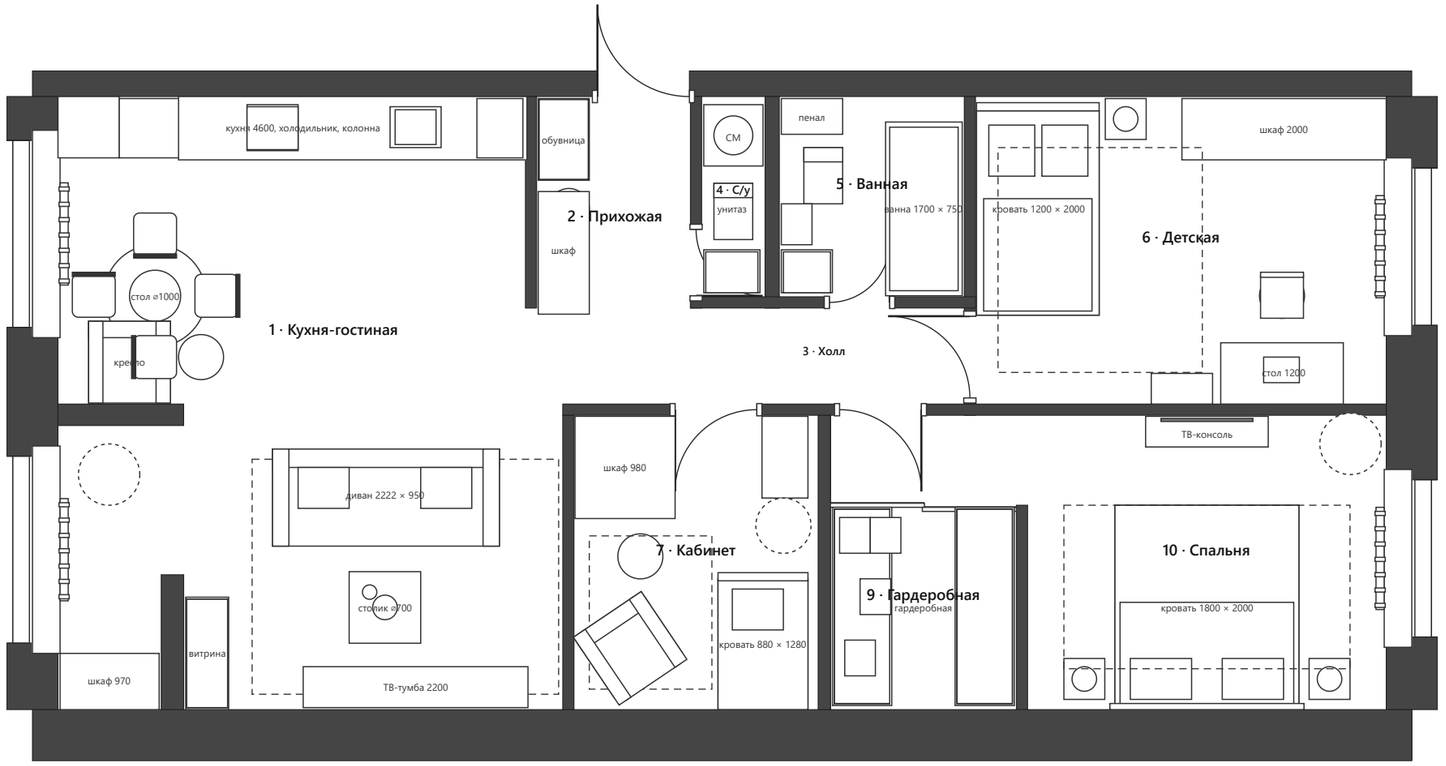




Та же расстановка на 3D-модели (вид сверху, стены срезаны на 1,1 м)

Примечания

1. Габариты мебели — по планировке №148 и 3D-модели; перед заказом уточнить по каталогам выбранных моделей.
2. Встроенная мебель (кухня, шкафы, гардеробная) — по чертежам раздела «Чертежи мебели».
3. Проходы не менее 700 мм; у кровати в спальне — по 800 мм с обеих сторон.
4. Размеры на плане даны условно; окончательные — по контрольному обмеру.

						Дизайн-проект квартиры 20, 6 этаж г. Салехард · планировочное решение №148, вариант 1	№ ДП	Лист	Листов
Изм.	Уч-к	К-во	№ Док.	Подпись	Дата		ДП-20	30	54
Дизайнер						План расположения мебели и оборудования	**КВ 20** 3D-модель · альбом		
Рук. проекта									
Заказчик									

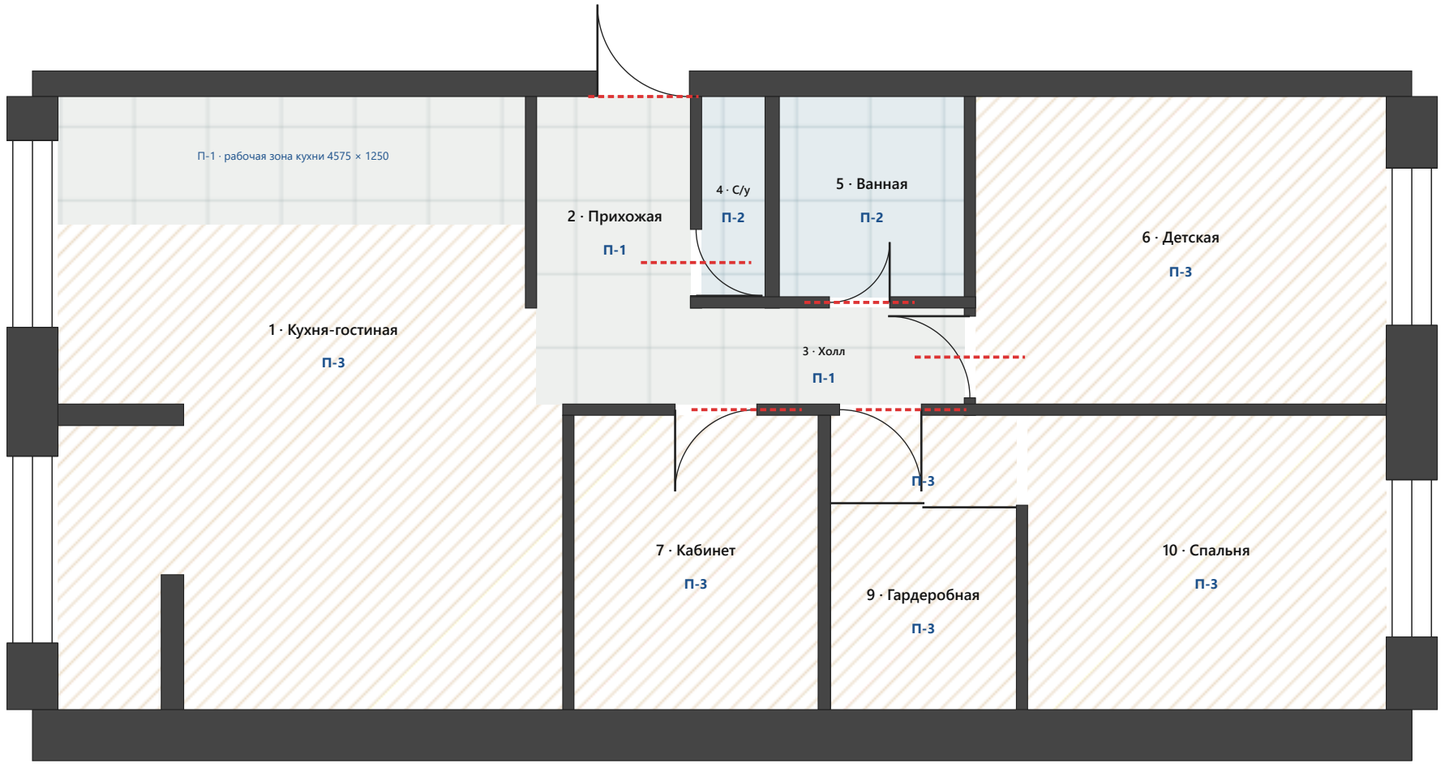

Марка	Покрытие	Помещения	м²
П-1	Керамогранит 600 × 600, светлый камень, матовый	прихожая, холл	12,7
П-2	Керамогранит 600 × 600 R10 (нескользящий), под светлый камень	санузлы	4,7
П-3	Инженерная доска, дуб натуральный, ёлочка 110 × 550	жилые комнаты, кухня-гостиная, кабинет, гардеробная	57,9
—	Порог / стык покрытий: Т-образный профиль, латунь матовая	в дверных проёмах	6 шт.

Примечания

1. Расход — площадь + 7 % (ёлочка — + 12 %). Направление укладки доски — вдоль длинной стены комнаты.
2. Под доску — фанера 12 мм на стяжке / клеевая укладка; под керамогранит — выравнивающая стяжка, в мокрых зонах — гидроизоляция.
3. Плинтус — по плану плинтусов. Стыки покрытий — по оси дверного полотна.

						Дизайн-проект квартиры 20, 6 этаж г. Салехард · планировочное решение №148, вариант 1	№ ДП	Лист	Листов
Изм.	Уч-к	К-во	№ Док.	Подпись	Дата		ДП-20	31	54
Дизайнер						План пола спецификация напольных покрытий	**KB 20** 3D-модель · альбом		
Рук. проекта									
Заказчик									



Условные обозначения


— Пл-1: плинтус МДФ 80 × 16 мм, крашенный в цвет стен (RAL 9001), скрытое крепление — 81 м.п. (за вычетом проёмов и встроенной мебели)

— в санузлах плинтус не ставится: плитка стен до пола, затирка в цвет

Примечания

1. Плинтус заводить под дверные наличники; стыки — под 45°, внутренние углы — запил.
2. За встроенной мебелью (кухня, шкафы до потолка, гардеробная) плинтус не устанавливается.
3. Кабель-каналы в плинтусе не предусмотрены: разводка — в стенах.

						Дизайн-проект квартиры 20, 6 этаж г. Салехард · планировочное решение №148, вариант 1	№ ДП	Лист	Листов
Изм.	Уч-к	К-во	№ Док.	Подпись	Дата		ДП-20	32	54
Дизайнер						План плинтусов	**КВ 20** 3D-модель · альбом		
Рук. проекта									
Заказчик									

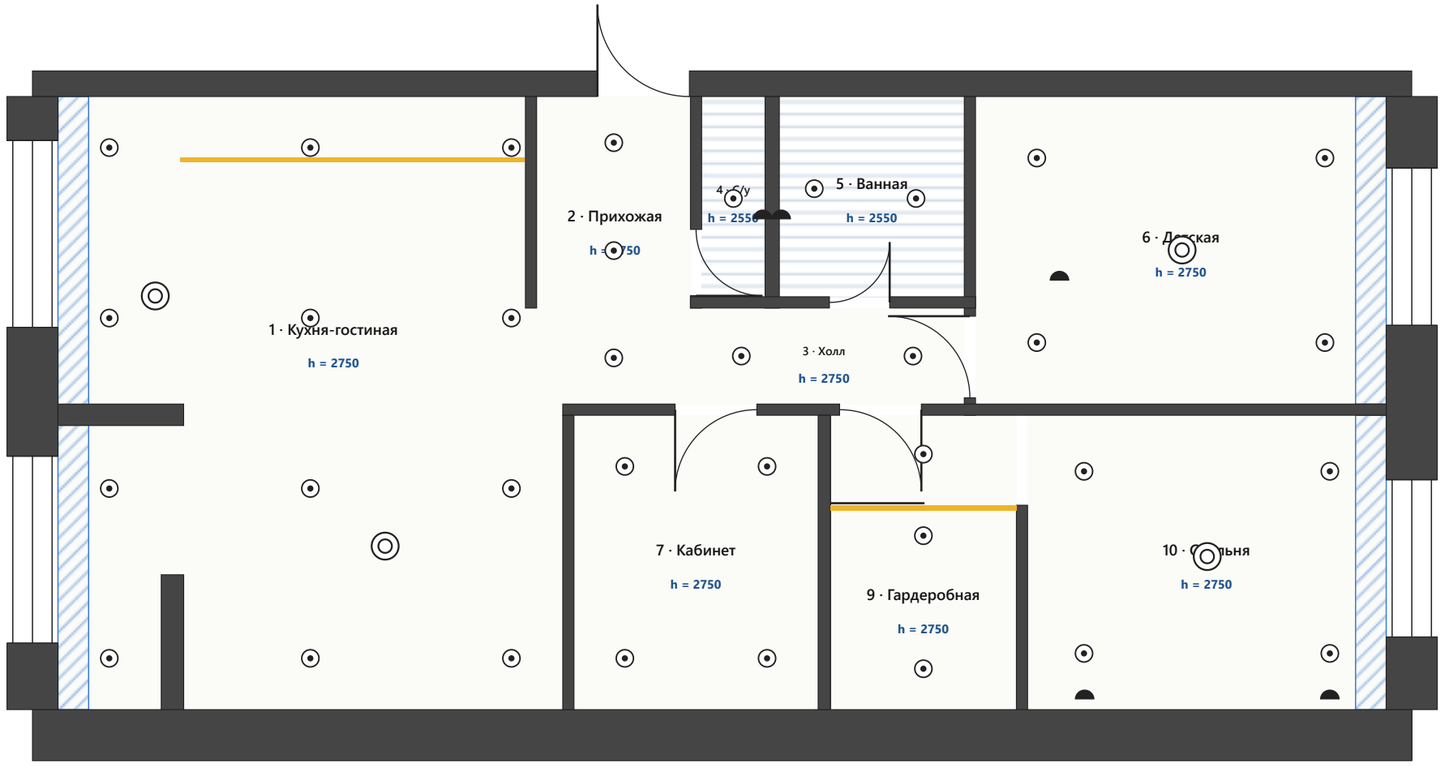


Условные обозначения

- основной потолок: штукатурка, краска матовая, h = 2750
- ГКЛВ на каркасе, h = 2550 (санузлы — доступ к коммуникациям)
- ниша для штор 300 мм вдоль окон (ГКЛ-короб, карниз скрытый)
- встроенный светильник GU10 / LED 7 Вт, 3000 K — 35 шт.
- подвесной светильник — 4 шт.
- бра / настенный светильник — 5 шт.
- LED-лента 3000 K в профиле: подсветка кухни под навесными шкафами, гардеробная

Примечания

1. Все светильники — тёплый свет 3000 K, CRI ≥ 90; диммирование — общий свет гостиной и спальни.
2. Привязки светильников — от осей помещений, по плану; окончательные — по месту с учётом мебели.
3. Над столом — подвес на высоте 750 мм от столешницы; над диваном — подвес 1 шт. (центр зоны).

						Дизайн-проект квартиры 20, 6 этаж г. Салехард · планировочное решение №148, вариант 1	№ ДП	Лист	Листов
Изм.	Уч-к	К-во	№ Док.	Подпись	Дата		ДП-20	33	54
Дизайнер						План потолка и освещения	**КВ 20** 3D-модель · альбом		
Рук. проекта									
Заказчик									

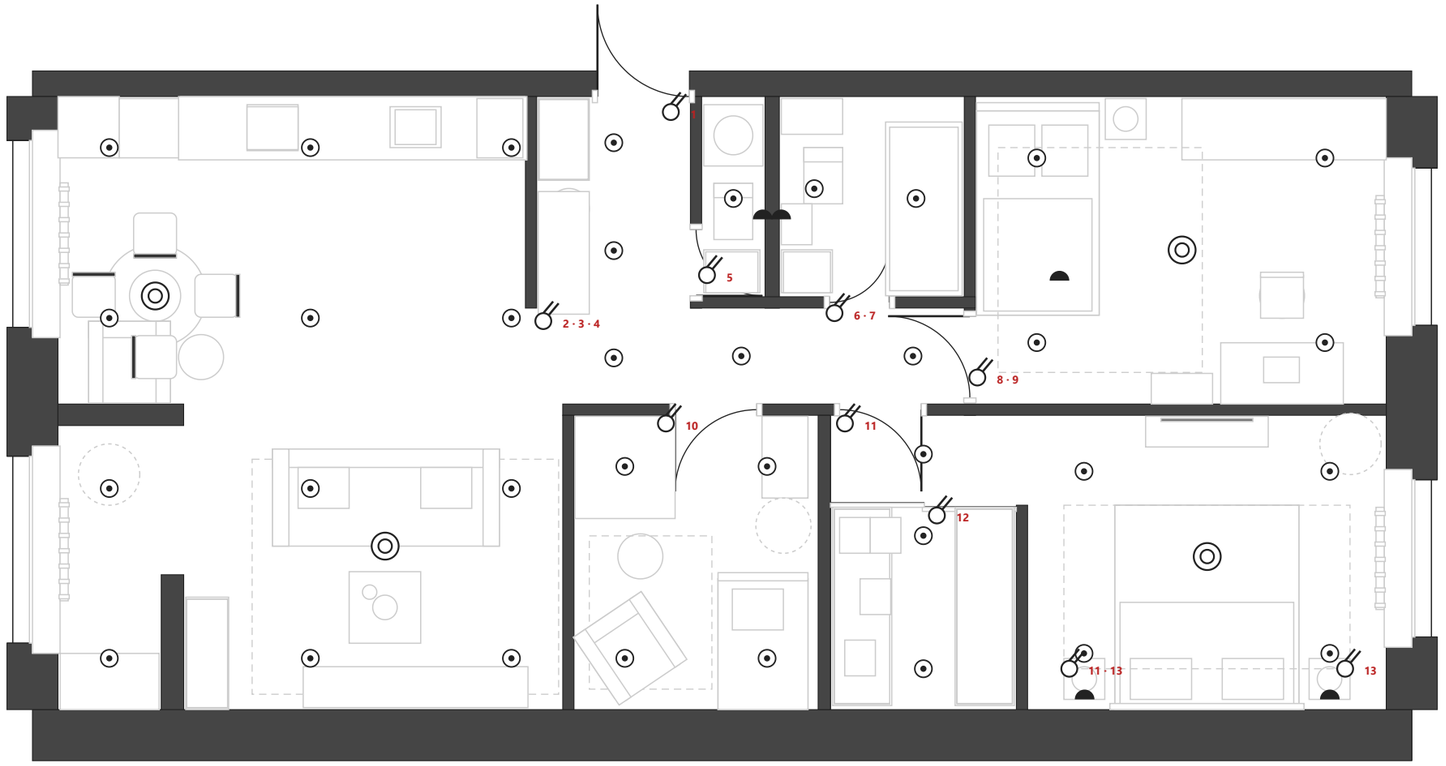


Группа	Выключатель	Управляет
1	прихожая, холл	общий свет
2 · 3 · 4	кухня-гостиная	общий / подвесы / LED
5	санузел	общий свет
6 · 7	ванная	общий / зеркало
8 · 9	детская	общий / подвес
10	кабинет	общий свет
11	спальня (вход)	общий
12	гардеробная + LED	общий свет
11 · 13	спальня	проходной у кровати, бра
13	бра	общий свет

Примечания

1. Выключатели — на высоте 900 мм от чистого пола, в 100–150 мм от наличника со стороны ручки.
2. Спальня: проходные выключатели у входа и у кровати (группа 11); бра — с отдельных клавиш у кровати.
3. Гостиная: три клавиши — общий свет, подвесы над столом и диваном, LED-подсветка кухни.
4. Санузлы: выключатели снаружи у двери. Все группы — через щит с автоматами 10 А.

						Дизайн-проект квартиры 20, 6 этаж г. Салехард · планировочное решение №148, вариант 1	№ ДП	Лист	Листов
Изм.	Уч-к	К-во	№ Док.	Подпись	Дата		ДП-20	34	54
Дизайнер						План привязки выключателей к группам освещения	KB 20 3D-модель · альбом		
Рук. проекта									
Заказчик									

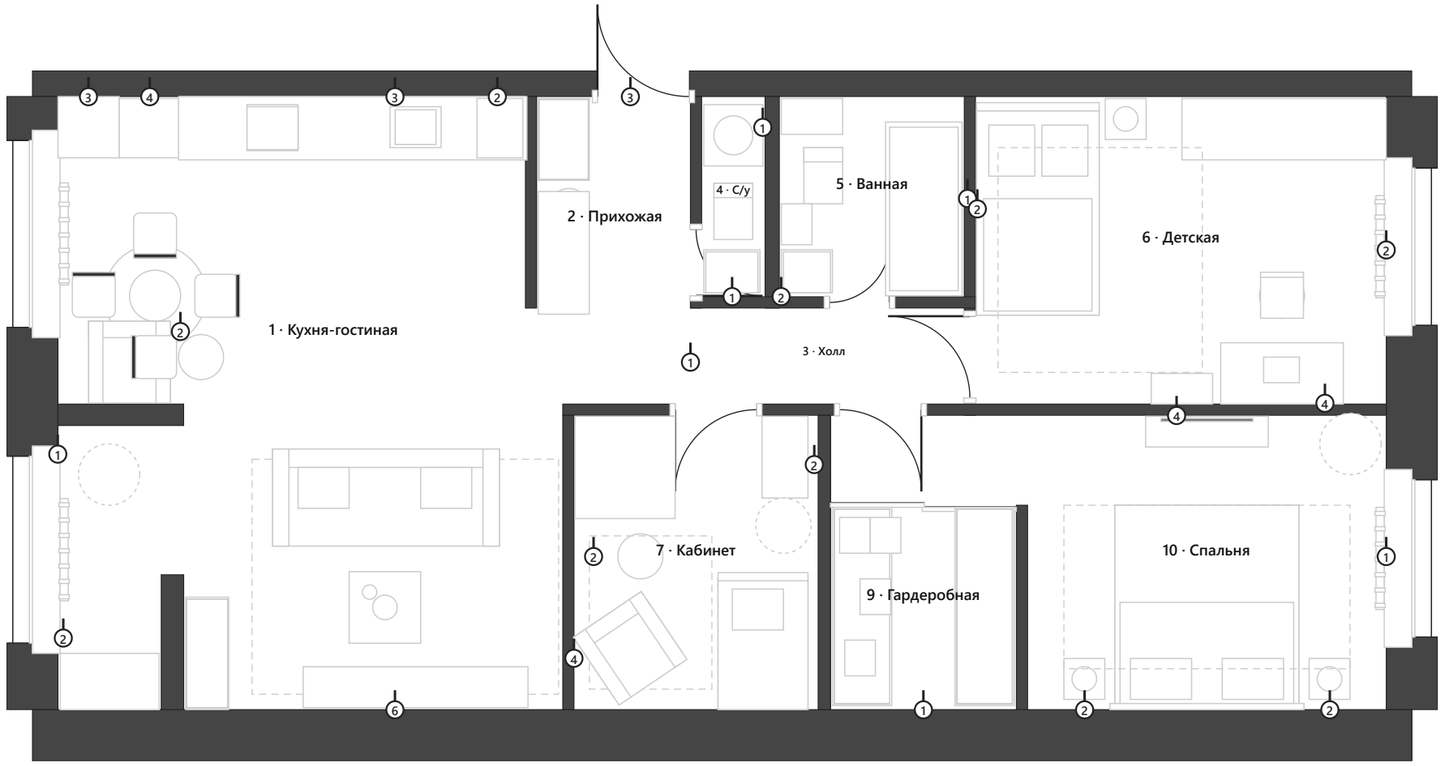


Зона	Розеток	Высота от ч. п., мм
кухня: ряд над столешницей 1100	4	1100
кухня: фартук 1100	3	1100
холодильник / колонна (за мебелью)	3	300
ПММ	2	300
обеденная зона 300	2	300
кресло / торшер	1	300
ТВ-зона: 5 + ТВ-розетка + LAN	6	300 / 1200
витрина	2	300
у дивана	2	300
прихожая: щит	3	300
холл	1	300
стиральная машина 1000	1	1000
санузел у зеркала 1200	1	1200
ванная у зеркала 1200	2	1200
полотенцесушитель 600	1	600
детская у кровати 300 / 700	2	300 / 700
рабочий стол 300 + 1100	4	300
общие	2	300
кабинет: рабочее место 300 / 1100	4	300 / 1100
кабинет	2	300
гардеробная: утюг	1	300
спальня у кровати 700	2	700
спальня у кровати 700	2	700
ТВ-зона спальни 300 / 1200 + ТВ	4	300 / 1200
общая	1	300

Всего розеток: 58 шт. · цифра у символа — количество в блоке

Примечания

1. Высота по умолчанию 300 мм до оси; у рабочих поверхностей 1100; у зеркал 1200; за ТВ 1200 (скрытый кабель-канал к тумбе 300).
2. В санузлах — розетки IP44 на линиях с УЗО 10 мА; стиральная машина — отдельная линия.
3. Кухня: духовой шкаф, варочная панель, ПММ, холодильник — отдельные линии; варочная — 32 А.
4. Слаботочные: LAN в ТВ-зоне, кабинете и детской; роутер — в прихожей у щита; ТВ-кабель — к двум ТВ-зонам.
5. Выводы для кондиционеров — по плану кондиционирования; тёплые полы — по плану тёплых полов.

						Дизайн-проект квартиры 20, 6 этаж г. Салехард · планировочное решение №148, вариант 1	№ ДП	Лист	Листов
Изм.	Уч-к	К-во	№ Док.	Подпись	Дата		ДП-20	35	54
Дизайнер						План размещения розеток и электровыводов	**КВ 20** 3D-модель · альбом		
Рук. проекта									
Заказчик									

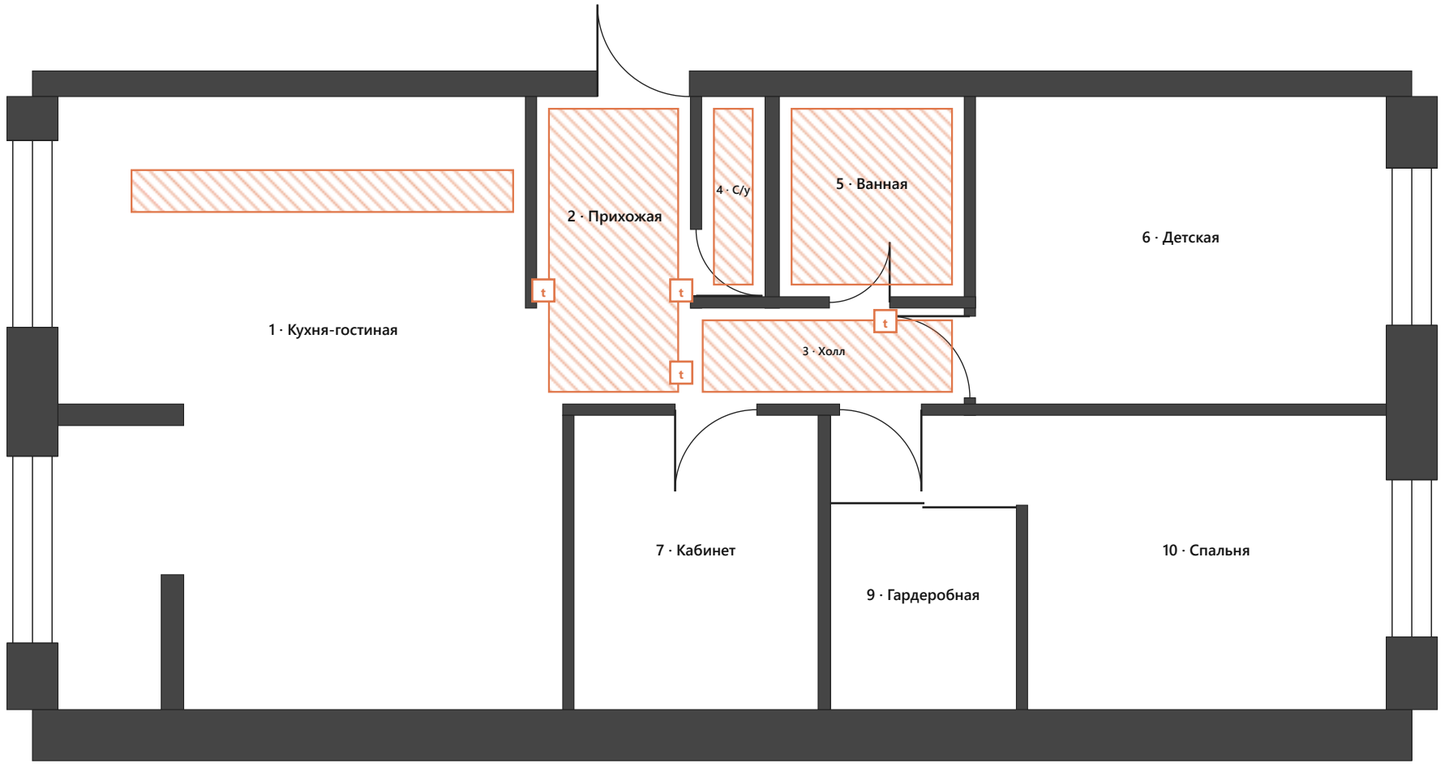

Условные обозначения


электрический тёплый пол (мат 150 Вт/м²) под керамогранитом, отступ от стен и сантехники 100 мм — ≈ 9,6 м²

t — терморегулятор с датчиком пола, 900 мм от ч. п. — 4 шт.

Примечания

1. Зоны: прихожая, холл, оба санузла и полоса вдоль кухонного гарнитура (без зоны под мебелью и приборами).
2. Под инженерной доской тёплый пол не предусмотрен; при желании — только инфракрасная плёнка по рекомендации производителя доски.
3. Каждая зона — отдельный терморегулятор и линия от щита через УЗО 30 мА.
4. Перед заливкой стяжки — фотофиксация раскладки мата с привязками.

						Дизайн-проект квартиры 20, 6 этаж г. Салехард · планировочное решение №148, вариант 1	№ ДП	Лист	Листов
Изм.	Уч-к	К-во	№ Док.	Подпись	Дата		ДП-20	36	54
Дизайнер						План тёплого пола	**КВ 20** 3D-модель · альбом		
Рук. проекта									
Заказчик									

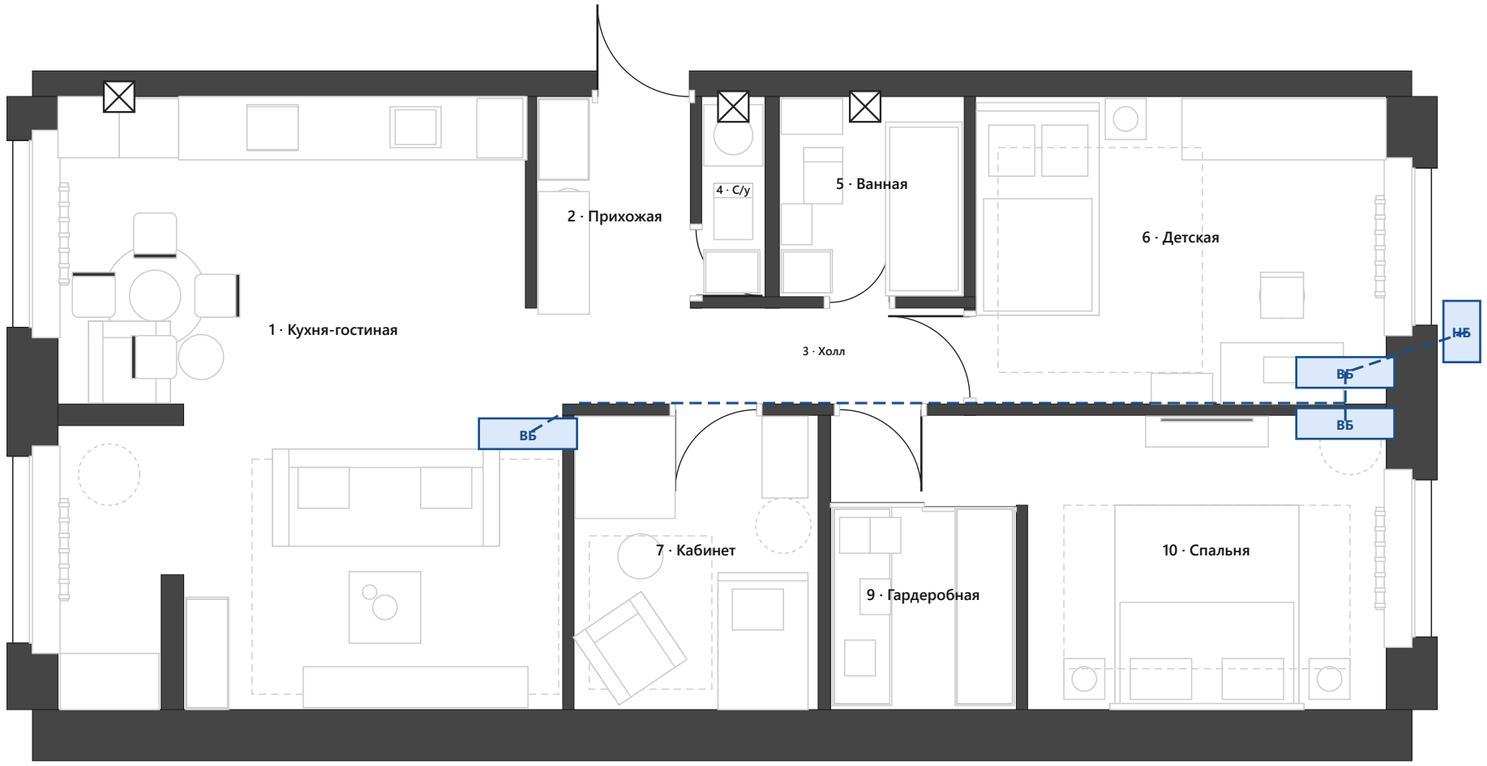

Условные обозначения

- ВБ — внутренний настенный блок мульти-сплит-системы (3 шт.); НБ — наружный блок на фасаде (1 шт.), место — по согласованию с УК
- трасса фреонопровода и дренажа в штробе / за потолком, дренаж — в канализацию с сифоном
- вентканал / вытяжка: санузлы (вентиляторы с таймером), кухня — вытяжка над плитой в вентканал

Примечания

1. Мульти-сплит 3 × 2,5 кВт с одним наружным блоком; трассы закладываются до штукатурки.
2. Внутренние блоки не направлять на кровати и рабочие места; высота установки — 200 мм от потолка.
3. Приточные клапаны — в оконных блоках жилых комнат.
4. Наличие и положение вентканалов проверить по факту; на 3D-модели они не показаны.

						Дизайн-проект квартиры 20, 6 этаж г. Салехард · планировочное решение №148, вариант 1	№ ДП	Лист	Листов
Изм.	Уч-к	К-во	№ Док.	Подпись	Дата		ДП-20	37	54
Дизайнер						План кондиционирования и вентиляции	**КВ 20** 3D-модель · альбом		
Рук. проекта									
Заказчик									




Марка	Помещение	Проём, мм	Полотно	шт.
Д1	Входная	900 × 2100	металлическая, графит, с терморазрывом; открывание наружу	1
Д2	Гостевой санузел	650 × 2100	распашная, скрытый короб, полотно в цвет стен, с вентрешёткой / зазором 20 мм	1
Д3	Ванная	600 × 2100	распашная, скрытый короб, полотно в цвет стен	1
Д4	Детская	800 × 2100	распашная, скрытый короб, эмаль RAL 9001	1
Д5	Кабинет	800 × 2100	распашная, скрытый короб, эмаль RAL 9001	1
Д6	Спальня	800 × 2100	распашная, скрытый короб, эмаль RAL 9001	1
Д7	Гардеробная	2 × 920 × 2700	раздвижные полотна в потолочном треке, шпон дуба	1

Примечания

1. Размеры проёмов — в штукатурке; размер полотна уточняется у производителя по снятым замерам.
2. Фурнитура — ручки на розетке, латунь матовая; магнитные замки; в санузлах — с фиксатором.
3. Межкомнатные двери — без порогов; зазор под полотном 10 мм (в санузлах — 20 мм для вентиляции).
4. Сторона открывания — по плану (петли показаны дугой).

						Дизайн-проект квартиры 20, 6 этаж г. Салехард · планировочное решение №148, вариант 1	№ ДП	Лист	Листов
Изм.	Уч-к	К-во	№ Док.	Подпись	Дата		ДП-20	38	54
Дизайнер						План дверей спецификация дверных блоков	**КВ 20** 3D-модель · альбом		
Рук. проекта									
Заказчик									

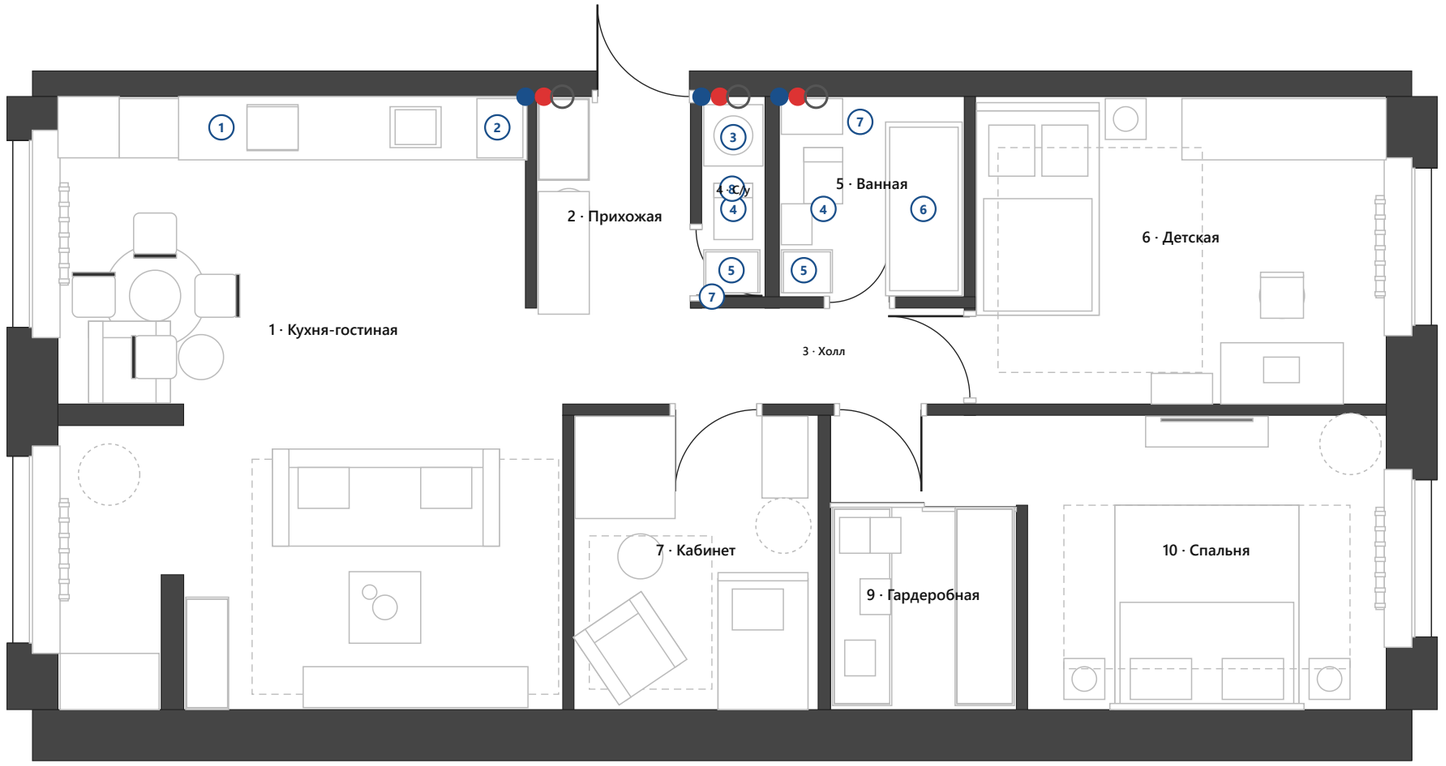


№	Прибор	шт.
1	Мойка кухонная врезная 500 × 400, смеситель с выдвижным изливом	1
2	Посудомоечная машина 450 (встр.)	1
3	Стиральная машина 600 × 600 (гостевой санузел)	1
4	Унитаз подвесной с инсталляцией, клавиша в цвет стен	2
5	Раковина подвесная / на тумбе 500 × 400, смеситель	2
6	Ванна акриловая 1700 × 750, смеситель с душевой стойкой, стеклянная шторка	1
7	Полотенцесушитель электрический 500 × 900	2
8	Водонагреватель накопительный 50 л (резерв, гостевой санузел)	1
9	Коллекторный узел, фильтры, редукторы, защита от протечек	1

Примечания


1. Положение стояков на 3D-модели не показано — уточнить по факту; выводы ХВС/ГВС/канализации (синий/красный/серый) показаны условно у стен санузлов и кухни.
2. Высоты выводов: унитаз — по инсталляции; раковина 550 (смеситель на тумбе) или 1000 (настенный); ванна — смеситель 850; СМ — 600; мойка — 450.
3. Канализация — уклон 2–3 см/м; стиральная машина — через сифон с обратным клапаном.
4. Полотенцесушители электрические — вывод 220 В на 600 мм, IP44.

						Дизайн-проект квартиры 20, 6 этаж г. Салехард · планировочное решение №148, вариант 1	№ ДП	Лист	Листов
Изм.	Уч-к	К-во	№ Док.	Подпись	Дата		ДП-20	39	54
Дизайнер						План сантехнического оборудования и спецификация	**КВ 20** 3D-модель · альбом		
Рук. проекта									
Заказчик									


Вид А

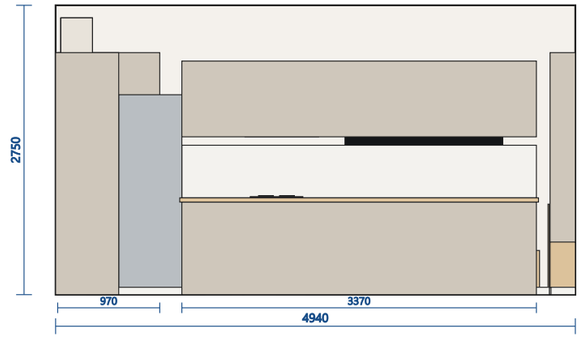

Вид Б

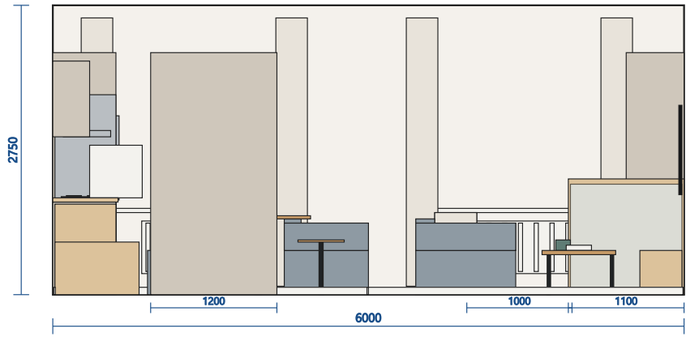

Вид В

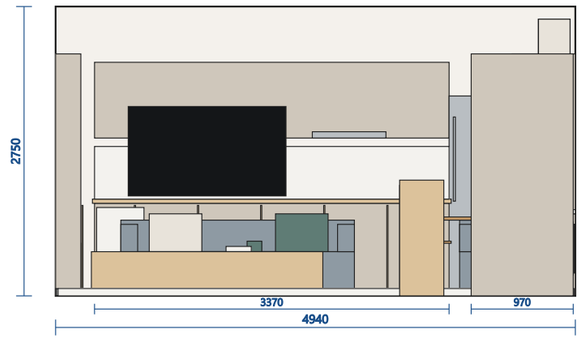


Вид Г



Отделка · Кухня-гостиная


С-1	краска матовая моющаяся, оттенок greige (RAL 9001 / 1013)
С-2	фартук кухни: керамогранит под светлый камень в цвет столешницы
С-3	ТВ-стена: панели МДФ, шпон дуба / рейки
Пл-1	плинтус МДФ 80 мм в цвет стен

Развёртки построены по 3D-модели: мебель показана в проекции на стену; виды А–Г — по ключ-плану. Размеры — в штукатурке, до контрольного обмера.

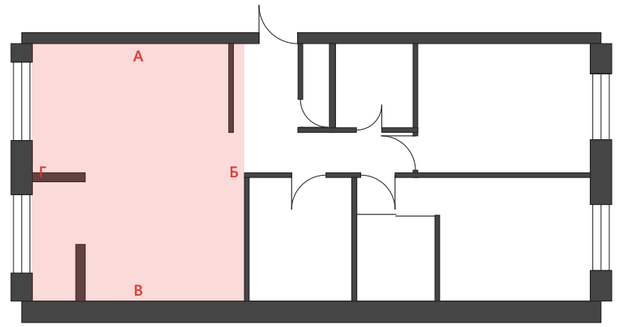


						Дизайн-проект квартиры 20, 6 этаж г. Салехард · планировочное решение №148, вариант 1	№ ДП	Лист	Листов
Изм.	Уч-к	К-во	№ Док.	Подпись	Дата		**ДП-20**	**40**	**54**
Дизайнер						Развёртки стен кухни-гостиной	**КВ 20** 3D-модель · альбом		
Рук. проекта									
Заказчик									


Вид А

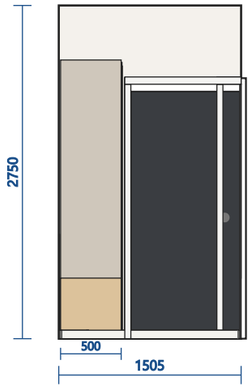


Вид Б

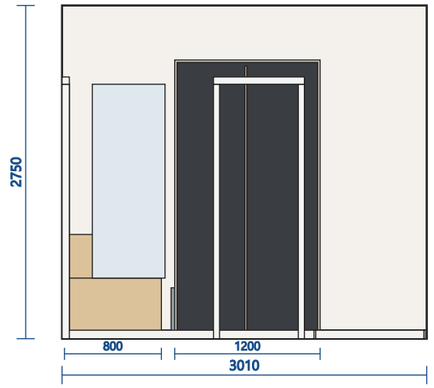

Вид В

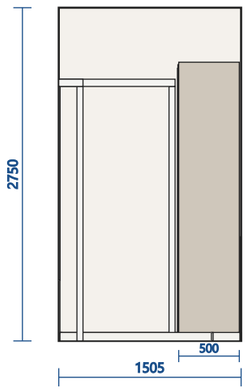

Вид Г

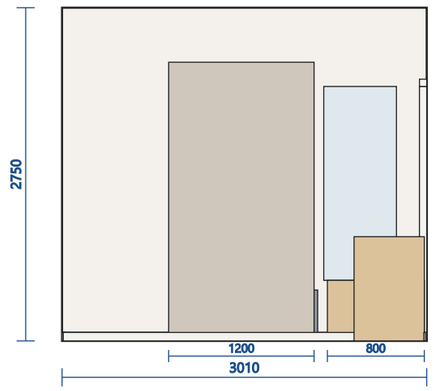


Отделка · Прихожая

С-1 краска матовая моющаяся, оттенок greige


Пл-1 плинтус МДФ 80 мм в цвет стен

Развёртки построены по 3D-модели: мебель показана в проекции на стену; виды А–Г — по ключ-плану. Размеры — в штукатурке, до контрольного обмера.

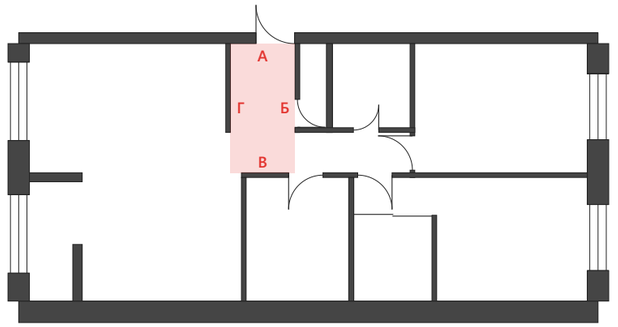


						Дизайн-проект квартиры 20, 6 этаж г. Салехард · планировочное решение №148, вариант 1	№ ДП	Лист	Листов
Изм.	Уч-к	К-во	№ Док.	Подпись	Дата		**ДП-20**	**41**	**54**
Дизайнер						Развёртки стен прихожей	**КВ 20** 3D-модель · альбом		
Рук. проекта									
Заказчик									


Вид А

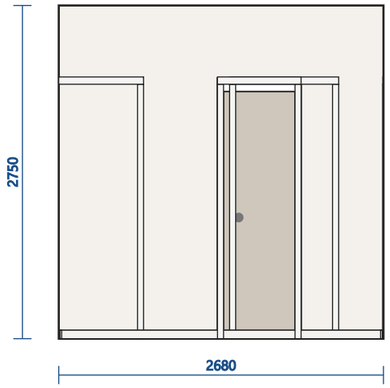


Вид Б

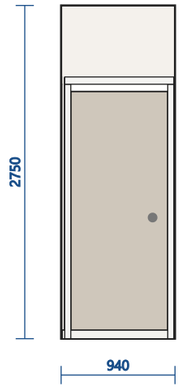

Вид В

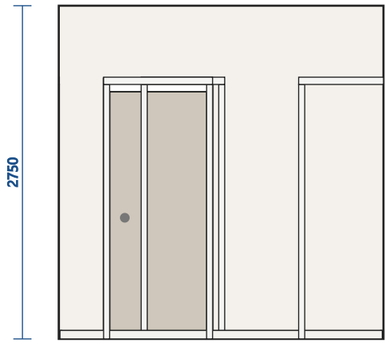

Вид Г

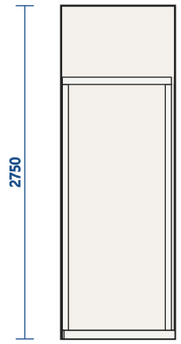


Отделка · Холл

С-1 краска матовая моющаяся, оттенок greige


Пл-1 плинтус МДФ 80 мм в цвет стен

Развёртки построены по 3D-модели: мебель показана в проекции на стену; виды А–Г — по ключ-плану. Размеры — в штукатурке, до контрольного обмера.

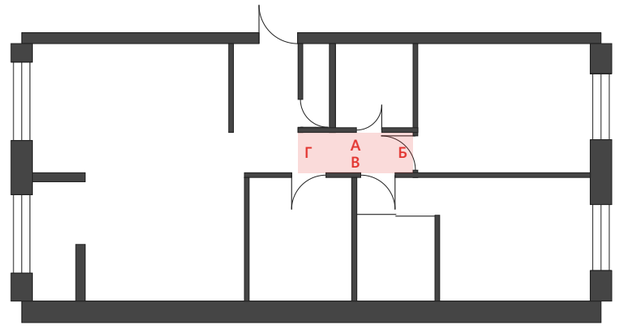


						Дизайн-проект квартиры 20, 6 этаж г. Салехард · планировочное решение №148, вариант 1	№ ДП	Лист	Листов
Изм.	Уч-к	К-во	№ Док.	Подпись	Дата		**ДП-20**	**42**	**54**
Дизайнер						Развёртки стен холла	**КВ 20** 3D-модель · альбом		
Рук. проекта									
Заказчик									

Вид А

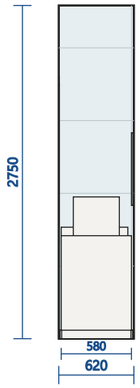

Вид Б

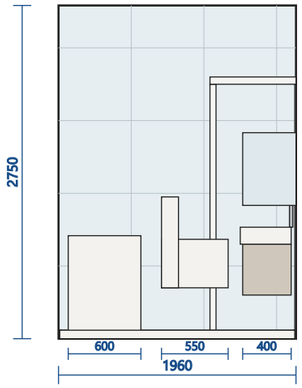


Вид В

Вид Г

Отделка · Гостевой санузел


К-1	керамогранит 600 × 1200 под светлый камень (стены по периметру до потолка)
К-2	акцент: керамогранит под дерево, зона ванны / зеркала
Пл	плинтус не предусмотрен — плитка до пола

Развёртки построены по 3D-модели: мебель показана в проекции на стену; виды А–Г — по ключ-плану. Размеры — в штукатурке, до контрольного обмера.

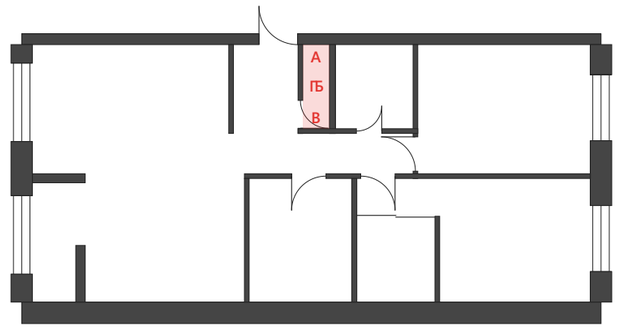


						Дизайн-проект квартиры 20, 6 этаж г. Салехард · планировочное решение №148, вариант 1	№ ДП	Лист	Листов
Изм.	Уч-к	К-во	№ Док.	Подпись	Дата		**ДП-20**	**43**	**54**
Дизайнер						Развёртки стен гостевого санузла	**КВ 20** 3D-модель · альбом		
Рук. проекта									
Заказчик									


Вид А

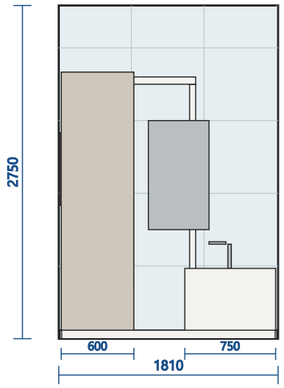


Вид Б

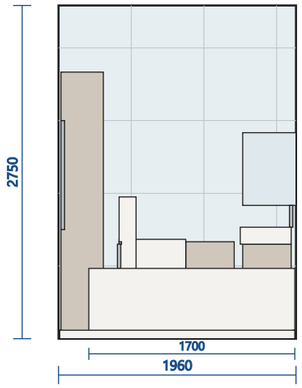

Вид В

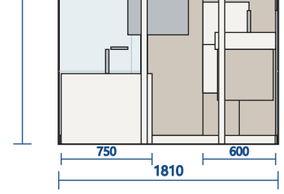


Вид Г

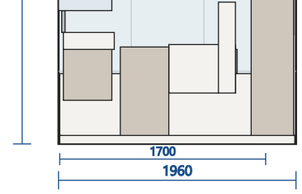

Отделка · Ванная


К-1	керамогранит 600 × 1200 под светлый камень (стены по периметру до потолка)
К-2	акцент: керамогранит под дерево, зона ванны / зеркала
Пл	плинтус не предусмотрен — плитка до пола

Развёртки построены по 3D-модели: мебель показана в проекции на стену; виды А–Г — по ключ-плану. Размеры — в штукатурке, до контрольного обмера.

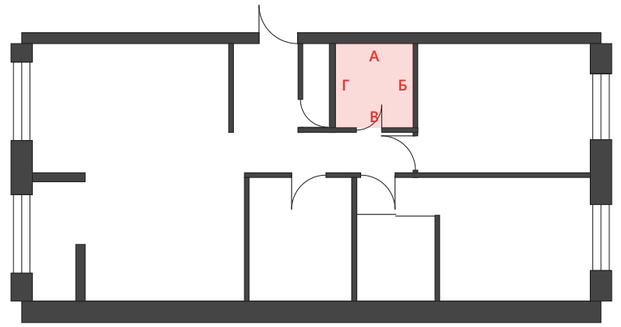


						Дизайн-проект квартиры 20, 6 этаж г. Салехард · планировочное решение №148, вариант 1	№ ДП	Лист	Листов
Изм.	Уч-к	К-во	№ Док.	Подпись	Дата		**ДП-20**	**44**	**54**
Дизайнер						Развёртки стен ванной	**КВ 20** 3D-модель · альбом		
Рук. проекта									
Заказчик									

Вид А

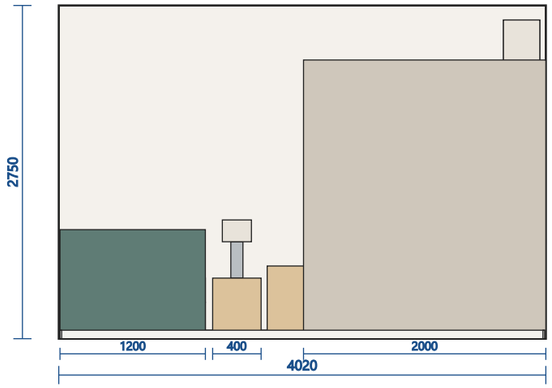

Вид Б

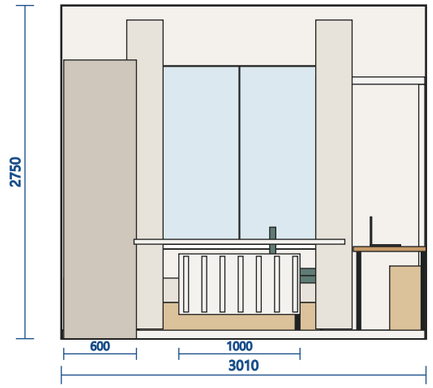


Вид В

Вид Г

Отделка · Детская


С-1	краска матовая моющаяся, оттенок greige
С-4	изголовье: мягкие панели / текстиль, акцентная стена
Пл-1	плинтус МДФ 80 мм в цвет стен

Развёртки построены по 3D-модели: мебель показана в проекции на стену; виды А–Г — по ключ-плану. Размеры — в штукатурке, до контрольного обмера.

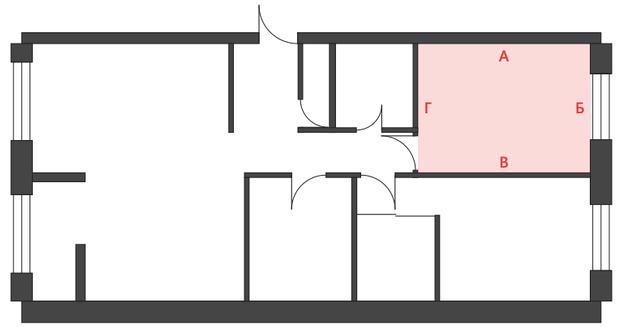


						Дизайн-проект квартиры 20, 6 этаж г. Салехард · планировочное решение №148, вариант 1	№ ДП	Лист	Листов
Изм.	Уч-к	К-во	№ Док.	Подпись	Дата		**ДП-20**	**45**	**54**
Дизайнер						Развёртки стен детской	**КВ 20** 3D-модель · альбом		
Рук. проекта									
Заказчик									

Вид А

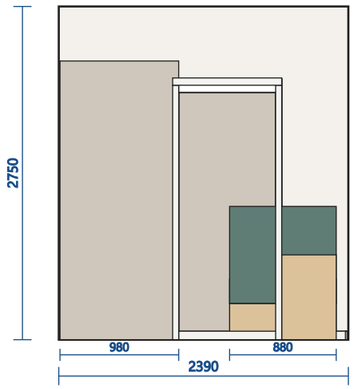

Вид Б

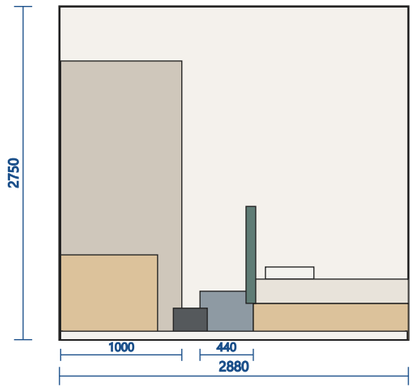

Вид В


Вид Г

Отделка · Кабинет / вторая детская

С-1 краска матовая моющаяся, оттенок greige


Пл-1 плинтус МДФ 80 мм в цвет стен

Развёртки построены по 3D-модели: мебель показана в проекции на стену; виды А–Г — по ключ-плану. Размеры — в штукатурке, до контрольного обмера.

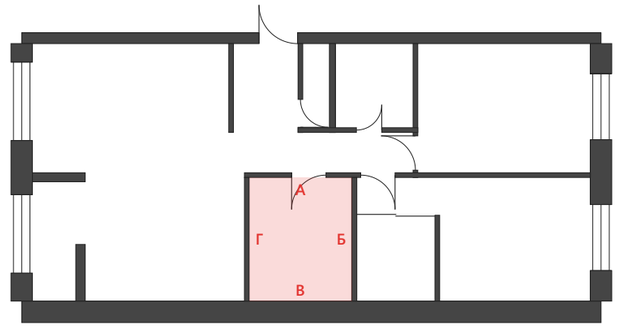


						Дизайн-проект квартиры 20, 6 этаж г. Салехард · планировочное решение №148, вариант 1	№ ДП	Лист	Листов
Изм.	Уч-к	К-во	№ Док.	Подпись	Дата		**ДП-20**	**46**	**54**
Дизайнер						Развёртки стен кабинета	**КВ 20** 3D-модель · альбом		
Рук. проекта									
Заказчик									


Вид А

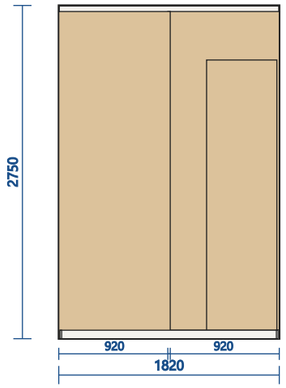


Вид Б

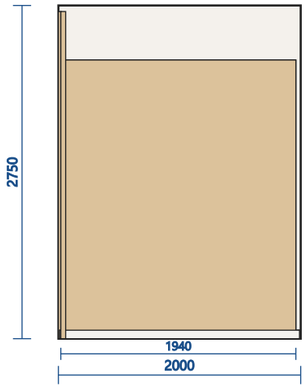

Вид В

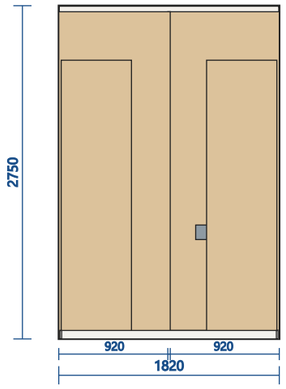

Вид Г

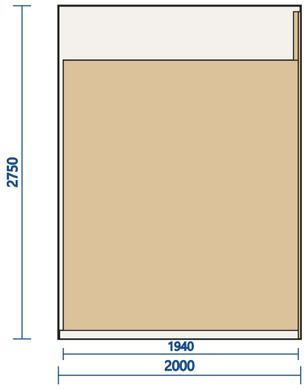


Отделка · Гардеробная

С-1 краска матовая моющаяся, оттенок greige


Пл-1 плинтус МДФ 80 мм в цвет стен

Развёртки построены по 3D-модели: мебель показана в проекции на стену; виды А–Г — по ключ-плану. Размеры — в штукатурке, до контрольного обмера.

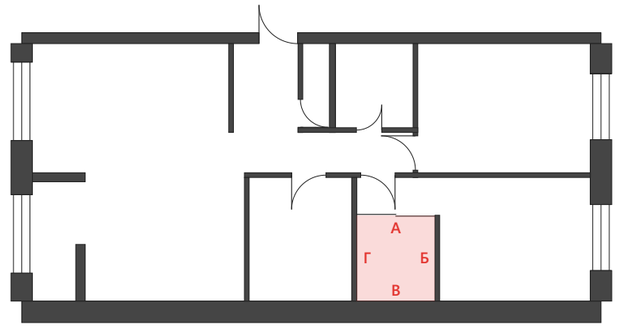


						Дизайн-проект квартиры 20, 6 этаж г. Салехард · планировочное решение №148, вариант 1	№ ДП	Лист	Листов
Изм.	Уч-к	К-во	№ Док.	Подпись	Дата		**ДП-20**	**47**	**54**
Дизайнер						Развёртки стен гардеробной	**КВ 20** 3D-модель · альбом		
Рук. проекта									
Заказчик									

Вид А

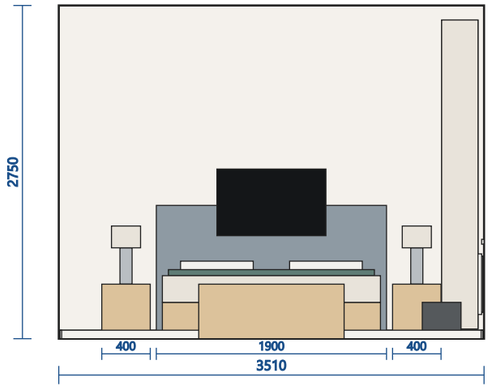

Вид Б

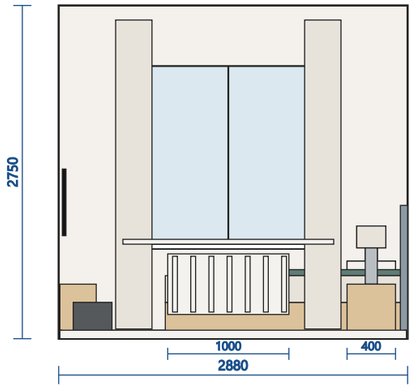


Вид В

Вид Г

Отделка · Спальня

С-1	краска матовая моющаяся, оттенок greige
С-4	изголовье: мягкие панели / текстиль, акцентная стена
Пл-1	плинтус МДФ 80 мм в цвет стен

Развёртки построены по 3D-модели: мебель показана в проекции на стену; виды А–Г — по ключ-плану. Размеры — в штукатурке, до контрольного обмера.

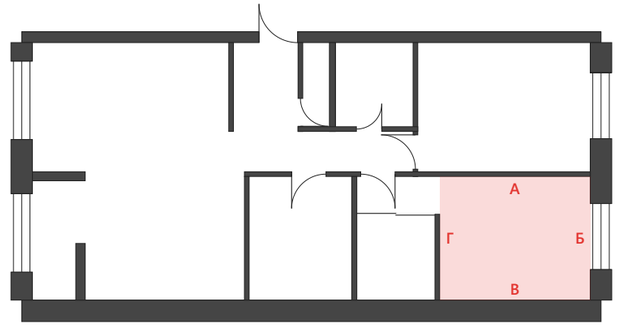

						Дизайн-проект квартиры 20, 6 этаж г. Салехард · планировочное решение №148, вариант 1	№ ДП	Лист	Листов
Изм.	Уч-к	К-во	№ Док.	Подпись	Дата		**ДП-20**	**48**	**54**
Дизайнер						Развёртки стен спальни	**КВ 20** 3D-модель · альбом		
Рук. проекта									
Заказчик									

Ведомость отделки помещений

основной вариант «Светлая»; площади — по 3D-модели, без учёта запаса

№	Помещение	S пола, м²	Пол	м²	Стены	м² (за вычетом проёмов)	Потолок	м²	Плинтус, м.п.
1	Кухня-гостиная	29,3	П-3	29,3	С-1, С-2, С-3	54,9	штукатурка, краска	29,3	20,1
2	Прихожая	4,5	П-1	4,5	С-1	21,6	штукатурка, краска	4,5	8,3
3	Холл	2,5	П-1	2,5	С-1	15,3	штукатурка, краска	2,5	6,7
4	Гостевой санузел	1,2	П-2	1,2	К-1 / К-2	11,8	ГКЛВ, краска	1,2	—
5	Ванная	3,5	П-2	3,5	К-1 / К-2	18,0	ГКЛВ, краска	3,5	—
6	Детская	12,1	П-3	12,1	С-1, С-4	34,8	штукатурка, краска	12,1	12,9
7	Кабинет / вторая детская	6,9	П-3	6,9	С-1	27,3	штукатурка, краска	6,9	9,7
8	Тамбур спальни	1,6	П-3	1,6	С-1	13,2	штукатурка, краска	1,6	5,0
9	Гардеробная	3,6	П-3	3,6	С-1	21,0	штукатурка, краска	3,6	7,0
10	Спальня	10,1	П-3	10,1	С-1, С-4	32,9	штукатурка, краска	10,1	11,8
	Итого	**75,3**				**250,8**			**81,5**


Материалы

Марка	Материал	Примечание
П-1	Керамогранит 600 × 600, светлый камень, матовый	затирка в цвет, укладка со смещением ½
П-2	Керамогранит 600 × 600 R10 (нескользящий), под светлый камень	гидроизоляция, тёплый пол
П-3	Инженерная доска, дуб натуральный, ёлочка 110 × 550	укладка ёлочкой под 45°, масло-воск
С-1	краска интерьерная матовая, моющаяся (класс 1), оттенок greige	по шпаклёвке и грунту; выкрас согласовать
С-2	керамогранит под светлый камень 600 × 1200 (фартук кухни)	в цвет столешницы
С-3	панели МДФ шпон дуба / рейки 40 × 20 с шагом 40	ТВ-стена гостиной
С-4	мягкие панели, текстиль (изголовья)	спальня, детская
К-1	керамогранит 600 × 1200 под светлый камень, матовый	санузлы, стены до потолка
К-2	керамогранит под дерево 200 × 1200	акцентные зоны санузлов
Пл-1	плинтус МДФ 80 × 16, крашенный в цвет стен	скрытое крепление
Пт-1	потолок: штукатурка, шпаклёвка, краска матовая белая	жилые помещения, h 2750
Пт-2	ГКЛВ на каркасе, краска влагостойкая	санузлы, h 2550


						Дизайн-проект квартиры 20, 6 этаж г. Салехард · планировочное решение №148, вариант 1	№ ДП	Лист	Листов
Изм.	Уч-к	К-во	№ Док.	Подпись	Дата		**ДП-20**	**49**	**54**
Дизайнер						Ведомость отделки помещений	**КВ 20** 3D-модель · альбом		
Рук. проекта									
Заказчик									

Кухонный гарнитур 4600 мм (колонна, холодильник, нижний ряд, навесные шкафы)

вид спереди

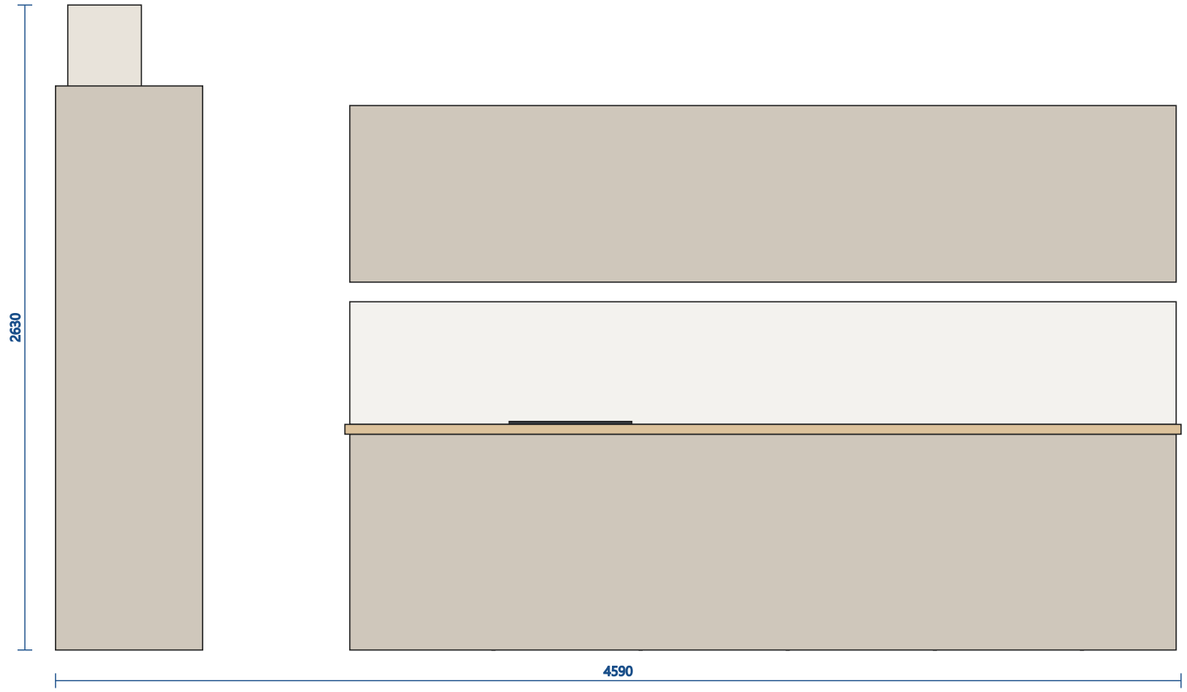

вид сбоку

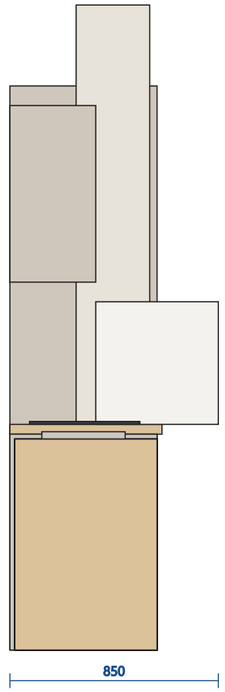

вид сверху




Материалы и примечания

Корпус	ЛДСП 16 мм, кромка ПВХ 1 мм в цвет
Фасады	МДФ, эмаль матовая greige (RAL 1013 / NCS S 2005-Y30R), интегрированные ручки
Акценты	шпон дуба натуральный, лак матовый
Столешницы	кварцевый агломерат 20 мм, светлый камень
Фурнитура	Blum / Hettich: доводчики, выдвижные ящики полного выдвижения


Чертежи — по 3D-модели, масштаб 1:25. Габариты — ориентир для изготовителя; окончательные размеры — по контрольному замеру после отделки.

						Дизайн-проект квартиры 20, 6 этаж г. Салехард · планировочное решение №148, вариант 1	№ ДП	Лист	Листов
Изм.	Уч-к	К-во	№ Док.	Подпись	Дата		ДП-20	50	54
Дизайнер						Чертежи мебели кухонный гарнитур	**KB 20** 3D-модель · альбом		
Рук. проекта									
Заказчик									

Шкаф прихожей 1200 × 500 с зеркальной стенкой и обувница 800 × 500

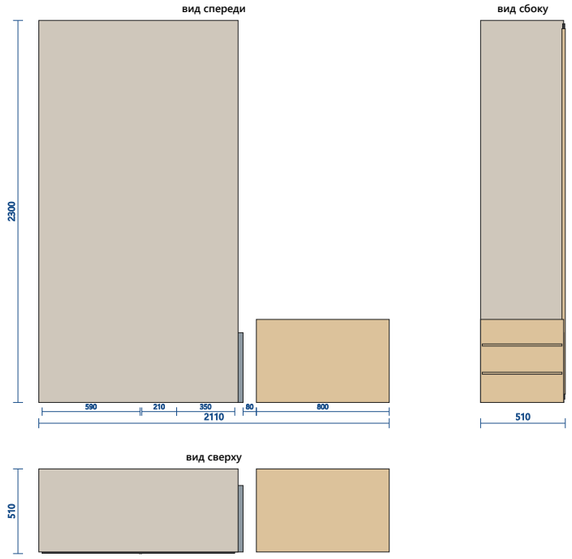

ТВ-тумба 2200 × 400 с ТВ и витрина 420 × 1100

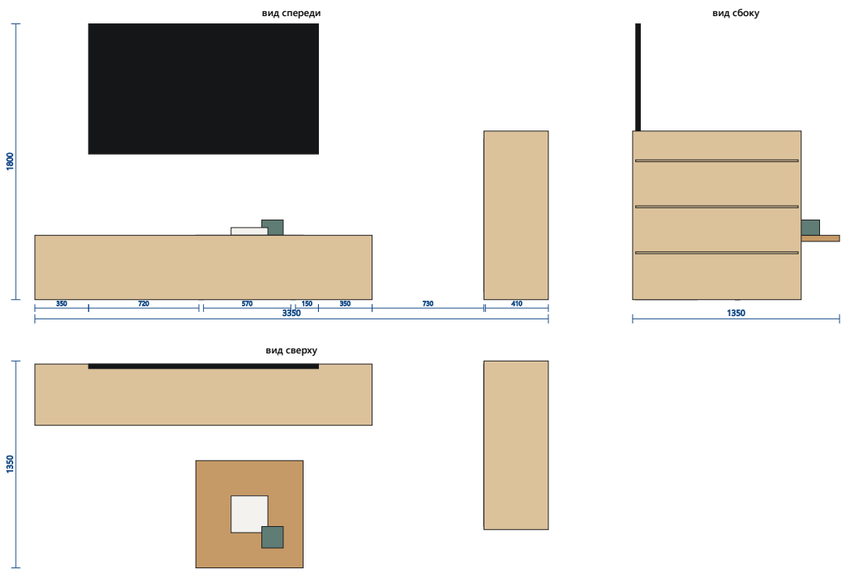

Материалы и примечания

Корпус	ЛДСП 16 мм, кромка ПВХ 1 мм в цвет
Фасады	МДФ, эмаль матовая greige (RAL 1013 / NCS S 2005-Y30R), интегрированные ручки
Акценты	шпон дуба натуральный, лак матовый
Столешницы	кварцевый агломерат 20 мм, светлый камень
Фурнитура	Blum / Hettich: доводчики, выдвижные ящики полного выдвижения


Чертежи — по 3D-модели, масштаб 1:25. Габариты — ориентир для изготовителя; окончательные размеры — по контрольному замеру после отделки.

						Дизайн-проект квартиры 20, 6 этаж г. Салехард · планировочное решение №148, вариант 1	№ ДП	Лист	Листов
Изм.	Уч-к	К-во	№ Док.	Подпись	Дата		ДП-20	51	54
Дизайнер						Чертежи мебели прихожая и гостиная	**KB 20** 3D-модель · альбом		
Рук. проекта									
Заказчик									

Детская: шкаф 2000 × 600 и кровать 1200 × 2000 с изголовьем



Детская: стол 1200 × 600 с тумбой у окна

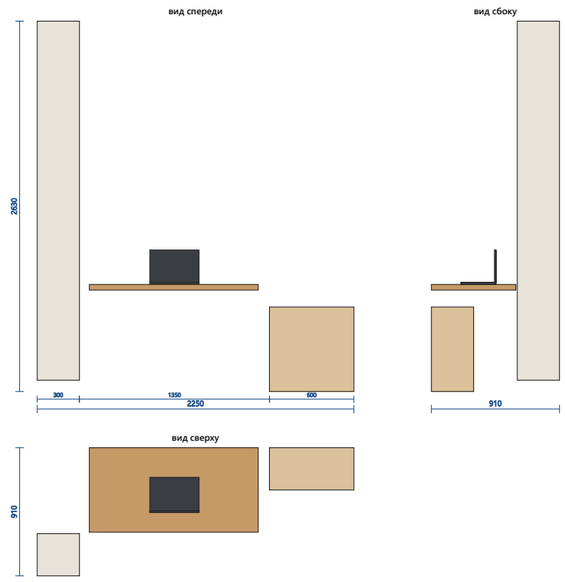


Материалы и примечания

Корпус	ЛДСП 16 мм, кромка ПВХ 1 мм в цвет
Фасады	МДФ, эмаль матовая greige (RAL 1013 / NCS S 2005-Y30R), интегрированные ручки
Акценты	шпон дуба натуральный, лак матовый
Столешницы	кварцевый агломерат 20 мм, светлый камень
Фурнитура	Blum / Hettich: доводчики, выдвижные ящики полного выдвижения


Чертежи — по 3D-модели, масштаб 1:25. Габариты — ориентир для изготовителя; окончательные размеры — по контрольному замеру после отделки.

						Дизайн-проект квартиры 20, 6 этаж г. Салехард · планировочное решение №148, вариант 1	№ ДП	Лист	Листов
Изм.	Уч-к	К-во	№ Док.	Подпись	Дата		ДП-20	52	54
Дизайнер						Чертежи мебели детская и кабинет	**KB 20** 3D-модель · альбом		
Рук. проекта									
Заказчик									

Гардеробная 1820 × 2000: стеллажи 580 мм с двух сторон, штанга

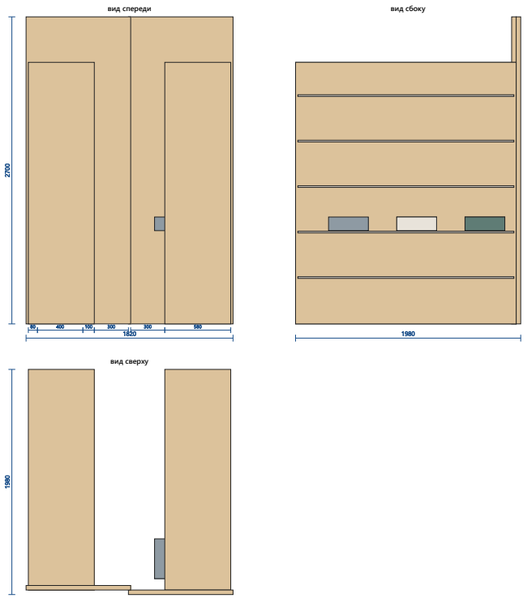

Спальня: кровать 1800 × 2000, тумбы 400, ТВ-консоль 1200 × 300

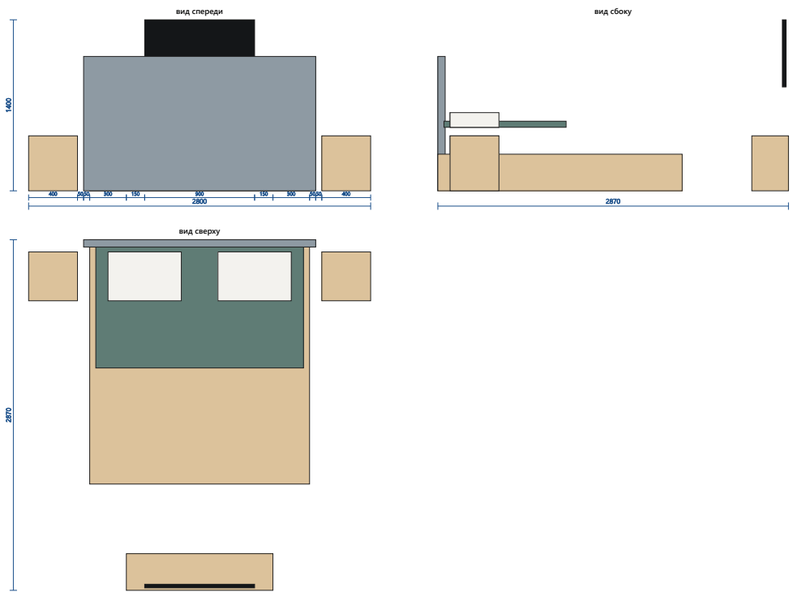


Материалы и примечания

Корпус	ЛДСП 16 мм, кромка ПВХ 1 мм в цвет
Фасады	МДФ, эмаль матовая greige (RAL 1013 / NCS S 2005-Y30R), интегрированные ручки
Акценты	шпон дуба натуральный, лак матовый
Столешницы	кварцевый агломерат 20 мм, светлый камень
Фурнитура	Blum / Hettich: доводчики, выдвижные ящики полного выдвижения


Чертежи — по 3D-модели, масштаб 1:25. Габариты — ориентир для изготовителя; окончательные размеры — по контрольному замеру после отделки.

						Дизайн-проект квартиры 20, 6 этаж г. Салехард · планировочное решение №148, вариант 1	№ ДП	Лист	Листов
Изм.	Уч-к	К-во	№ Док.	Подпись	Дата		**ДП-20**	**53**	**54**
Дизайнер						Чертежи мебели гардеробная и спальня	**KB 20** 3D-модель · альбом		
Рук. проекта									
Заказчик									

Гостевой санузел: тумба с раковиной 550 × 420

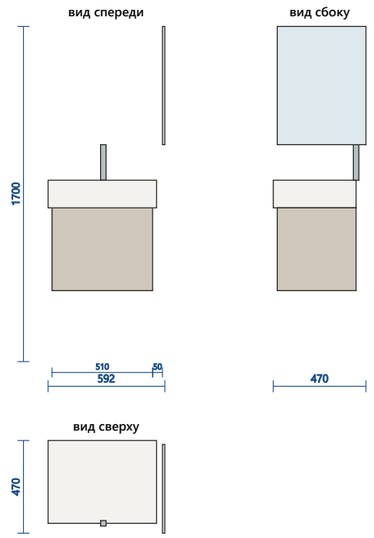

Ванная: тумба с раковиной 500 × 420, зеркало, пенал 600 × 350

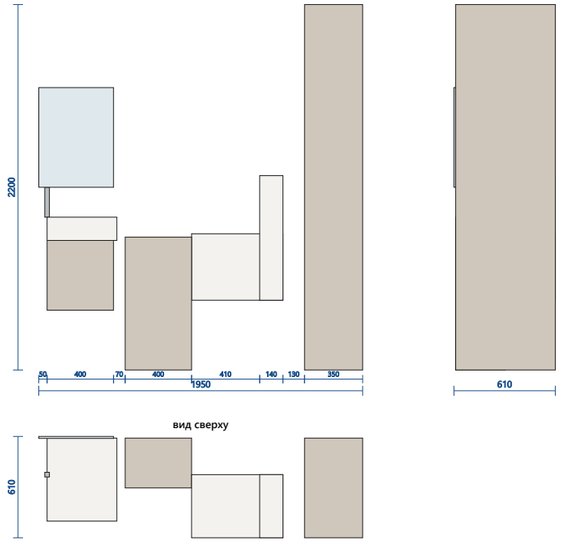

Материалы и примечания

Корпус	ЛДСП 16 мм, кромка ПВХ 1 мм в цвет
Фасады	МДФ, эмаль матовая greige (RAL 1013 / NCS S 2005-Y30R), интегрированные ручки
Акценты	шпон дуба натуральный, лак матовый
Столешницы	кварцевый агломерат 20 мм, светлый камень
Фурнитура	Blum / Hettich: доводчики, выдвижные ящики полного выдвижения

Чертежи — по 3D-модели, масштаб 1:25. Габариты — ориентир для изготовителя; окончательные размеры — по контрольному замеру после отделки.

						Дизайн-проект квартиры 20, 6 этаж г. Салехард · планировочное решение №148, вариант 1	№ ДП	Лист	Листов
Изм.	Уч-к	К-во	№ Док.	Подпись	Дата		**ДП-20**	**54**	**54**
Дизайнер						Чертежи мебели санузлы	**KB 20** 3D-модель · альбом		
Рук. проекта									
Заказчик									